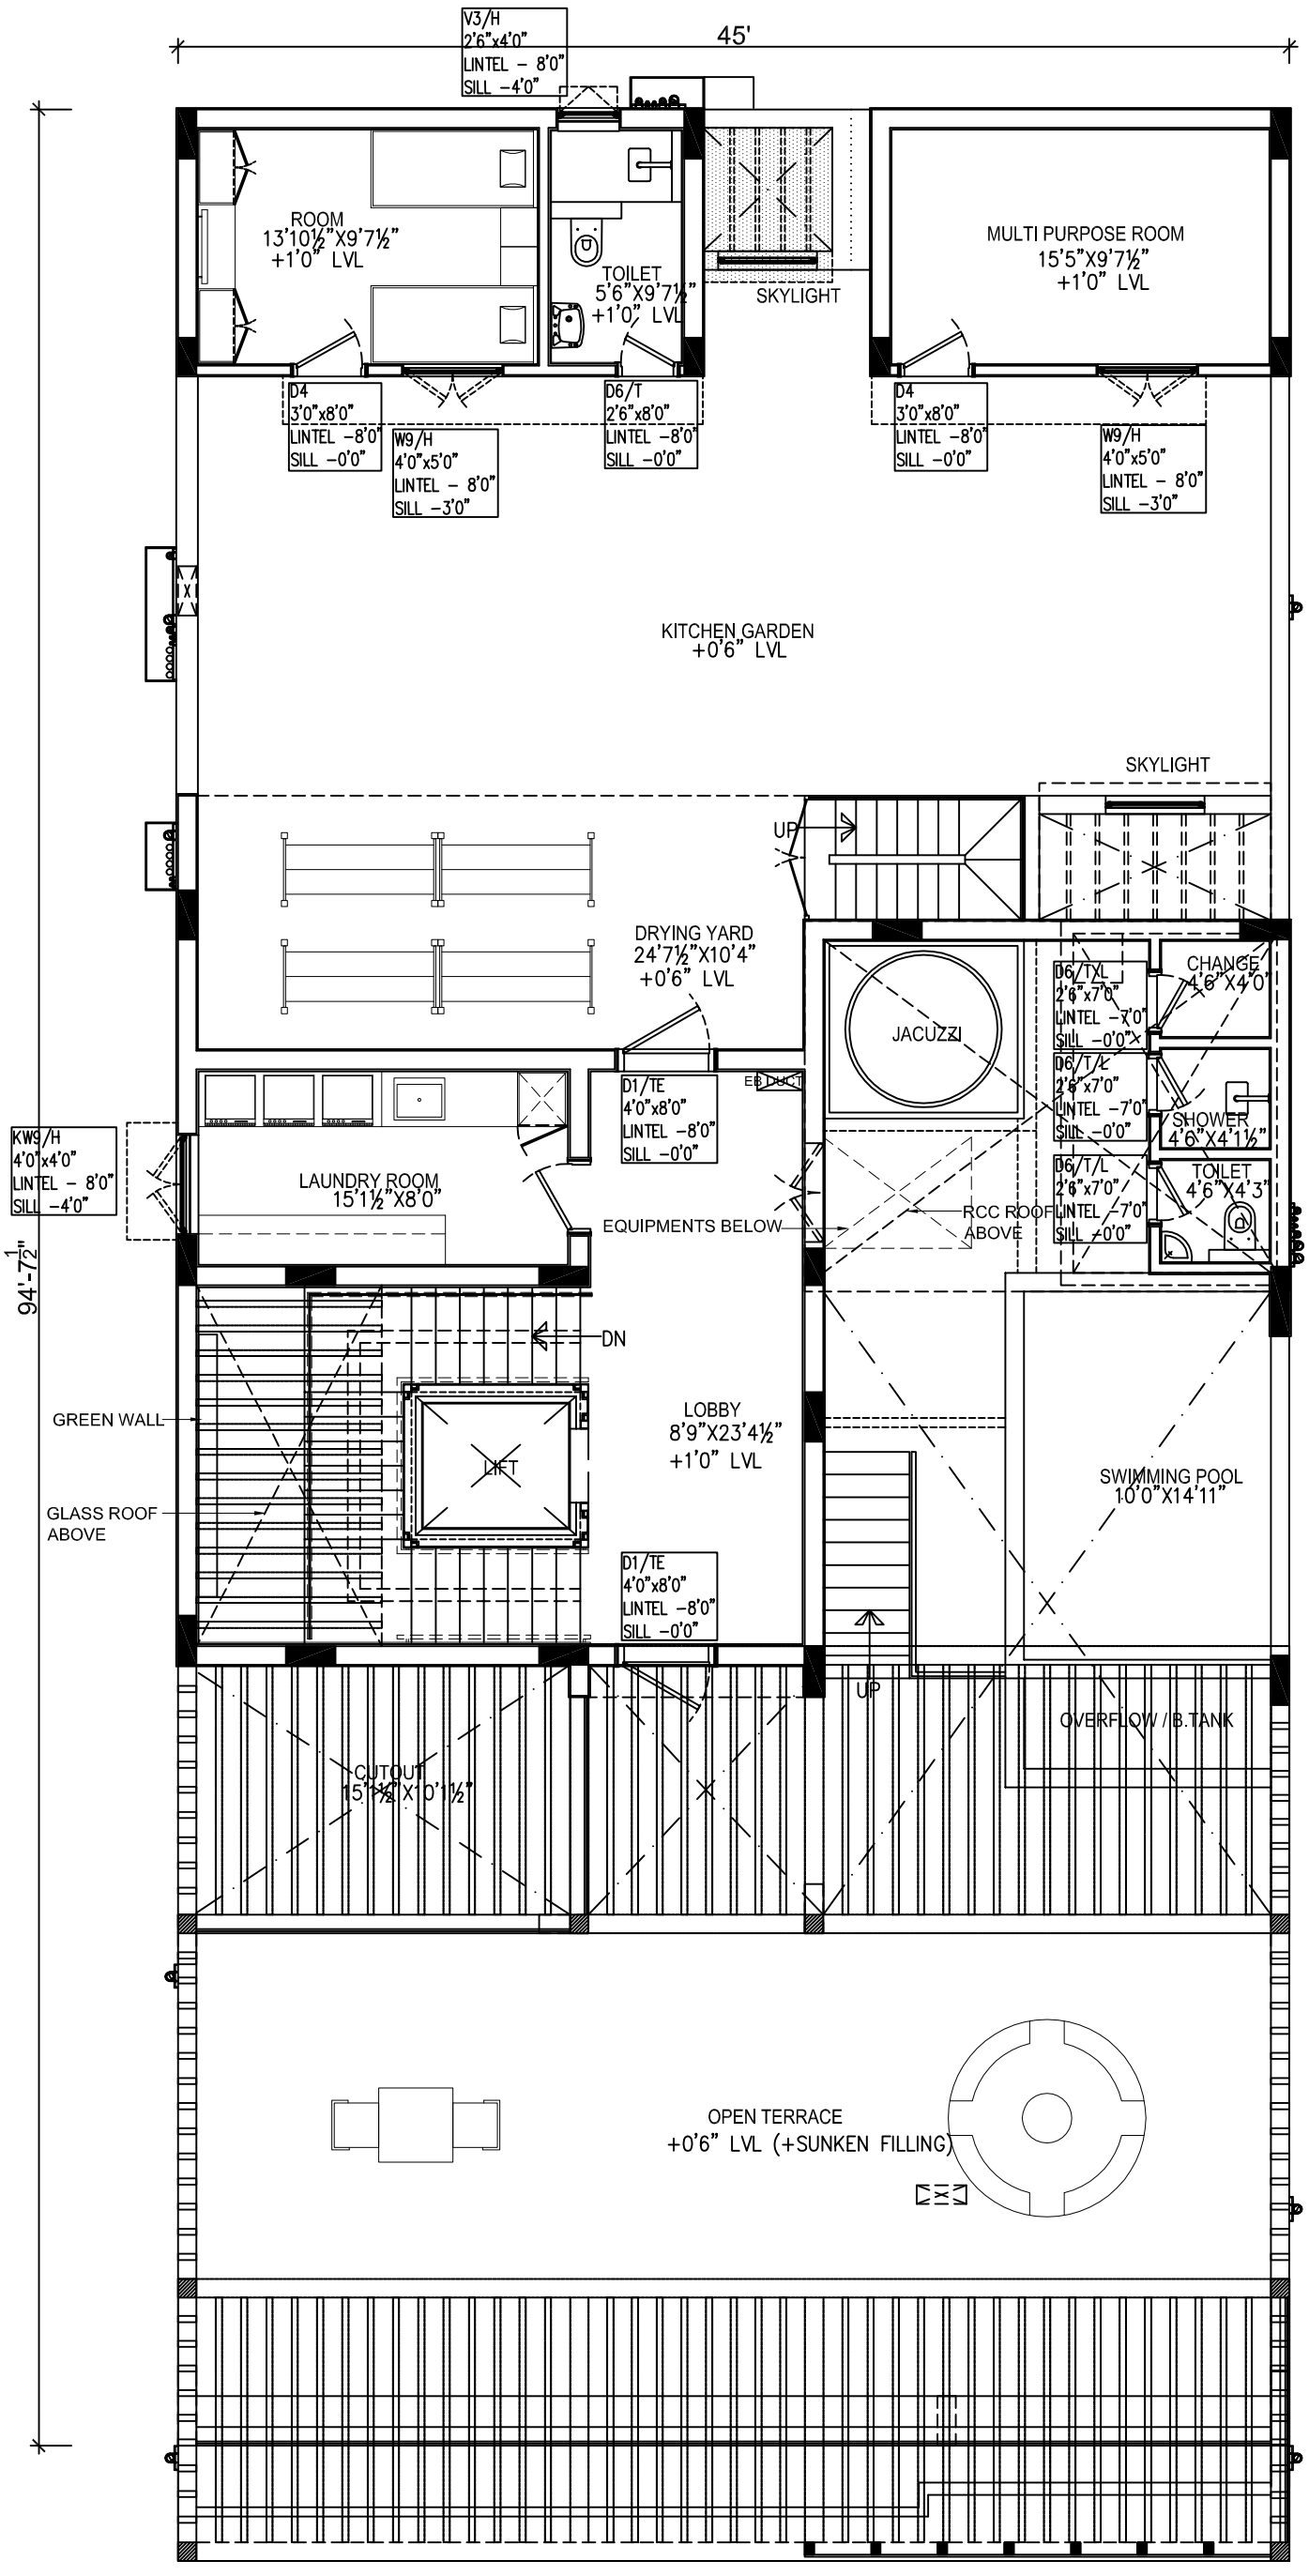

45'
V3/H
2'6"x4'0"
LINTEL – 8'0"
SILL –4'0"
ROOM
13'10½"X9'7½"
+1'0" LVL
TOILET
5'6"X9'7½"
+1'0" LVL
SKYLIGHT
MULTI PURPOSE ROOM
15'5"X9'7½"
+1'0" LVL
D4
3'0"x8'0"
LINTEL –8'0"
SILL –0'0"
W9/H
4'0"x5'0"
LINTEL – 8'0"
SILL –3'0"
D6/T
2'6"x8'0"
LINTEL –8'0"
SILL –0'0"
D4
3'0"x8'0"
LINTEL –8'0"
SILL –0'0"
W9/H
4'0"x5'0"
LINTEL – 8'0"
SILL –3'0"
KITCHEN GARDEN
+0'6" LVL
SKYLIGHT
UP
DRYING YARD
24'7½"X10'4"
+0'6" LVL
JACUZZI
D6/T/L
2'6"x7'0"
LINTEL –7'0"
SILL –0'0"
CHANGE
4'6"X4'0"
D6/T/L
2'6"x7'0"
LINTEL –7'0"
SILL –0'0"
SHOWER
4'6"X4'1½"
D6/T/L
2'6"x7'0"
LINTEL –7'0"
SILL –0'0"
TOILET
4'6"X4'3"
D1/TE
4'0"x8'0"
LINTEL –8'0"
SILL –0'0"
EB DUCT
KWS/H
4'0"x4'0"
LINTEL – 8'0"
SILL –4'0"
LAUNDRY ROOM
15'1½"X8'0"
EQUIPMENTS BELOW
RCC ROOF ABOVE
94'-7½"
DN
GREEN WALL
LIFT
LOBBY
8'9"X23'4½"
+1'0" LVL
GLASS ROOF ABOVE
SWIMMING POOL
1'0"X14'11"
D1/TE
4'0"x8'0"
LINTEL –8'0"
SILL –0'0"
UP
CUTOUT
15'1½"X10'1½"
OVERFLOW / B.TANK
OPEN TERRACE
+0'6" LVL (+SUNKEN FILLING)