CAPACITY	15 TON
PLATFORM SIZE	2500(L) X 2000(W)
POWER PACK	15 HP, 3 PH
SHUT HEIGHT	1000 MM
LIFT HEIGHT	1200 MM
OPEN HEIGHT	2200 MM
RAILING	1000 MM HEIGHT

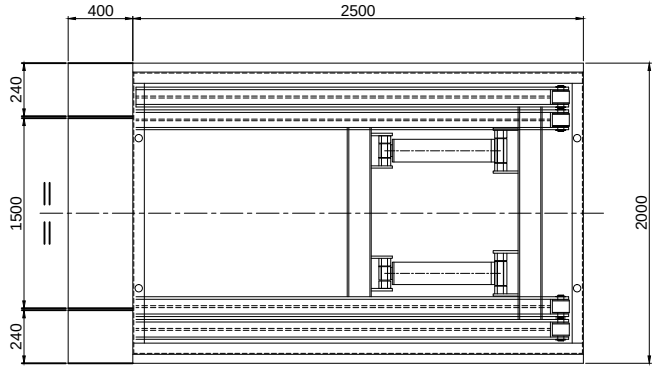

PLAN VIEW

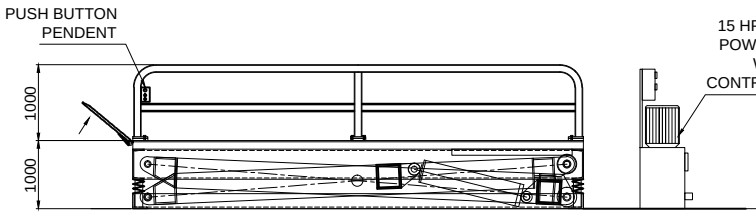

FRONT VIEW - SHUT HEIGHT

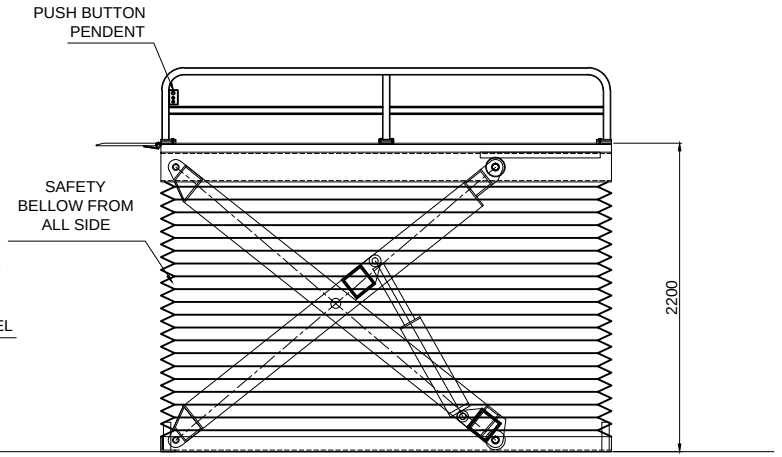

FRONT VIEW - OPEN HEIGHT

This drawing & designing is the property of NIHVA TECHNOLOGIES. Not to be sold or copied to any other concern.

TITLE: ELECTRO HYDRAULIC SCISSOR LIFT

NIHVA TECHNOLOGIES PVT. LTD.
NIHVA TECHNOLOGIES PVT. LTD. PUNE
Tel : 020 66304033
Email:- info@nihva.com
Website:- www.nihva.com

	NAME	SIGN	DATE
DRAWN	P.A		27.02.20
CHECK	G.J		27.02.20
APPROVAL			

CLIENT - Endress + Hauser Flowtec (India) Pvt. Ltd.

PROJECT - Endress + Hauser Flowtec (India) Pvt. Ltd.

SITE LOCATION - AURANGABAD

If any queries contact : design@nihva.com

DWG. NO. : NIHVA/19-20/0225 | REV- 00

ALL DIMENSION ARE IN mm

SCALE: NTS | WT: | SHEET: 01 OF 01