


PRODUCED BY AN AUTODESK EDUCATIONAL PRODUCT

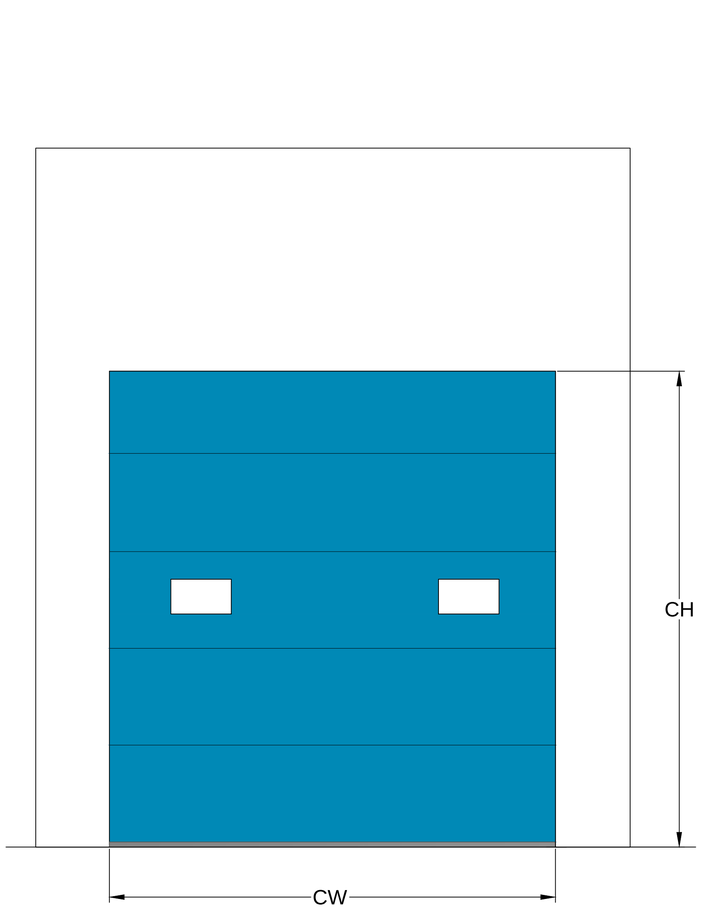


OUTSIDE ELEVATION

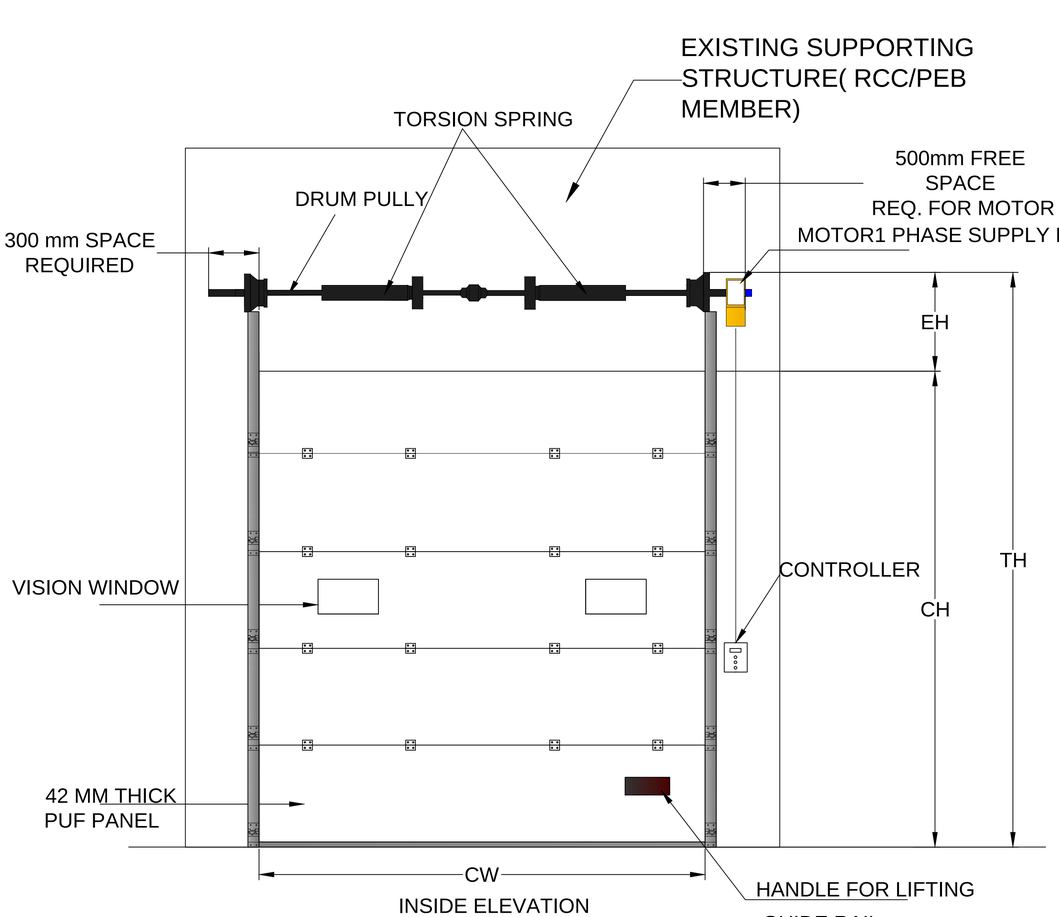

INSIDE ELEVATION

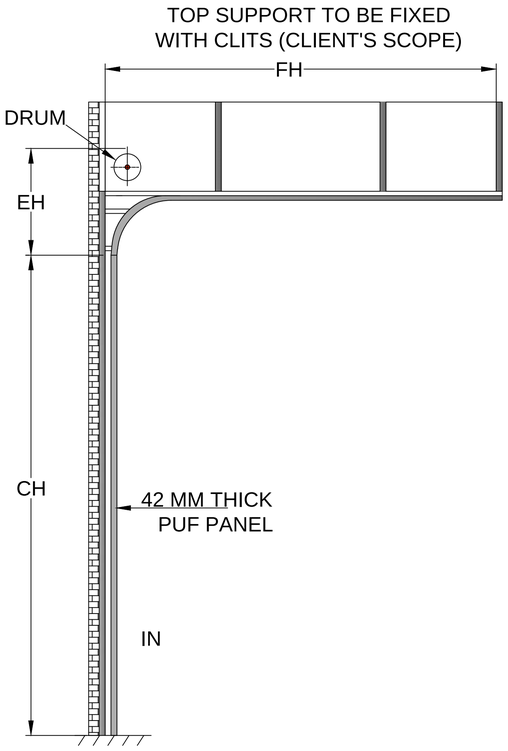


SIDE VIEW

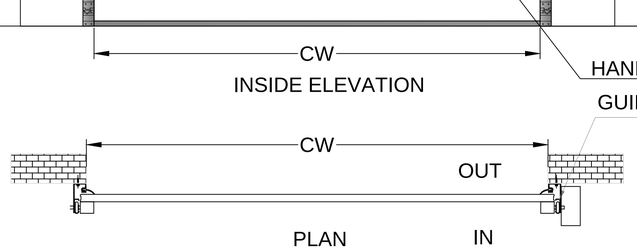

PLAN

SR NO	CLEAR WIDTH (CW)	CLEAR HEIGHT (CH)	QUANTITY	EH	FH	TH	LOCATION
1	5000	5000	2	600	5600	5600	
2	4850	4000	1	600	4600	4600	

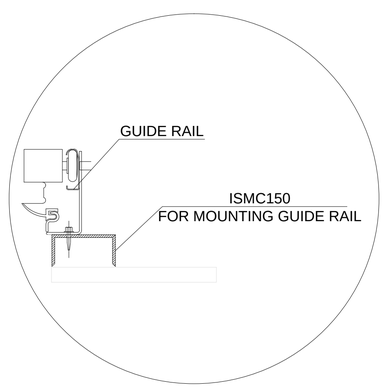

TRACK DETAILS

NOTE- 1. STRUCTURE REQUIRED FOR SECTIONAL DOOR SHALL BE IN CLIENT'S SCOPE.
2.COLOR FOR SECTIONAL DOOR PANEL WOULD BE RAL 5012(LIGHT BLUE)

This drawing & design is the property of NIHVA TECHNOLOGIES. Not be sold or copy to any other concern.

TITLE	SECTIONAL DOOR SL (MOTORIZED)		
	SIGN	DATE	
DRAWN	OMKAR	31/07/17	CLIENT - SCON PROJECTS
CHECK	SHEKHAR	31/07/17	PROJECT - BEKAERT INDUSTRIES PVT. LTD.
REV.			SITE - RAJANGAON, MIDC
APPROVAL			DWG. NO. : NIHVA/17-18/0140
If any queries contact : projects@nihva.com			SCALE: NTS / WT: / SHEET: 01 OF 01
ALL DIMENSION ARE IN mm			

NIHVA TECHNOLOGIES PVT. LTD. PUNE
Tel : 020 66304033
Email:- info@nihva.com
Website:- www.nihva.com

PRODUCED BY AN AUTODESK EDUCATIONAL PRODUCT