

Prinzipzeichnung
RapidRoll 300 plus


General Drawing RapidRoll 300 plus

ALBANY
ASSA ABLOY

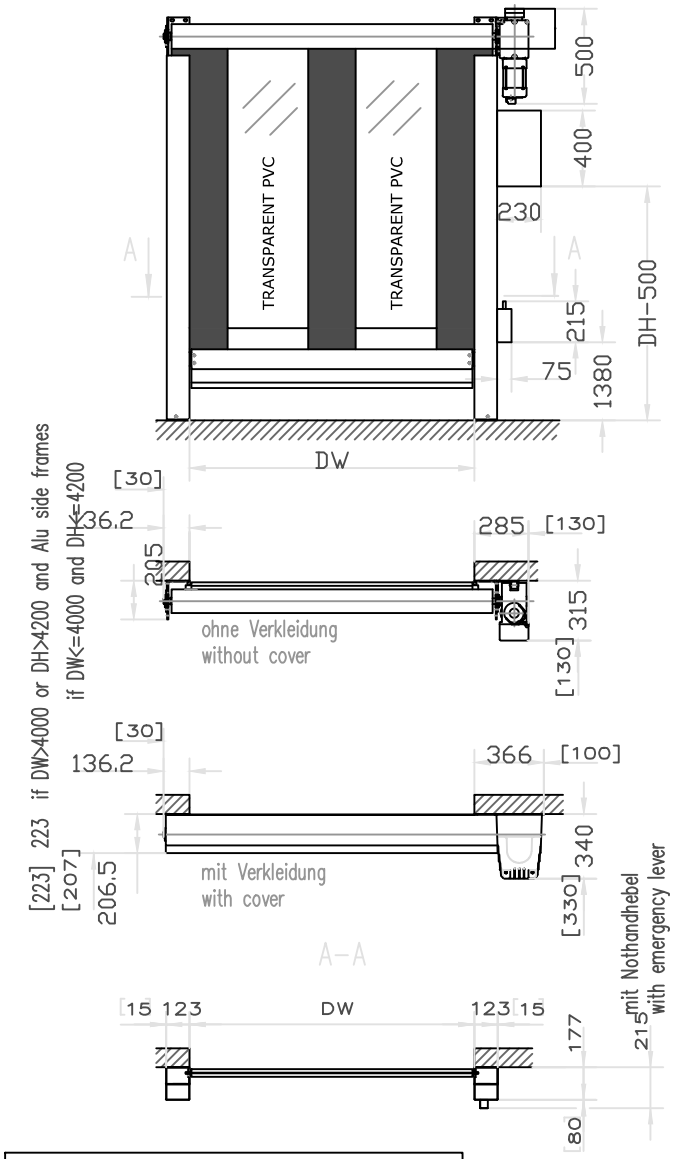


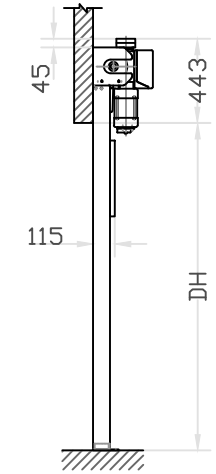

ohne Verkleidung
without cover

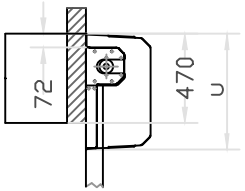

Motorverkleidung
motor cover

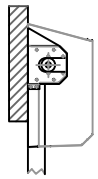

Motor- und Ballenverkleidung
Edelstahl – 30½/15½ Schr.ge

NOTES-
1. REQUIRED M.S. STRUCTURE , FITTING & ALL CIVIL WORK IS IN CLIENT SCOPE .
2. HIGH SPEED DOOR WILL BE INSTALLED AFTER READINESS OF STRUCTURE AS PER DRAWING .

SR NO	CLEAR OPENING WIDTH (DW)	CLEAR OPENING HEIGHT (DH)	QTY	LOCATION	MOTOR SIDE	MOUNTING SURFACE
1	1950	3900	1	PROCESS AREA ENTRY	RH	M.S. STRUCTURE
2	2500	4000	1	KINDER JOY TUNNEL	LH	M.S. STRUCTURE
3	3000	3900	1	KSBC PARKING	LH	M.S. STRUCTURE
4	1950	2500	1	ROCHER PACKING	RH	M.S. STRUCTURE
5	2850	3700	1	KINDER JOY PACKING	RH	M.S. STRUCTURE
6	2200	3500	1	SYRUP TUNNEL	RH	M.S. STRUCTURE
7	2400	2600	1	KINDER JOY ENTRY TUNNEL	LH	M.S. STRUCTURE

NOTE :
1. TRANSPARENT PVC WITH RED (RAL 3002) REINFORCEMENT STRIPES.
2. VERTICAL TRANSPARENT VISION PANEL.
3. SIDE FRAME - ALUMINUM PROFILES, ANODIZED.

Tolerance ±3 mm (for all dimensions)
Dimensions in [ ] ==> clearance for installation

This drawing & design is the property of NIHVA TECHNOLOGIES. Not to be sold or copied to any other concern.

TITLE - RR300 PLUS ALU HSD

NIHVA
NIHVA TECHNOLOGIES PVT. LTD.

NIHVA TECHNOLOGIES PVT. LTD. PUNE
Tel : 020 66304033
Email:- info@nihva.com
Website:- www.nihva.com

	NAME	SIGN	DATE
DRAWN	S.M.S.		8.2.2021
CHECK	A.G.		8.2.2021
APPROVED			

CLIENT - FERRERO INDIA PVT. LTD
PROJECT -
LOCATION - BARAMATI
If any queries contact:sales@nihva.com
DWG. NO. -NIHVA/20-21/0154 REV- 0
ALL DIMENSION ARE IN mm
SCALE: NTS WT: SHEET: