




SIDE VIEW

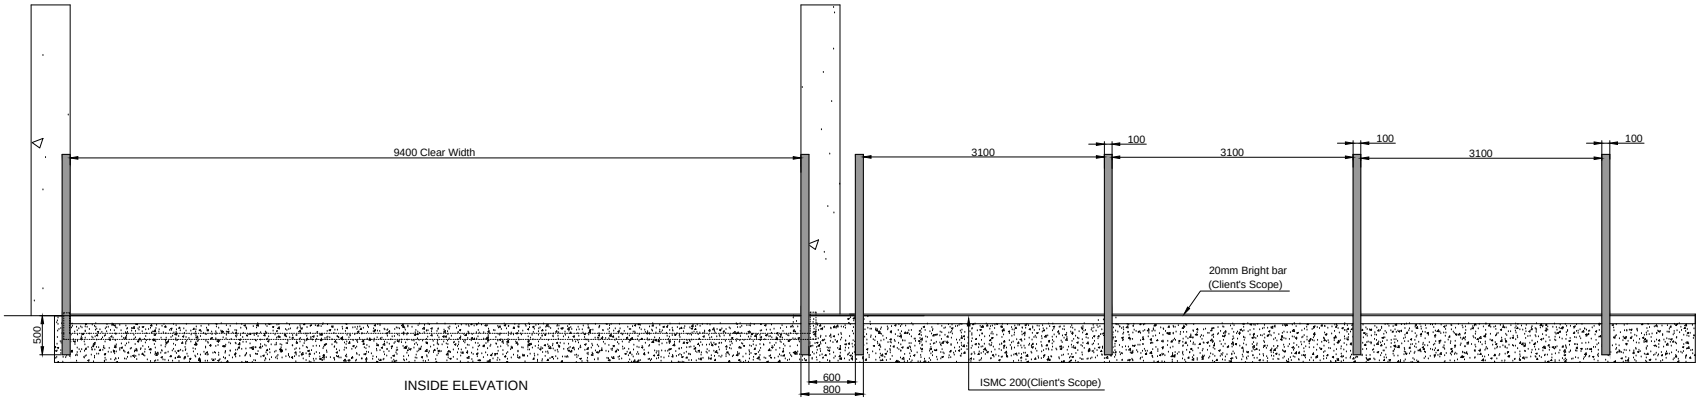

INSIDE ELEVATION

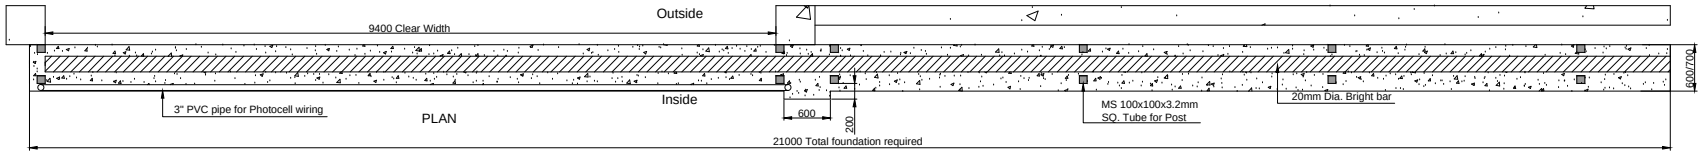

PLAN

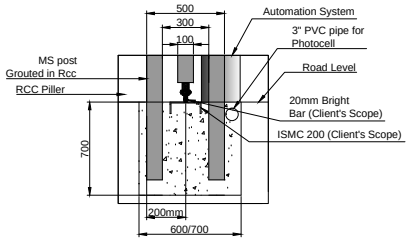

Detailed View of A

CLEAR WIDTH	CLEAR HEIGHT	QUANTITY
9400mm	1800mm	1 NOS

This drawing & designing is the property of NIHVA TECHNOLOGIES. Not to be sold or copied to any other concern.

TITLE
Foundation of Motorised Sliding gate 9.4x1.8m

NIHVA TECHNOLOGIES PVT. LTD. PUNE
Tel : 020 66304033
Email:- info@nihva.com
Website:- www.nihva.com

	SIGN	DATE
DRAWN	Omkar	10/01/18
CHECK	Shekhar	10/01/18
APPROVAL	Shekhar	10/01/18

CLIENT - Zamil Construction India Pvt. Ltd.
PROJECT - Kapci
SITE LOCATION - Banglore
DWG. NO. : NIHVA/17-18/0333 Rev- 0
If any queries contact : design@nihva.com
SCALE: NTS WT: SHEET: 01 OF 01
ALL DIMENSION ARE IN mm