




NOTE : ~ PLEASE MAINTAIN 8 MM GAP BETWEEN TWO LIP BUSHES.

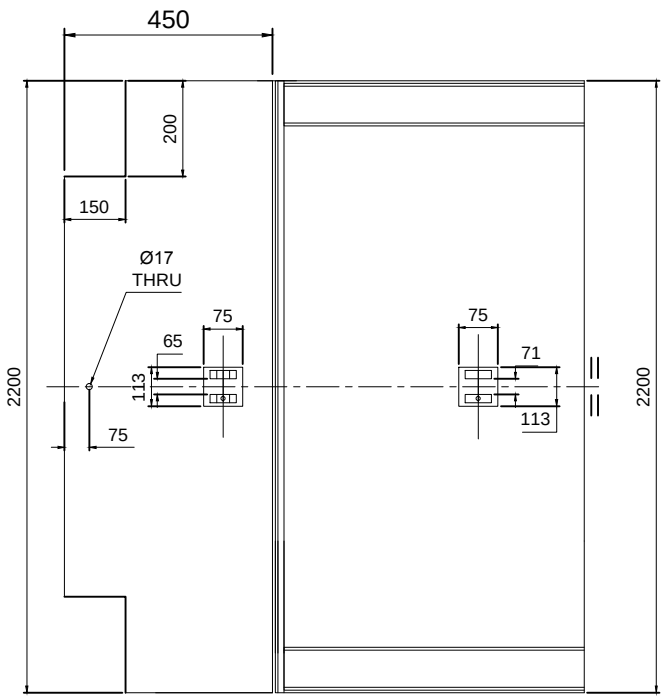

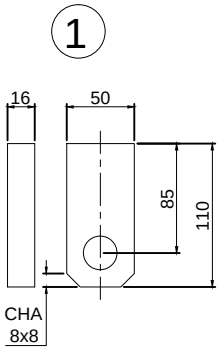

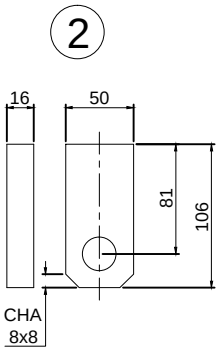

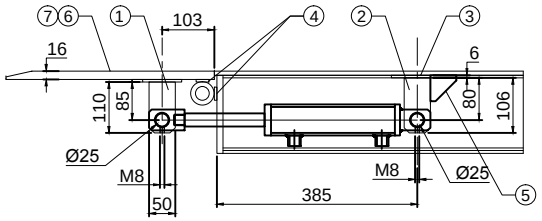

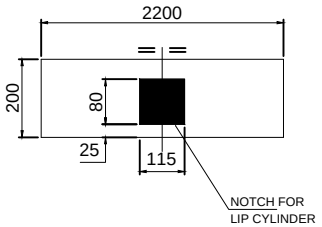

NOTE:~ MTL : MS

PART NO.	PART NAME	DESCRIPTION	QTY
1.	FLAT	50 X 16 X 113L	2 NOS
2.	FLAT	50 X 16 X 110L	2 NOS
3.	FLAT	75 X 5 X 113L	2 NOS
4.	FLAT	25 X 5 X 80L	21 NOS
5.	FLAT	50 X 10 X 50L	2 NOS
6.	CHEQ.SHEET	400 X 8 X 2200L	1 NO
7.	PLAIN SHEET	350 X 8 X 2200L	1 NO

TOLERANCE - ±5mm

This drawing & design is the property of NIHVA TECHNOLOGIES. Not to be sold or copied to any other concern.

TITLE				
LIP CYL MOUNTING				NIHVA TECHNOLOGIES PVT. LTD. PUNE
	NAME	SIGN	DATE	Tel : 020 66304033
DRAWN	P.V.A		28.06.2019	Email:- info@nihva.com
CHECK	V.M.T		28.06.2019	Website:- www.nihva.com
APPRD.				CLIENT -
If any queries contact : design@nihva.com				PROJECT - NDL456
				SITE LOCATION -
				DWG. NO. : NIHVA/19-20/VDR/096
ALL DIMENSION ARE IN mm				SCALE: NTS / WT: / REV- 0