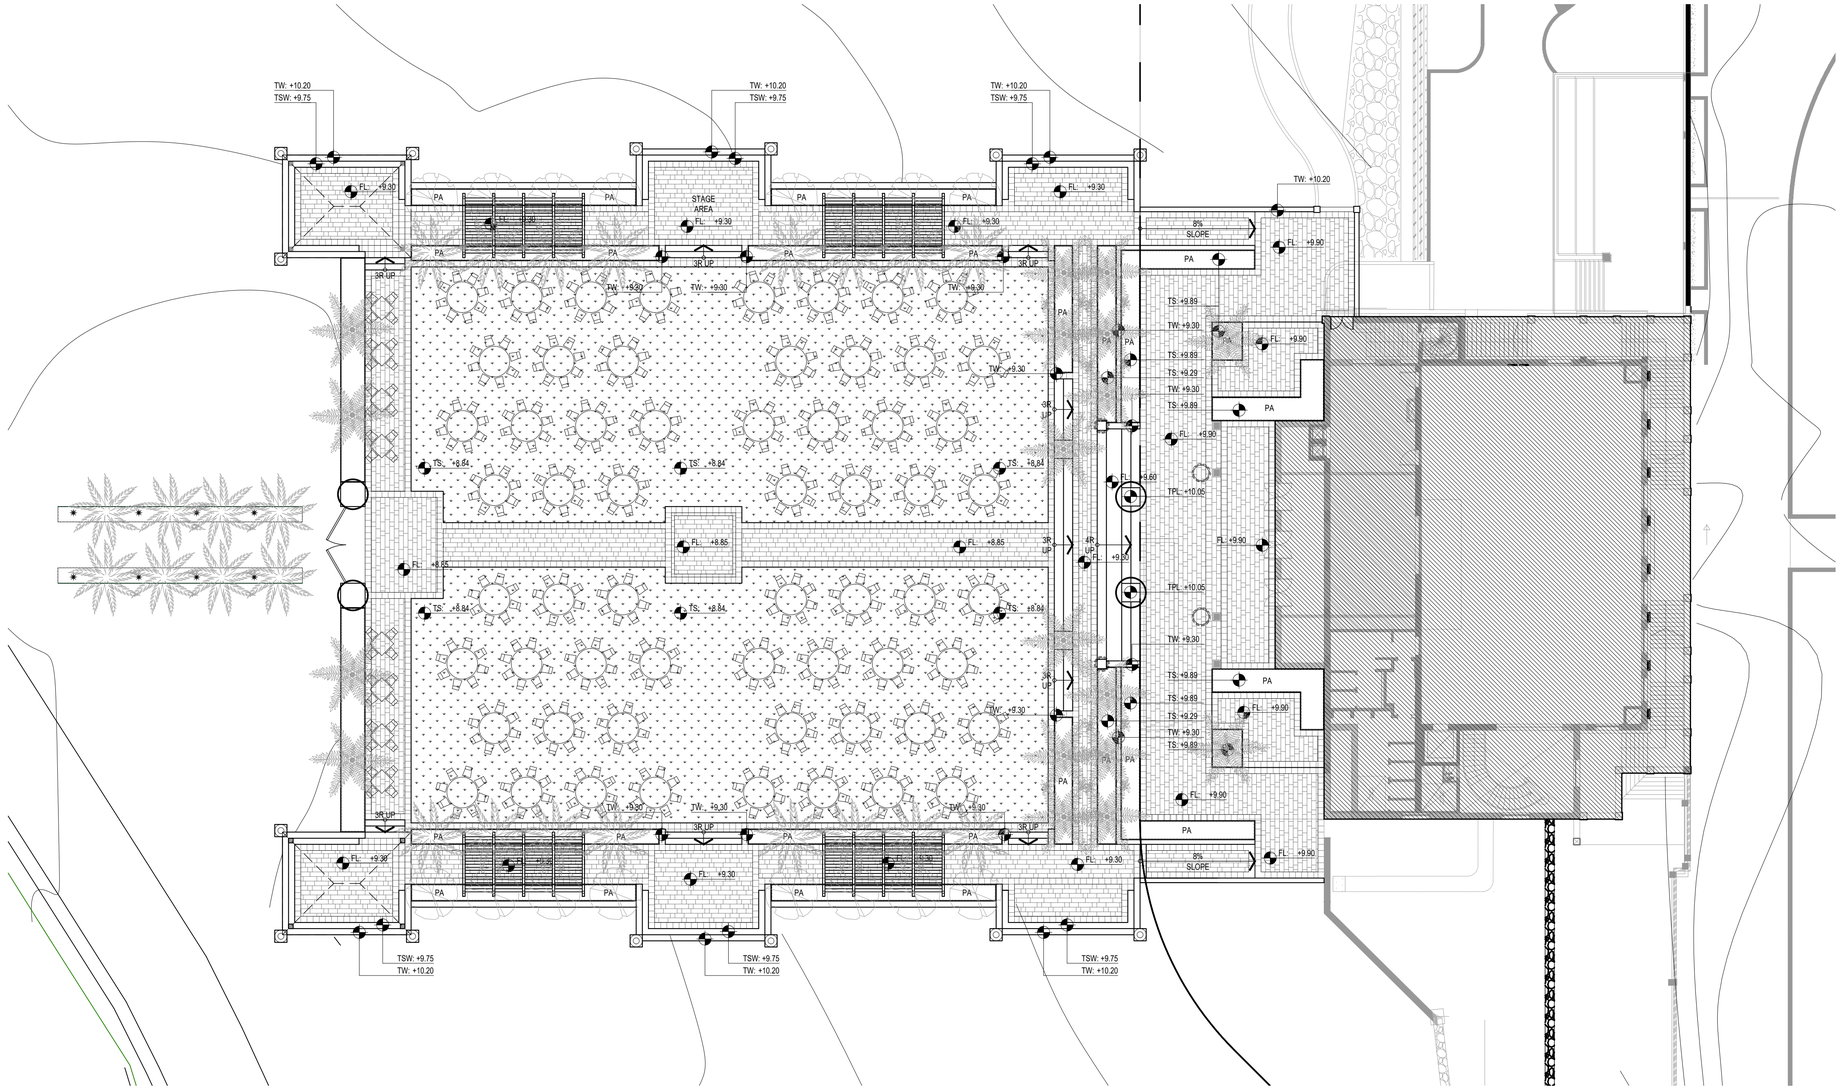


1 / 1000 GENERAL ARRANGEMENT PLAN
SCALE: 1:200

The copyright of this drawing remains with the SQM Design and may not be reproduced without prior written consent.

Figured Dimensions are to be used in preferences to scaled sizes.
All Dimensions must be checked before commencing work on site.
This Drawing is to be read in conjunction with all other relevant Drawings.
All Proposed works to be carried out in accordance with SQM Design technical specification for landscape architectural works.

KEY PLAN:

LEGEND:

PA	Planting Area
	Lawn
	Not in Scope
	Boundary Line

rev.	date	name	description
0	21-12-10	DD	100% DETAIL DESIGN

Lead Consultant:
KKD

Design Consultant:
SQUARE M DESIGN
P.O.BOX 36615, DUBAI, TEL: +971-4388758

Client:
KEF HOLDINGS

Project Name:
CHELAMBRA RESORT
INDIA

Drawing Title:
GENERAL ARRANGEMENT PLAN

Scale:	Size:	Drawn By:	Date:	Status:
1:200	A1	RI	10 DEC 2021	DD

Drawing No.

NKDG	1140	LA	DG	1000	0
Project	Project Number	Discipline	File Type	Drawing No.	Revision