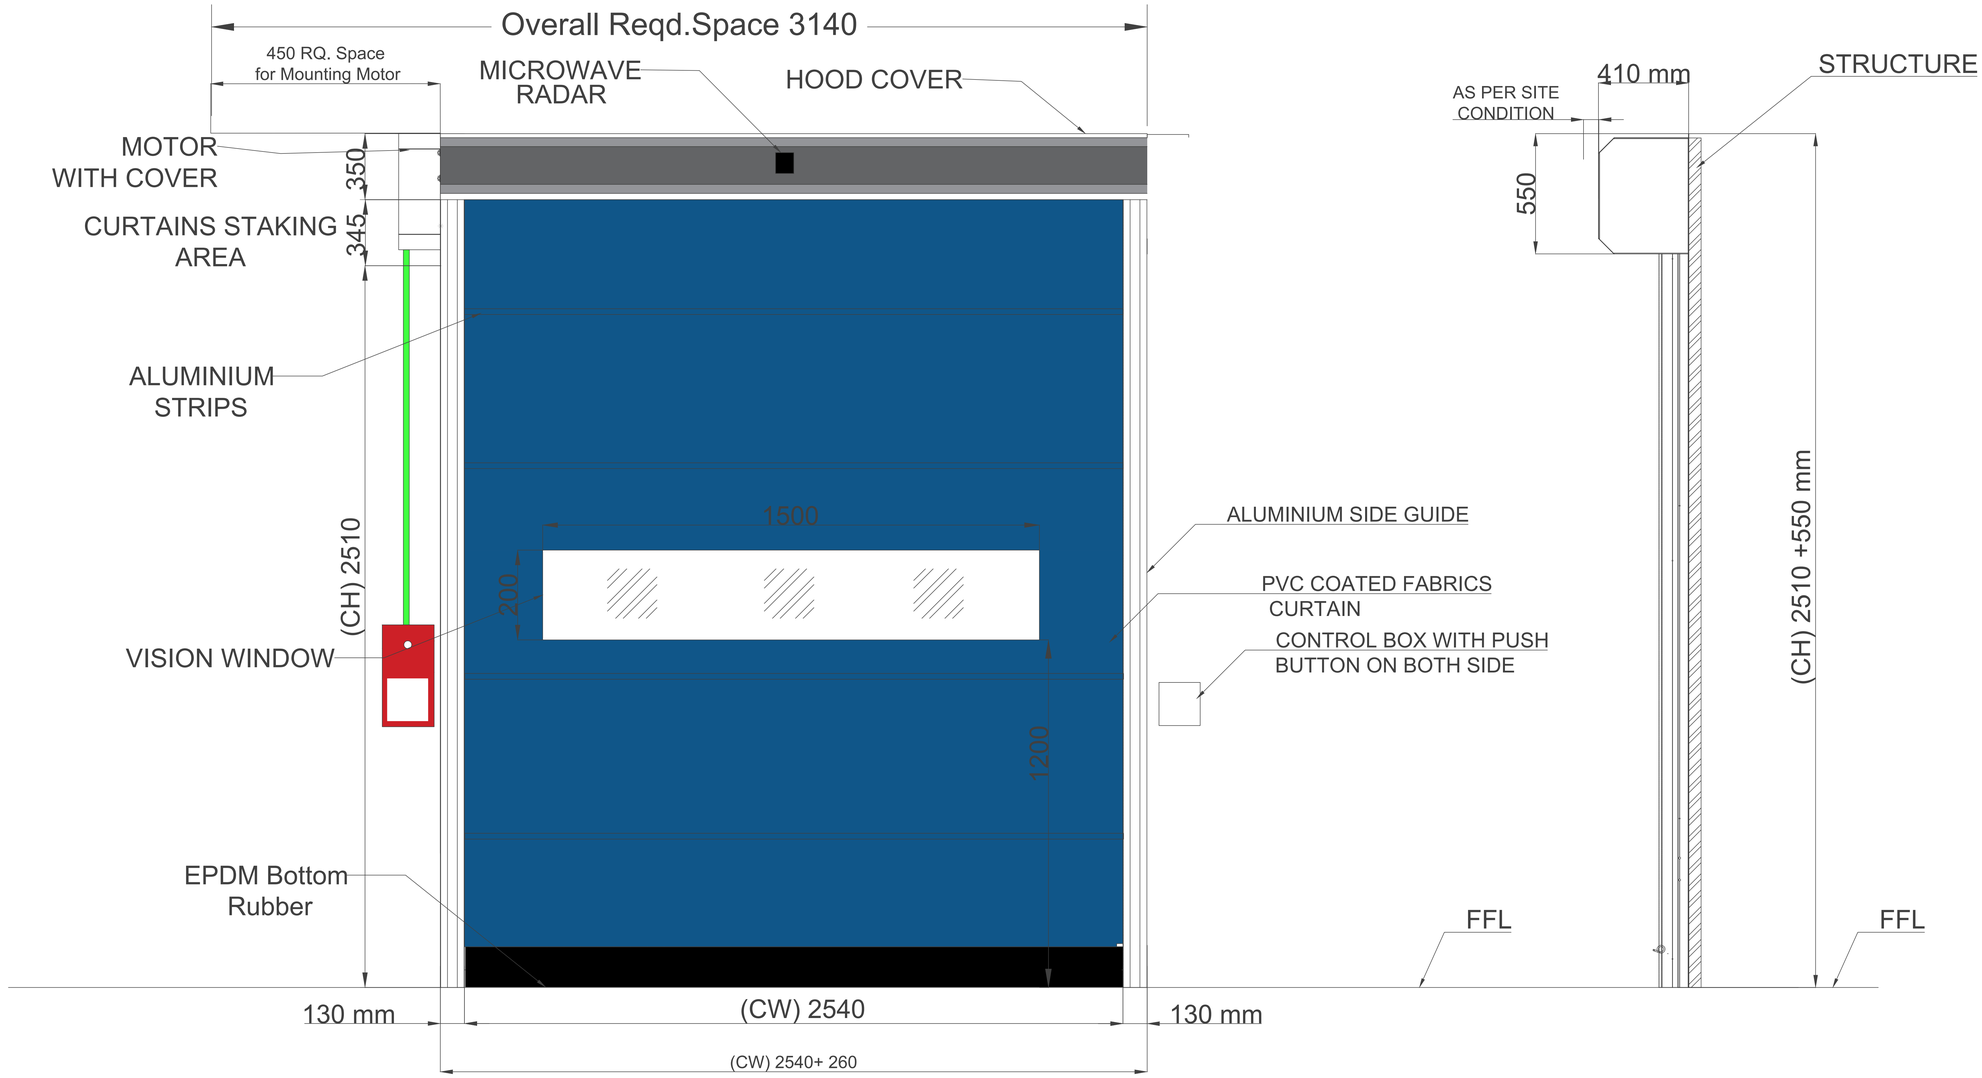


TECHNICAL SPECIFICATION :

SR.	SPECIFICATIONS	DETAILS
	Use	Internal Door
	Mounting	On Structure: Inside / outside
	Control Panel	As per STD
2	Motor	Nihva make
3	Manual Release	Hand Crank
4	Door Travel Speed	Opening: 1 m/Sec & Closing: 0.8m/Sec
5	Safety Device	Safety Photocell Pair & Safety Edges
6	Accessories	Microwave radar on both side ,interlocking system for two doors Flashing Light,Motor & Hood cover,push button

Note:-
1. All Dimensions are in mm
2.This drawing is solely meant to be understood.
3. RAL code confirm by client

Sr	Clear Width (CW)	Clear Height (CH)	QTY
1	**2540**	**2510**	01

Location area :- SEZ 1 C -Groung floor- entry

This drawing & design is the property of NIHVA TECHNOLOGIES. Not to be sold or copied to any other concern.

TITLE: HIGH SPEED DOOR

NIHVA TECHNOLOGIES PVT. LTD. PUNE
Tel : 020 66304033
Email:- info@nihva.com
Website:- www.nihva.com

	NAME	SIGN	DATE
DRAWN	B.S		10.03.2024
CHECK	V.T		10.03.2024
APPRD.	V.T		10.03.2024

CLIENT - TATA MOTORS
PROJECT - HIGH SPEED DOOR
FORMAT NO - NIHVA-DD-F-03
If any queries contact : projectsupport@nihva.com
DWG. NO. : NIHVA/24-25/SM/241001
REV- R00
ALL DIMENSION ARE IN mm
SCALE: NTS
WT:
SHEET: