
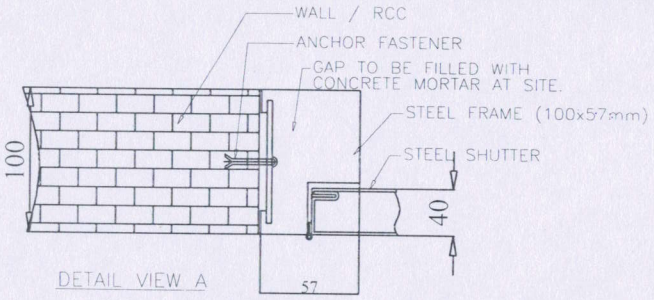


NOTES:-
ALL DIMENSIONS ARE IN MM.

NOTES:-
ALL DIMENSIONS ARE IN MM.

A. ABBREVIATION
Wall Opening Width : WOW
Wall Opening Height : WOH
Frame Opening Height : FOH
Frame Opening Width : FOW
Shutter Opening Height : SOH
Shutter Opening Width : SOW

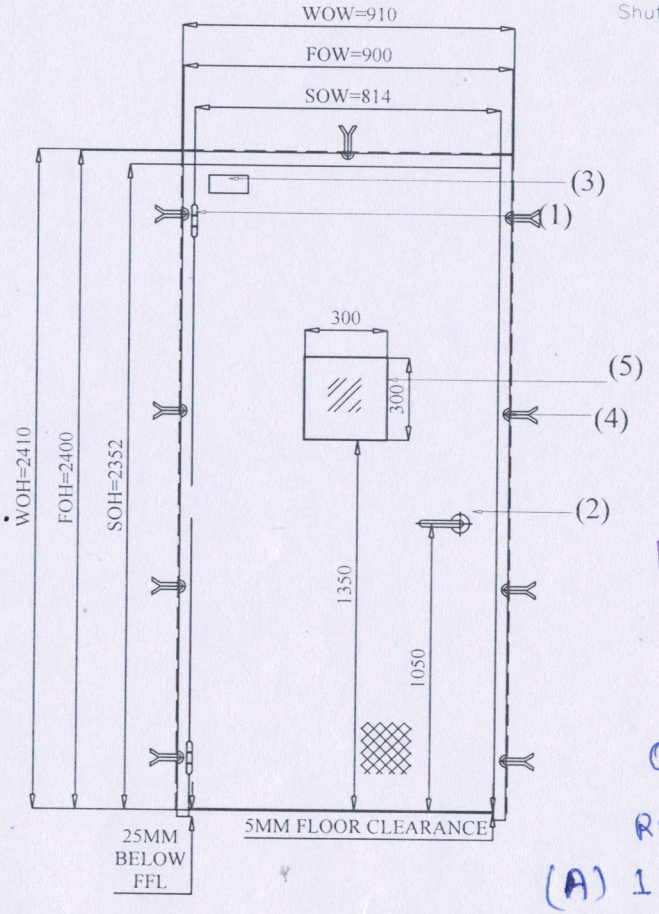

MATERIAL OF CONSTRUCTION

FRAME : G.I. 1.20mm Sheet
SHUTTER : G.I. 0.80mm Sheet
THICKNESS : 40MM
FRAME PROFILE : 100 x 57Mm (Single Ribet)

INFILL MATERIAL : MINERAL WOOL
DENSITY 48kg/cm3

PAINT: AS PER AS APPROVED RAL SHADE
POWDER COATED (DFT 80 Microns min)

SCHEDULE OF HARDWARE

1) S.S. Ball Bearing Hinges (GEZE MAKE) - 3 NOS .
2) Mortise Lock with Handle
3) Heavy Duty Door Closer GEZE MAKE -1 Nos
4) Anchor Fastener - 8 x 80MM.
5) Vision Panel with Non Fire Rated Glass of size 300 x 300MM (6mm thick Clear Float Glass)

3/4/19
NIHVA TECHNOLOGIES PVT. LTD.

Qty = 2 NOS
RAL 9002
(A) 1LH & 1RH (C)
Inside opening

DATE	REV.	STATUS	PARTICULARS	BY	CHKD.	APPD.

REVISIONS.


STATUS CODE: 1:PRELIMINERY COPY 2:FOR REVIEW 3:FOR MATERIAL PROCUREMENT
4:FOR APPROVAL 5:APPROVED FOR CONSTRUCTION

THIS DESIGNED OR DRAWING IS THE PROPERTY OF RADIANT SAFEDOORS PVT. LTD. IT IS SUBJECT TO THEIR RECALL, AND MUST NOT BE LENT,COPIED OR REPRODUCED WITHOUT THEIR WRITTEN PERMISSION.

APPROVED FOR CONSTRUCTION BY :-

	SIGN	DATE
DRAWN. BY		02/04/2019
CHKD. BY		02/04/2019
APPD. BY		02/04/2019

CLIENT : M/S. Nihva Technologies Pvt Ltd
SITE :
QTY. 2 Nos
TITLE: SINGLE LEAF GENERAL STEEL DOOR WITH Lock
DOOR SIZE: 900MM (W) x 2400MM (H) -- S.L.
PROJECTION
SCALE N.T.S.
RADIANT SAFEDOORS PVT. LTD.
WORKS : 539, PHASE I, VATVA GIDC, AHMEDABAD.
DRG. NO. RSPL/190402/04

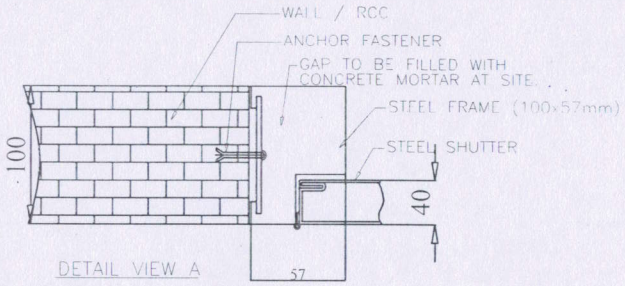

DETAIL VIEW A

NOTES:-


ALL DIMENSIONS ARE IN MM.

NOTES:-

ALL DIMENSIONS ARE IN MM.

A. ABBREVIATION

Wall Opening Width : WOW
Wall Opening Height : WOH
Frame Opening Height : FOH
Frame Opening Width : FOW
Shutter Opening Height : SOH
Shutter Opening Width : SOW

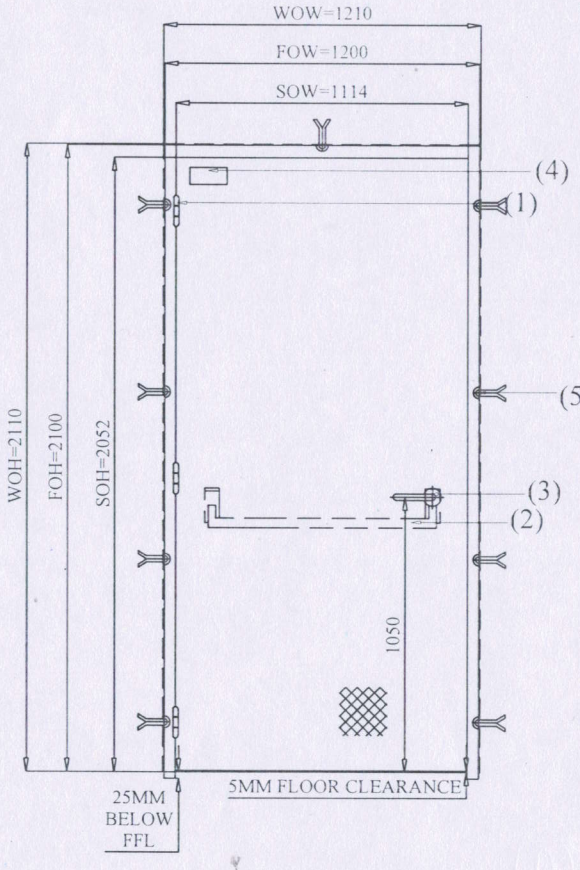

3/4/19

NIHVA TECHNOLOGIES PVT. LTD.

Qty = 1 NO

RAL - 3020

LH - Outside (O) opening

MATERIAL OF CONSTRUCTION

FRAME : G.I. 1.20mm Sheet
SHUTTER : G.I. 0.80mm Sheet
THICKNESS : 40MM
FRAME PROFILE : 100 x 57Mm (Single Ribet)

INFILL MATERIAL : MINERAL WOOL
DENSITY 48kg/cm3

PAINT: AS PER AS APPROVED RAL SHADE POWDER COATED (DFT 80 Microns min)

SCHEDULE OF HARDWARE

1) S.S. Ball Bearing Hinges (GEZE MAKE) - 3 NOS .
2) Panic Bar for Single Leaf Door - YALE MAKE - 1 Nos.
3) External Trim Bar (Panic Latch) - Yale Make -1 Nos.
4) Heavy Duty Door Closer GEZE MAKE -1 Nos
5) Anchor Fastener - 8 x 80MM.

DATE	REV.	STATUS	PARTICULARS	BY	CHKD.	APPD.
			REVISIONS.			

STATUS CODE: 1:PRELIMINERY COPY 2:FOR REVIEW 3:FOR MATERIAL PROCUREMENT 4:FOR APPROVAL 5:APPROVED FOR CONSTRUCTION

THIS DESIGNED OR DRAWING IS THE PROPERTY OF RADIANT SAFEDOORS PVT. LTD. IT IS SUBJECT TO THEIR RECALL, AND MUST NOT BE LENT,COPIED OR REPRODUCED WITHOUT THEIR WRITTEN PERMISSION.

APPROVED FOR CONSTRUCTION BY:-


	SIGN	DATE
DRAWN BY		04/01/2019
CHKD. BY		04/01/2019
APPD. BY		04/01/2019

CLIENT : M/S. Nihva Technologies Pvt Ltd
SITE :
QTY. 28 Nos
TITLE: SINGLE LEAF GENERAL STEEL DOOR WITH PANIC BAR

PROJECTION: SCALE: N.T.S.

RADIANT SAFEDOORS PVT. LTD.
WORKS : 539, PHASE II, VATVA GIDC, AHMEDABAD.


ORG. NO. RSPL/190402/01

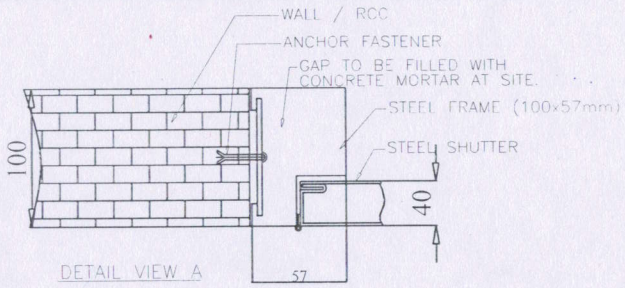

NOTES:-
ALL DIMENSIONS ARE IN MM.

NOTES:-
ALL DIMENSIONS ARE IN MM.

A. ABBREVIATION
Wall Opening Width : WOW
Wall Opening Height : WOH
Frame Opening Height : FOH
Frame Opening Width : FOW
Shutter Opening Height : SOH
Shutter Opening Width : SOW

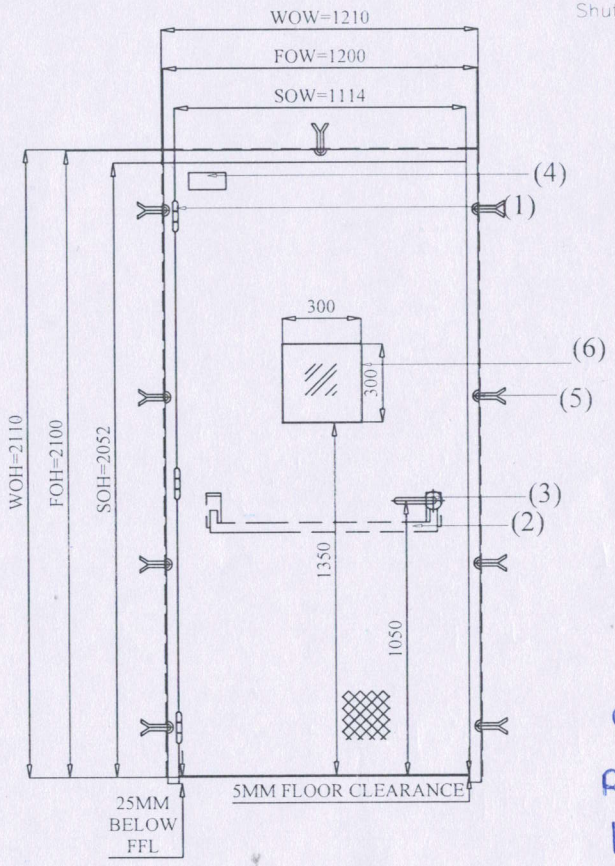

MATERIAL OF CONSTRUCTION

FRAME : G.I. 1.20mm Sheet
SHUTTER : G.I. 0.80mm Sheet
THICKNESS : 40MM
FRAME PROFILE : 100 x 57Mm (Single Ribet)

INFILL MATERIAL : MINERAL WOOL
DENSITY 48kg/cm3

PAINT: AS PER AS APPROVED RAL SHADE
POWDER COATED (DFT 80 Microns min)

SCHEDULE OF HARDWARE

1) S.S. Ball Bearing Hinges (GEZE MAKE) - 3 NOS .
2) Panic Bar for Single Leaf Door - YALE MAKE - 1 Nos.
3) External Trim Bar (Panic Latch) - Yale Make -1 Nos.
4) Heavy Duty Door Closer GEZE MAKE -1 Nos
5) Anchor Fastener - 8 x 80MM.
6) Vision Panel with Non Fire Rated Glass of size 300 x 300MM (6mm thick Clear Float Glass)

3/4/19

NIHVA TECHNOLOGIES Pvt. LTD.

Qty = 1 NO
RAL - 9002
LH - Outside (O) opening

DATE	REV.	STATUS	PARTICULARS	BY	CHKD.	APPD.


REVISIONS.

STATUS CODE: 1:PRELIMINERY COPY 2:FOR REVIEW 3:FOR MATERIAL PROCUREMENT 4:FOR APPROVAL 5:APPROVED FOR CONSTRUCTION

THIS DESIGNED OR DRAWING IS THE PROPERTY OF RADIANT SAFEDOORS PVT. LTD. IT IS SUBJECT TO THEIR RECALL AND MUST NOT BE LENT,COPIED OR REPRODUCED WITHOUT THEIR WRITTEN PERMISSION.

APPROVED FOR CONSTRUCTION BY:-


	SIGN.	DATE	CLIENT SITE	QTY.
DRAWN. BY		02/04/2019	M/S. Nihva Technologies Pvt Ltd	5 Nos
CHKD. BY		02/04/2019	TITLE: SINGLE LEAF GENERAL STEEL DOOR WITH PANIC BAR	
APPD. BY		02/04/2019	DOOR SIZE: 1200MM (W) x 2100MM (H) - S.L.	
PROJECTION		SCALE N.T.S.	RADIANT SAFEDOORS PVT. LTD. WORKS : 539, PHASE II, VATVA GIDC, AHMEDABAD.	DRG. NO. RSPL/190402/02

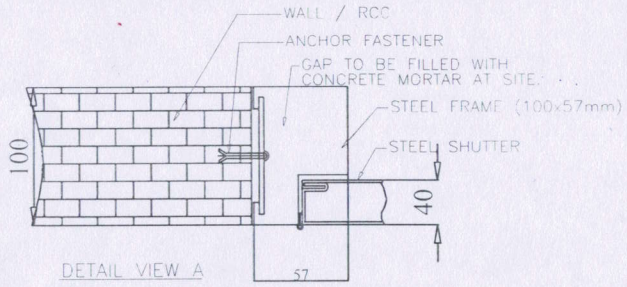

NOTES:-
ALL DIMENSIONS ARE IN MM.

NOTES:-
ALL DIMENSIONS ARE IN MM.

A. ABBREVIATION
Wall Opening Width : WOW
Wall Opening Height : WOH
Frame Opening Height : FOH
Frame Opening Width : FOW
Shutter Opening Height : SOH
Shutter Opening Width : SOW

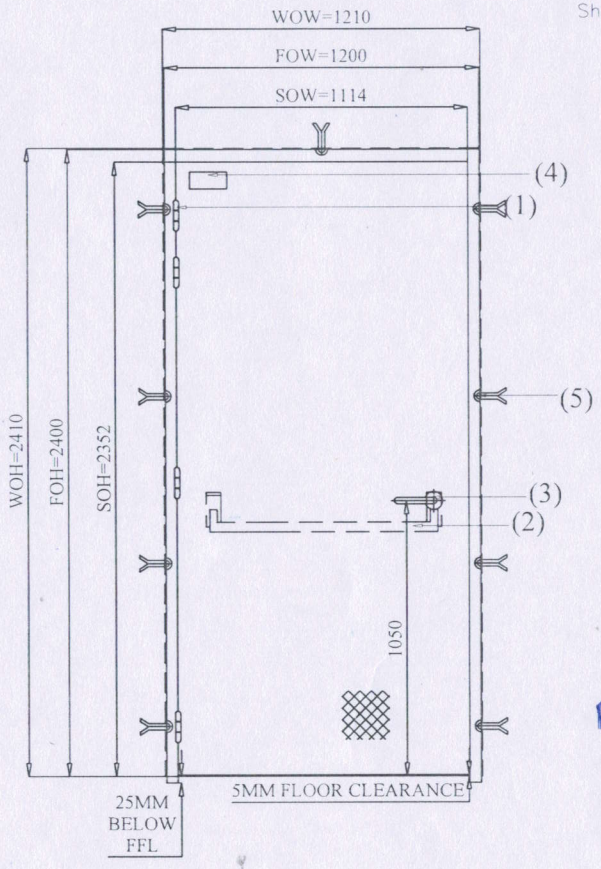

MATERIAL OF CONSTRUCTION

FRAME : G.I. 1.20mm Sheet
SHUTTER : G.I. 0.80mm Sheet
THICKNESS : 40MM
FRAME PROFILE : 100 x 57Mm (Single Ribet)

INFILL MATERIAL : MINERAL WOOL
DENSITY 48kg/cm3

PAINT: AS PER AS APPROVED RAL SHADE
POWDER COATED (DFT 80 Microns min)

SCHEDULE OF HARDWARE

1) S.S. Ball Bearing Hinges (GEZE MAKE) - 4 NOS .
2) Panic Bar for Single Leaf Door - YALE MAKE - 1 Nos.
3) External Trim Bar (Panic Latch) - Yale Make -1 Nos.
4) Heavy Duty Door Closer GEZE MAKE -1 Nos
5) Anchor Fastener - 8 x 80MM.

S 3/4/19

NIHVA TECHNOLOGIES PVT. LTD.

Qty = 1 NO

RAL- 3020

LH- Outside (D) Opening.

DATE	REV.	STATUS	PARTICULARS	BY	CHKD	APPD.
			REVISIONS.			

STATUS CODE: 1:PRELIMINERY COPY 2:FOR REVIEW 3:FOR MATERIAL PROCUREMENT
4:FOR APPROVAL 5:APPROVED FOR CONSTRUCTION

THIS DESIGNED OR DRAWING IS THE PROPERTY OF RADIANT SAFEDOORS PVT. LTD. IT IS SUBJECT TO THEIR RECALL, AND MUST NOT BE LENT,COPIED OR REPRODUCED WITHOUT THEIR WRITTEN PERMISSION.

APPROVED FOR CONSTRUCTION BY:-

	SIGN	DATE	CLIENT M/S. Nihva Technologies Pvt. Ltd	QTY.
DRAWN BY		02/04/2019	SITE	1Nos
CHKD. BY		02/04/2019	TITLE: SINGLE LEAF GENERAL STEEL DOOR WITH PANIC BAR	
APPD. BY		02/04/2019	DOOR SIZE: 1200MM (W) x 2400MM (H) - S.L.	
PROJECTION		SCALE N.T.S.	RADIANT SAFEDOORS PVT. LTD. WORKS : 539, PHASE II, VATVA GIDC., AHMEDABAD.	DRG. NO. RSPL/190402/03