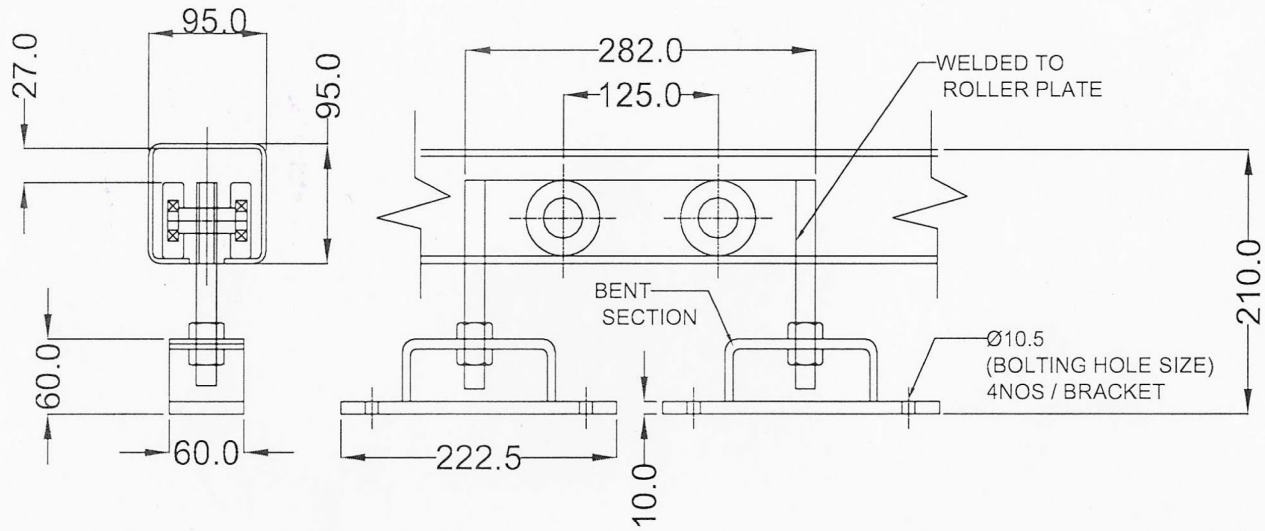
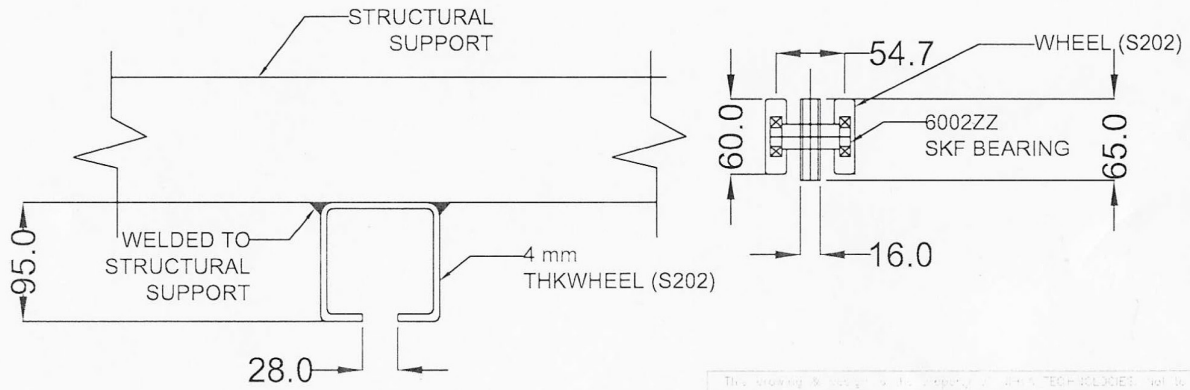



Approved
02-05-2022

NOTE:
END STOPPERS AT BOTH SIDES FOR EACH
TRACK SHOULD BE PROVIDED WITH TRACK

This drawing & design is the property of NIHVA TECHNOLOGIES. Not to be used, copied or any other purpose.

| | | | |
|---|---|---|---|
| TITLE : TOP TRACK AND BRACKET ASM | | | NIHVA TECHNOLOGIES PVT. LTD. PUNE<br>Tel : 020 66304033<br>Email:- info@nihva.com<br>Website:- www.nihva.com |
| | NAME | SIGN | DATE |
| DRAWN | M.SUTAR | | 02.05.2022 |
| CHECK | M.SUTAR | | 02.05.2022 |
| APPRD. | | | |
| CLIENT - NIHVA TECHNOLOGIES PVT LTD | | | |
| PROJECT - DOOR | | | |
| SITE LOCATION - PUNE | | | |
| If any queries contact : design@nihva.com | DWG. NO. :NIHVA/22-23/VDR/014 | | REV- 0 |
| ALL DIMENSION ARE IN mm | SCALE: NTS | WT: | SHEET: 01 OF 01 |