


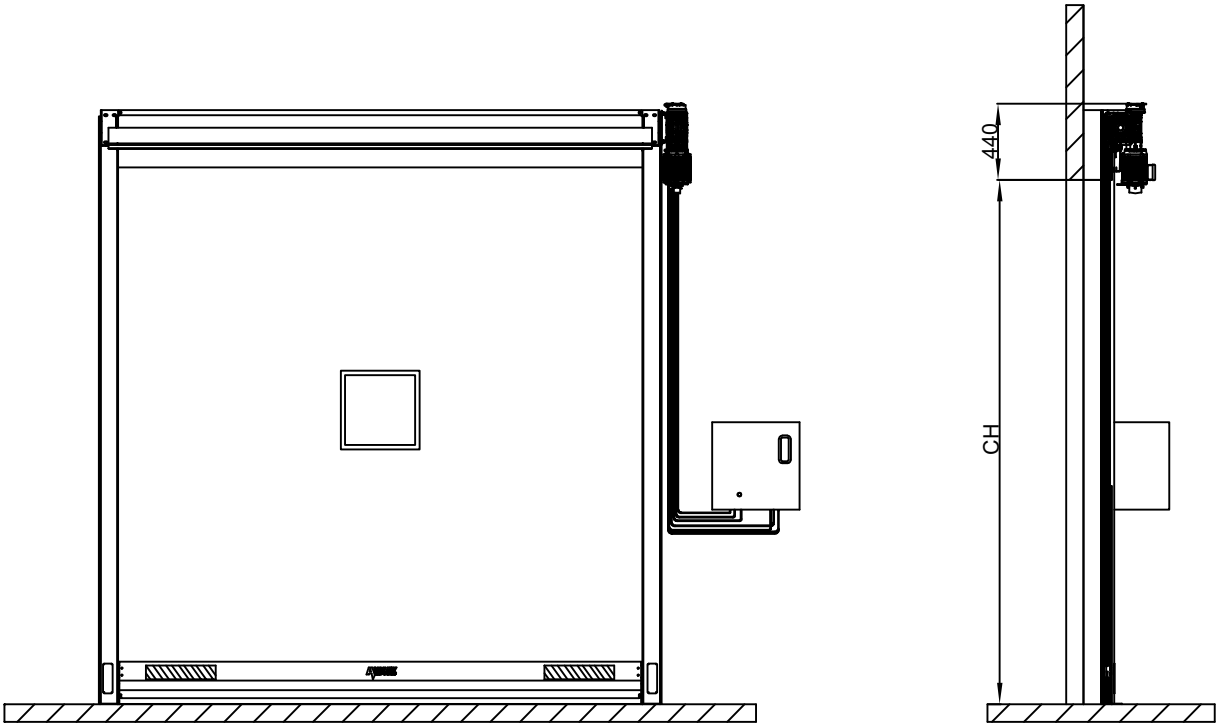


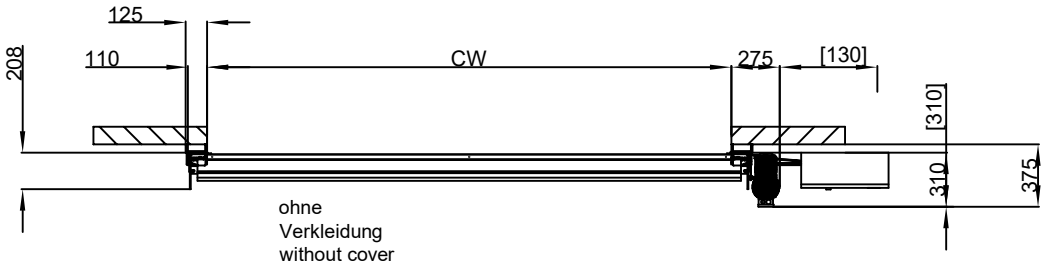

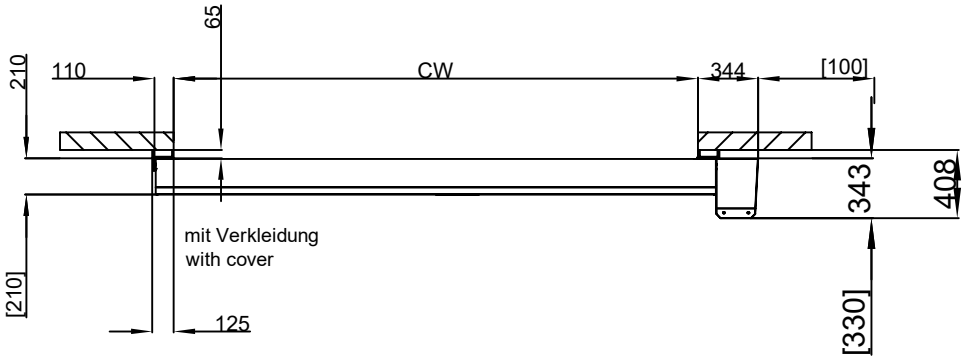

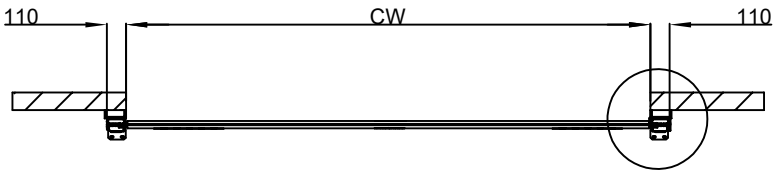

Note:-

1.All dimension are in MM

2.All civil work is in client scope

3.Given GA drawing is only for the client unerstanding purpose

4.If strucuture required, will be in client scope(ISMC 125X65)

CLEAR WIDTH	CLEAR HEIGHT
2750 mm	2750mm

This drawing & design is the property of NIHVA TECHNOLOGIES. Not to be sold or copied to any other concern.

TITLE:-MACHINE PROTECTION DOOR(RP300)

NIHVA TECHNOLOGIES PVT. LTD.

NIHVA TECHNOLOGIES PVT. LTD. PUNE
Tel : 020 66304033
Email:- info@nihva.com
Website:- www.nihva.com

	NAME	DATE	SIGN
DRAWN	SUJATA	11/02/2022	
CHECK	G. P	11/02/2022	
APPRD.	A.K	11/02/2022	

CLIENT - Jindal Stainless Limited.

LOCATION - Gurugram

PRODUCT - Machine Protection Door

If any queries contact : design@nihva.com

DWG NO:-NIHVA/21-22/CLT/0343 REV- 0

ALL DIMENSION ARE IN mm

SCALE: NTS SCALE:-- 1:1 SHEET: 01 OF 01

Rev No.	Revision	Date	Revised By