
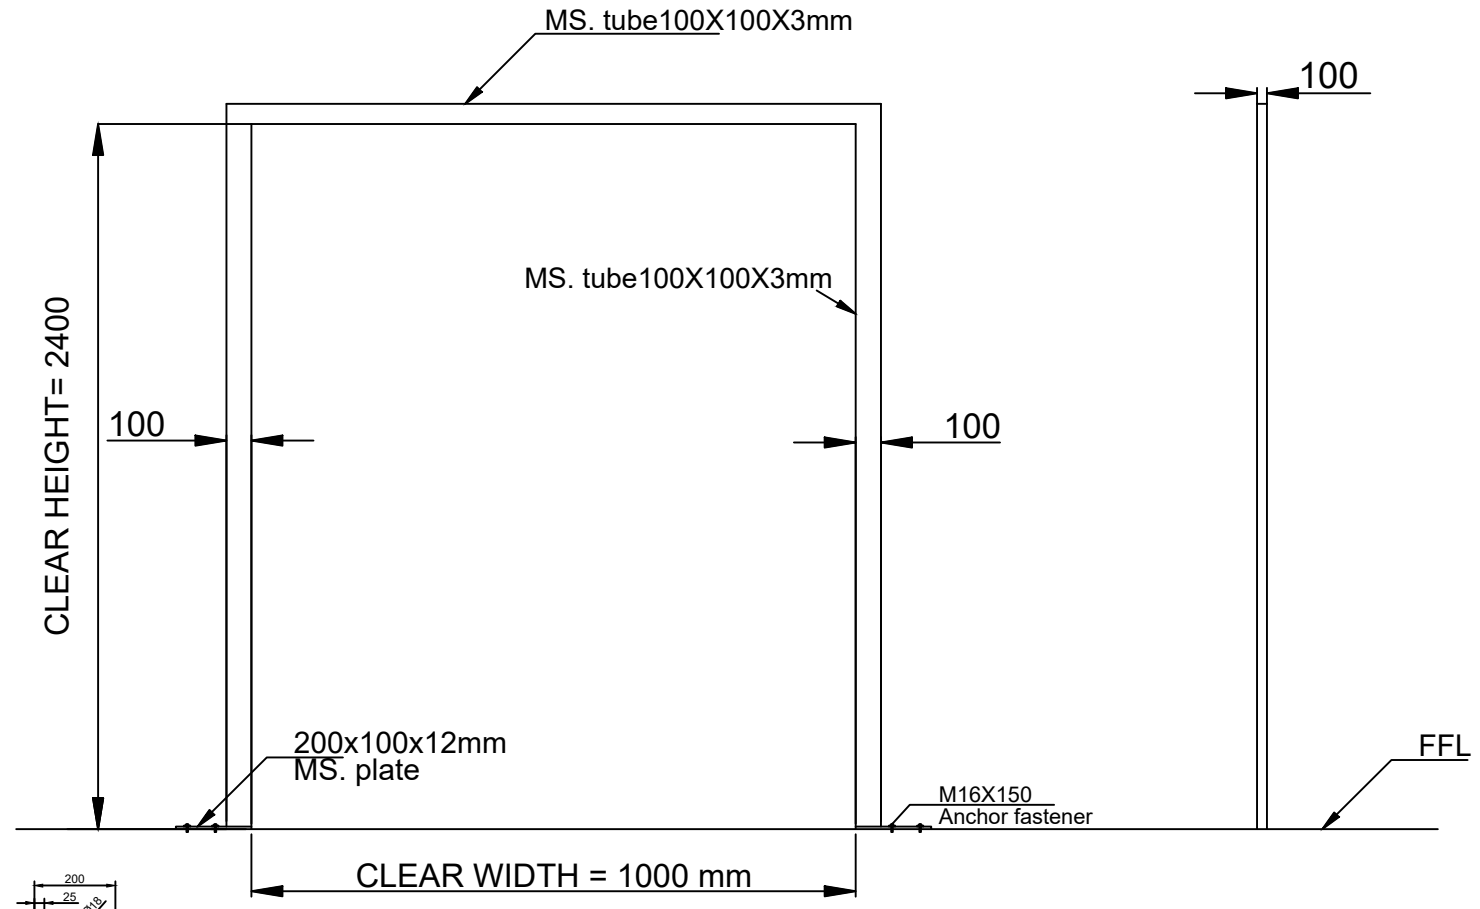


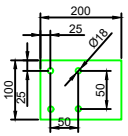

MS. plate

NOTE -
(1) ALL REQUIRED TECHNICAL MS STRUCTURE & FITTING IN CLIENT SCOPE .
(2) ALL CIVIL WORK IN CLIENT SCOPE .

This drawing & design is the property of NIHVA TECHNOLOGIES. Not to be sold or copied to any other concern.

TITLE	FIRE DOOR STRUCTURE			NIHVA TECHNOLOGIES PVT. LTD. PUNE
	NAME	SIGN	DATE	
DRAWN	S.J		23.07.2024	CLIENT - Ferrero India Pvt Ltd
CHECK	B.B		23.07.2024	PROJECT -..
APPRD.	A.K		23.07.2024	LOCATION - PUNE

NIHVA TECHNOLOGIES PVT. LTD.
Tel : 020 66304033
Email:- info@nihva.com
Website:- www.nihva.com

If any queries contact : design1@nihva.com	DWG. NO. : NIHVA/24-25/xxx	REV- 0
ALL DIMENSION ARE IN mm	SCALE: NTS WT:	SHEET: 01 OF 01