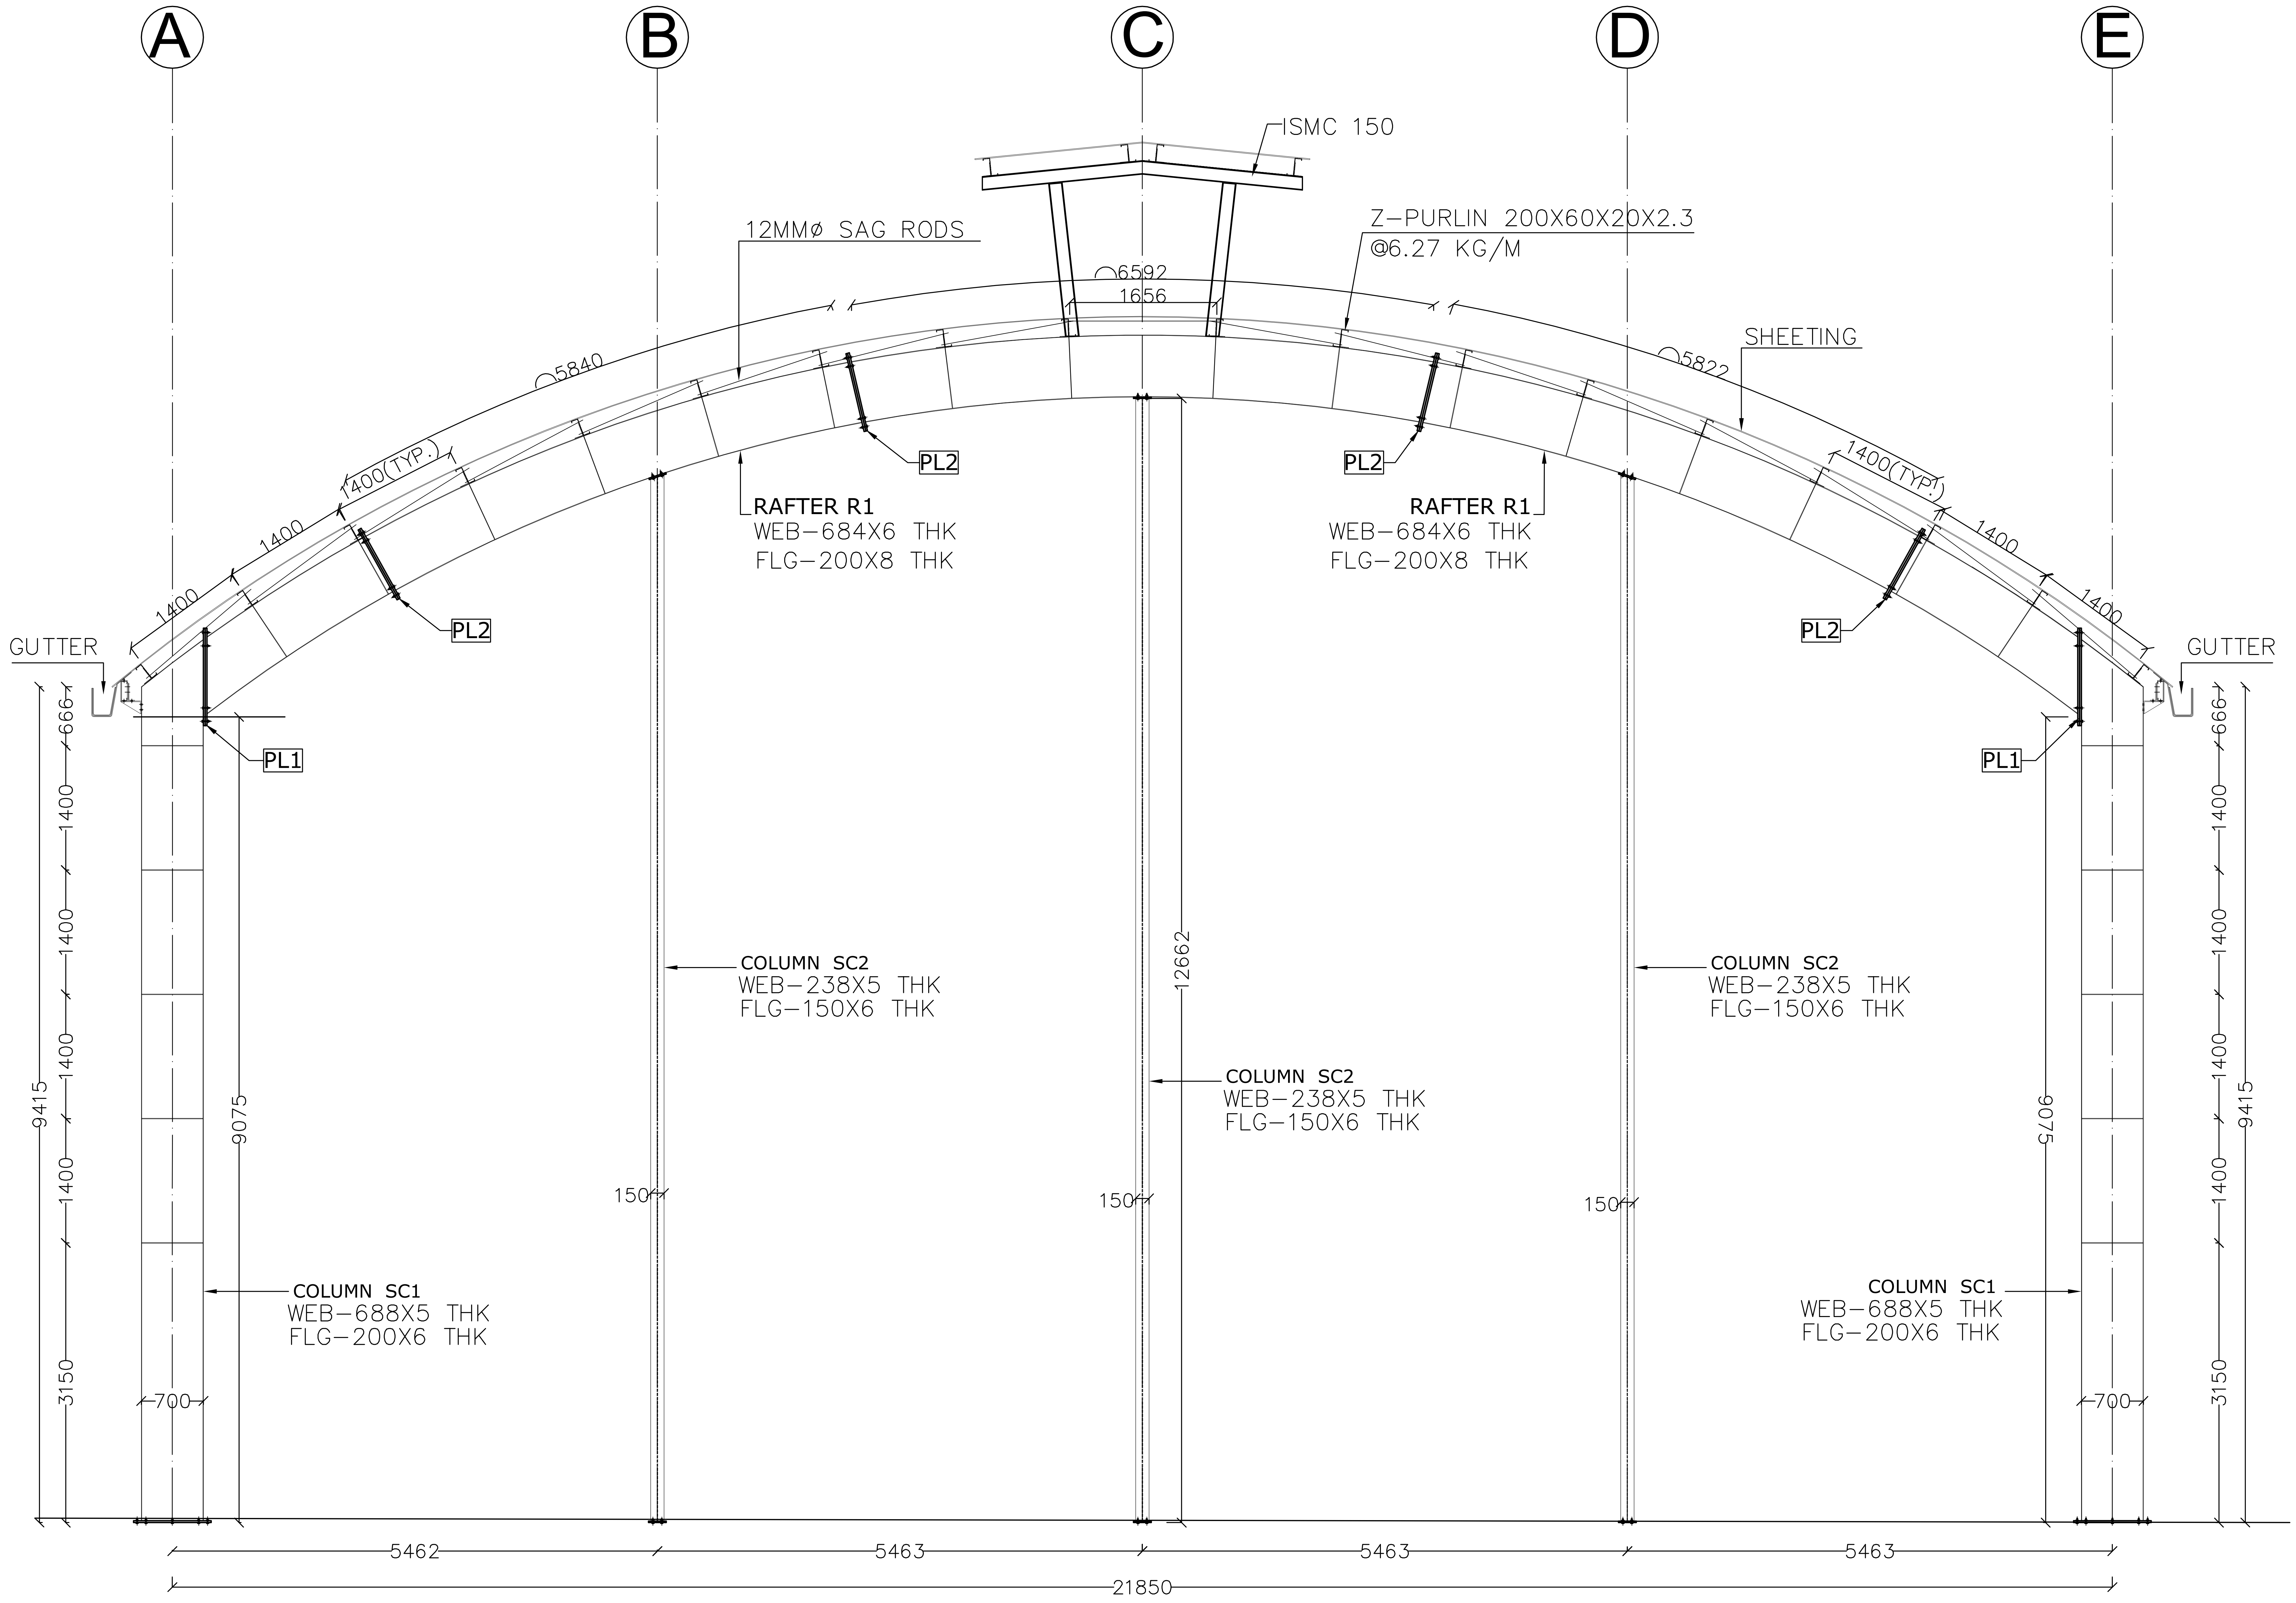
A
B
C
D
E
ISMC 150
12MMø SAG RODS
Z–PURLIN 200X60X20X2.3
@6.27 KG/M
6592
1656
5840
5822
SHEETING
1400(TYP.)
1400
1400
1400(TYP.)
1400
1400
GUTTER
GUTTER
PL1
PL1
PL2
PL2
PL2
PL2
RAFTER R1
WEB–684X6 THK
FLG–200X8 THK
RAFTER R1
WEB–684X6 THK
FLG–200X8 THK
COLUMN SC2
WEB–238X5 THK
FLG–150X6 THK
COLUMN SC2
WEB–238X5 THK
FLG–150X6 THK
COLUMN SC2
WEB–238X5 THK
FLG–150X6 THK
COLUMN SC1
WEB–688X5 THK
FLG–200X6 THK
COLUMN SC1
WEB–688X5 THK
FLG–200X6 THK
12662
9415
9075
666
1400
1400
1400
1400
3150
700
150
150
150
9075
9415
666
1400
1400
1400
1400
3150
700
5462
5463
5463
5463
21850

PORTAL FRAME ELEVATION
GRID LINE -01 & 02

KEY PLAN :-

LEGEND :-
▨ REINFORCED CONCRETE
▨ 230MM THK BRICK WALL
■ STRUCTURAL GLAZING

N

GENERAL NOTES :

ALL DIMENSIONS ARE IN MILLIMETRES AND ARE UNFINISHED DIMENSIONS UNLESS OTHERWISE SPECIFIED.

ALL LEVELS ARE IN METRES AND ARE UNFINISHED LEVELS UNLESS OTHERWISE SPECIFIED.

DO NOT SCALE DRAWINGS. ONLY WRITTEN DIMENSIONS SHALL BE FOLLOWED, ANY DISCREPANCIES NOTED SHALL BE BROUGHT TO THE NOTICE OF THE ARCHITECT PRIOR TO EXECUTION.

SCHEDULE OF JOINERY

TYPE	DESCRIPTION	SIZE	NO.
RS	HANGER DOOR	24000 x 9000	01
W	WINDOW	1500 x 1200	20
D	DOOR	1200 x 2200	0

STRUCTURAL NOTES :

- ANCHOR BOLTS OF GRADE 4.6
- CONCRETE GRADE M30
- REBAR GRADE Fe 415

REV.	DESCRIPTION	DATE	BY	CHD.
R1	ISSUED FOR APPROVAL	20-07-17	CMF	SSF
R0	ISSUED FOR APPROVAL	20-07-17	CMF	SSF

AMENDMENT

GRAPHIC SCALE:
0 0.5M 2M 4M
0.5M 0 1M 3M 5M

ARCHITECT

CLIENT:
HANGER
AT PUNE

PROJECT LOCATION:
PUNE

DRAWING TITLE:
GENERAL ARRANGEMENT DRAWINGS

SCALE :	NTS	DRAWN :	SRK	R0
DATE :	02-08-2018	CHKD :	SRK	
PROJECT ID:				DRAWING NO:
1718-AI-052-PEB				PD: 01

Astre Infra
Private Limited
imagine and its done
691, Bemciel Indl. Estate,
Khanapur Rd,
Udyambag, Belgaum- 590008.
www.astreinfra.com

THESE DRAWINGS ARE UNDER COPYRIGHT AND ARE THE PROPERTY OF ASTRE INFRA PVT. LTD.. NONE OF THE DRAWINGS AND RELATED DOCUMENTS CAN BE REPRODUCED, COPIED IN WHOLE OR IN PART WITHOUT PRIOR EXPRESSED WRITTEN CONSENT OF ASTRE INFRA PVT.LTD. THESE DRAWINGS CANNOT BE HANDED OVER TO A THIRD PARTY OR USED FOR ANY PURPOSE, OTHER THAN THAT FOR WHICH IT HAS BEEN LOANED. AFTER FULFILLING THE PURPOSE OF ISSUE THE DRAWINGS SHALL BE RETURNED TO ASTRE INFRA PVT.LTD.