

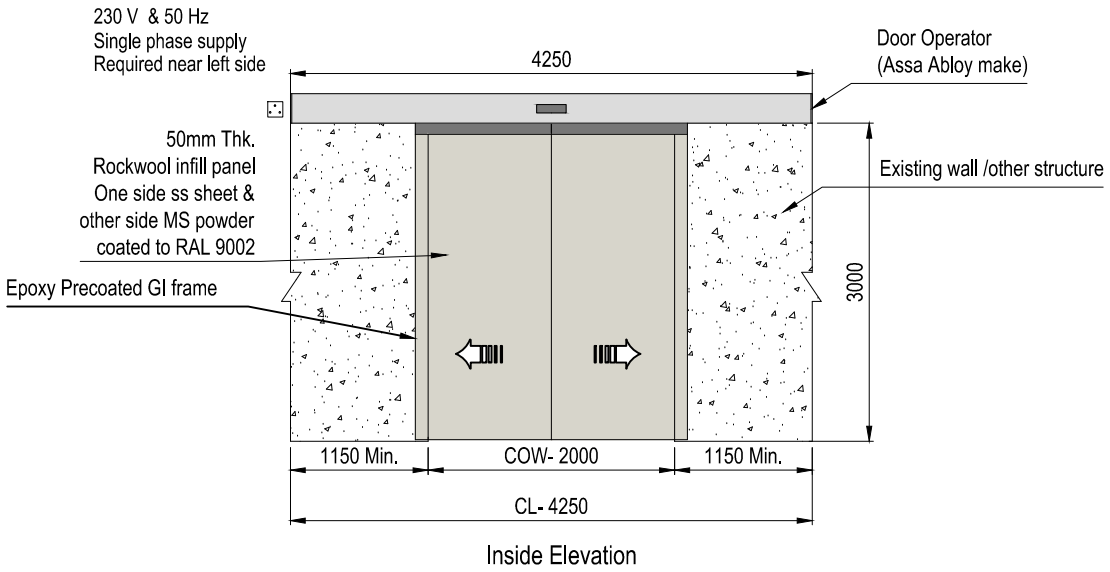


Inside Elevation

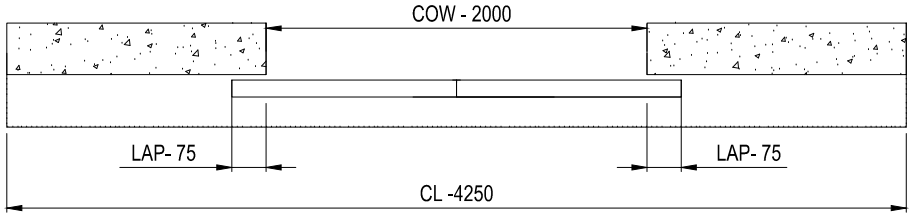


Closed Condition

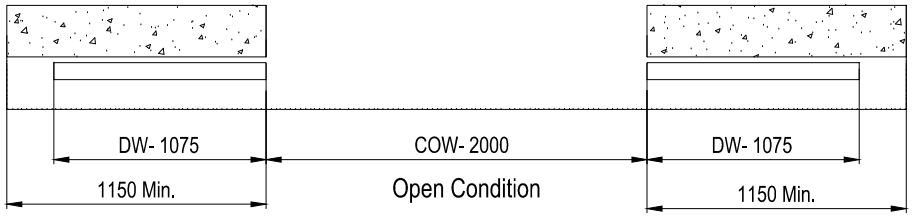

Open Condition

Plan

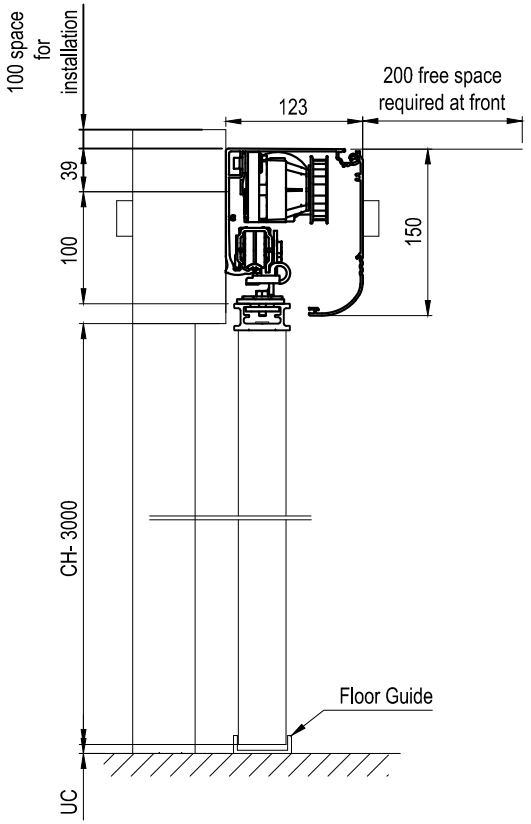

Door Size			
Sr. No.	Clear Width	Clear Height	Quantity
1	2000	3000	1

REV 1(31-03-2018)- Panel thickness revised from 60mm to 50mm.
Also panel will be of SS on one side & MS powder coated on other side.

This drawing & designing is the property of NIHVA TECHNOLOGIES. Not to be sold or copied to any other concern.

TITLE: G.A.OF AUTOMATIC SLIDING DOOR

	SIGN	DATE
DRAWN	OMKAR	10/03/18
CHECK	S.S.	10/03/18
REV.	00	
APPROVAL	S.S.	10/03/18

If any queries contact : design@nihva.com

ALL DIMENSION ARE IN mm

NIHVA TECHNOLOGIES PVT. LTD.
NIHVA TECHNOLOGIES PVT. LTD. PUNE
Tel : 020 66304033
Email:- info@nihva.com
Website:- www.nihva.com

CLIENT - MASTPRO
PROJECT - MARS INTERNATIONALS
SITE - PUNE
DWG. NO. : NIHVA/17-18/0397/R01 | REV-1
SCALE: NTS | WT: | SHEET: 01 OF 01