




SIDE VIEW

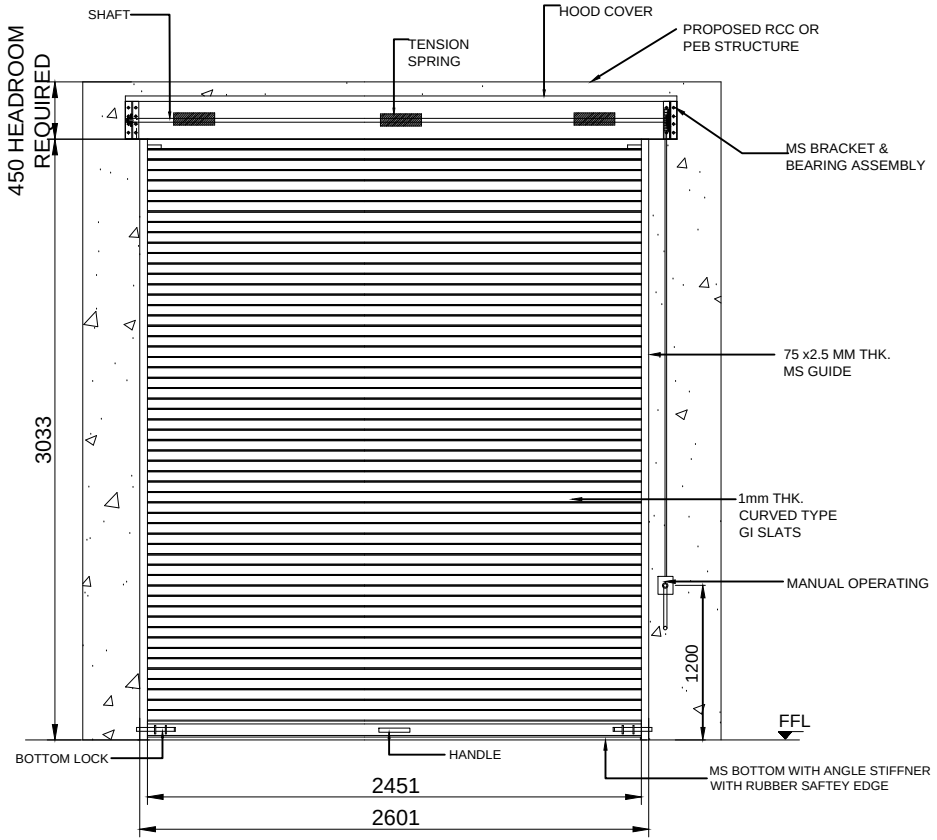


INSIDE ELEVATION

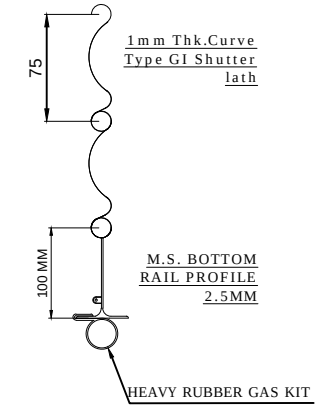

M.S. BOTTOM RAIL PROFILE 2.5MM

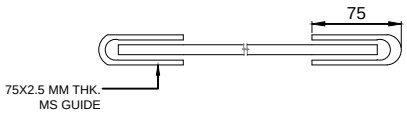

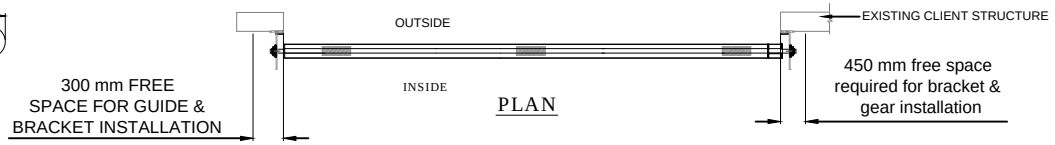

PLAN

S.N.	LOCATION	SIZE	QUANTITY
1	B100	2451(W)X3033(H)	36 Nos

TOLERANCE - ±10mm

NOTE-
1. ALL CIVIL WORK WILL BE CLIENT'S SCOPE.
2.STRUCTURE REQUIRED FOR SHUTTER IS IN CLIENT'S SCOPE.
3.FINAL FINISH OF SHUTTER WILL BE IN POWDER COATING OF APPROVED COLOR i.e.RAL 7001.

This drawing & design is the property of NIHVA TECHNOLOGIES. Not to be sold or copied to any other concern.

TITLE: GEAR OPERATED ROLLING SHUTTER 2.451mX3.033m Right side gear box.

NIHVA TECHNOLOGIES PVT. LTD.

NIHVA TECHNOLOGIES PVT. LTD. PUNE
Tel : 020 66304033
Email:- info@nihva.com
Website:- www.nihva.com

	NAME	SIGN	DATE
DRAWN	OMKAR		03.05.2018
CHECK	PRADEEP		03.05.2018
APPRD.	PRADEEP		03.05.2018

CLIENT - INDOSPACE
PROJECT - BUILDING B100
SITE LOCATION - CHAKAN 1

If any queries contact : design@nihva.com
DWG. NO. : NIHVA/18-19/0025 REV- 0
ALL DIMENSION ARE IN mm
SCALE: NTS WT: SHEET: 01 OF 01