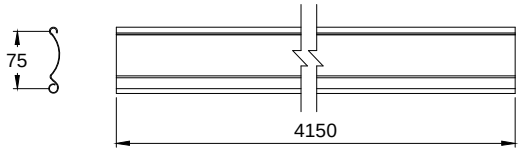

Curved slat

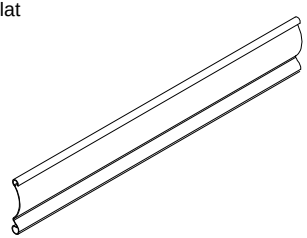

Slat profile- curved type.
Material- MS
Thickness - 1mm
Length of slats - 4150mm
Total no of slat - 240

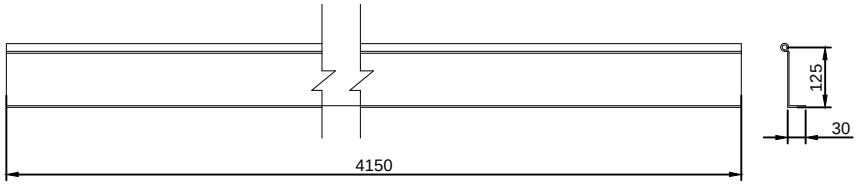

Curved slat

Material- MS
Thickness - 2.5mm
Length of bottom profile - 4150mm
Quantity- 3 Nos.

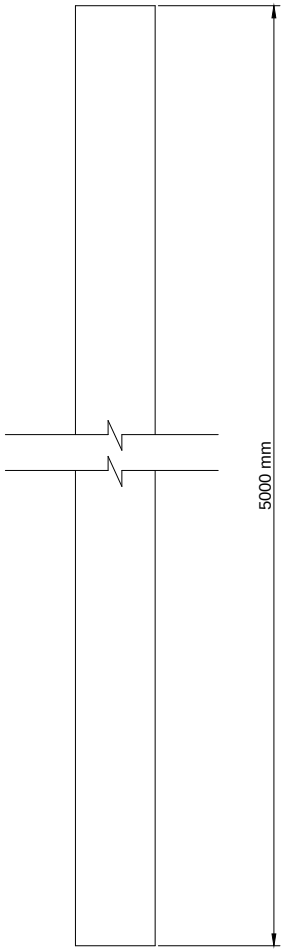

Material- MS
Thickness - 3mm
Length of guide - 5000mm
Quantity- 6 Nos.

DIMENSION :

CLEAR WIDTH	CLEAR HEIGHT	QUANTITY

MATERIAL : GI

THICKNESS : 0.9mm

NIHVA TECHNOLOGIES PVT. LTD.

NIHVA TECHNOLOGY PVT. LTD. PUNE
Email:- info@nihva.com
Website:- www.nihva.com

TITLE:

MS SLAT, GUIDE & BOTTOM PROFILE

CLIENT'S APPROVAL :

CLIENT -

PROJECT -

SITE LOCATION -

DWG. NO. : NIHVA/16-17/

SCALE: NTS	WT:	SHEET:1 OF 1
DRAWN BY: OMKAR		DATE: 21-11-2016
CHECK : SAGAR P.		DATE: 21-11-2016

If any queries contact : projects@nihva.com

NOTE: ALL DIMENSION ARE IN mm

THIS DRAWING & DESIGNING IS THE PROPERTY OF NIHVA TECHNOLOGIES. NOT BE SOLD OR COPY TO ANY OTHER CONCERN.