



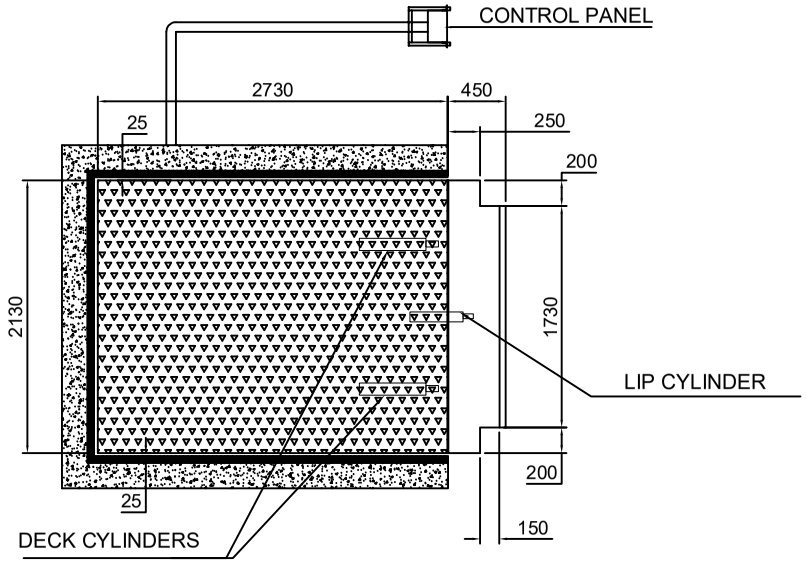


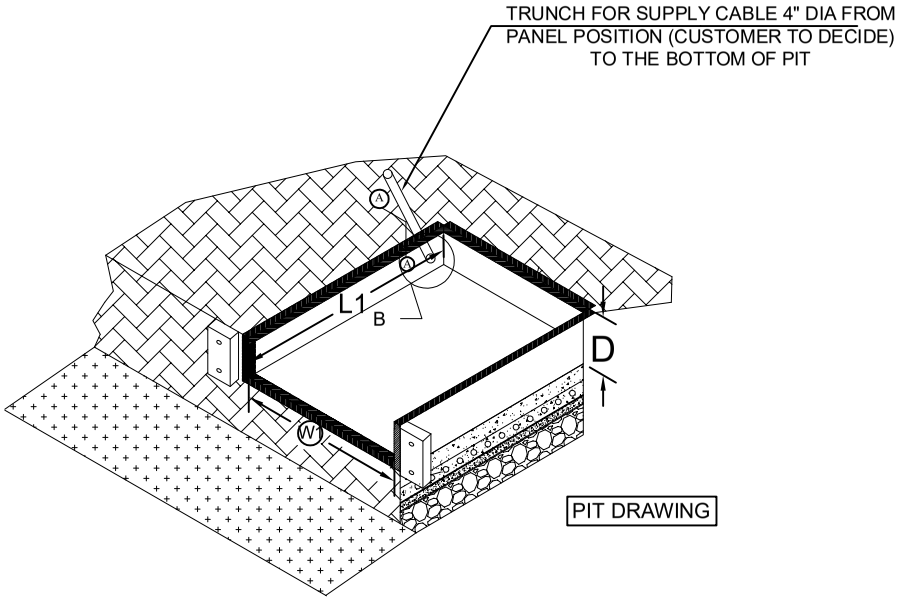

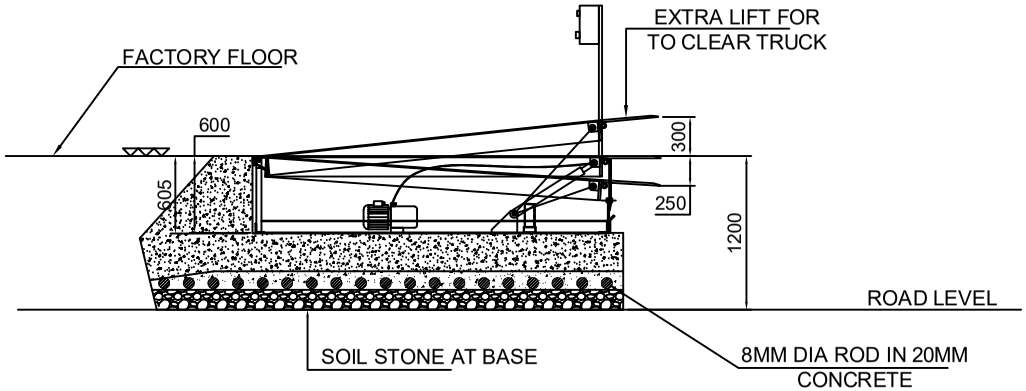

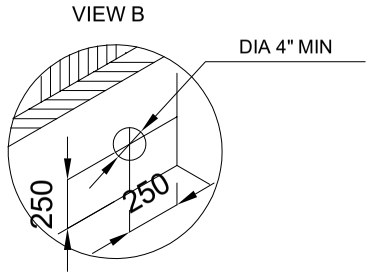

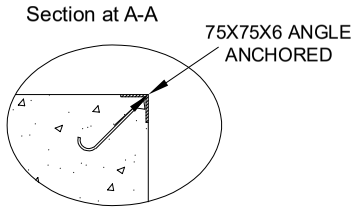

DOCK LEVELER SIZE	WIDTH (W)	LENGTH (L)	HEIGHT (H)	LIP (C) LENGTH
	2130	2730	600	450
PIT DIMENSION	WIDTH (W 1)	LENGTH (L 1)	DEPTH (D)	
DL	2180	2760	605	

Capacity:- 6Ton 15 Ton UDL

NOTE: -
1. PROPER DRAINAGE SHOULD BE DONE
2. TRENCH AS SHOWN SHOULD BE MADE BY DECIDING THE POWER PACK POSITION.
3. LEVEL OF THE PIT SHOULD BE PLAIN AND SHOULD TAKE AT LEAST 18000 KG FLOOR LOADING
4. FABRICATION TOLERANCE FOR PLATFROM SIZE WILL BE ± 15 MM.
5.PIT,DUCT FOR HOSES & ALL CIVIL WORK IN CLIENT SCOPE

Rev No.	Revision	Date	Revised By

This drawing & design is the property of NIHVA TECHNOLOGIES. Not to be sold or copied to any other concern.

TITLE:- DOCK LEVELER GA DRAWING

	NAME	DATE	SIGN
DRAWN	SUJATA	22/12/2021	
CHECK	GANESH.P	22/12/2021	
APPRD.	A.K		

If any queries contact : design@nihva.com

ALL DIMENSION ARE IN mm

NIHVA
NIHVA TECHNOLOGIES PVT. LTD.
NIHVA TECHNOLOGIES PVT. LTD. PUNE
Tel : 020 66304033
Email:- info@nihva.com
Website:- www.nihva.com

CLIENT - Elegant Offset Printers Private Limited
LOCATION - BELGAUM
PRODUCT - DOCK LEVELER
DWG NO:-NIHVA/21-22/CLT/0273 | REV- 0
SCALE: NTS | SCALE:-- 1:1 | SHEET: 01 OF 01