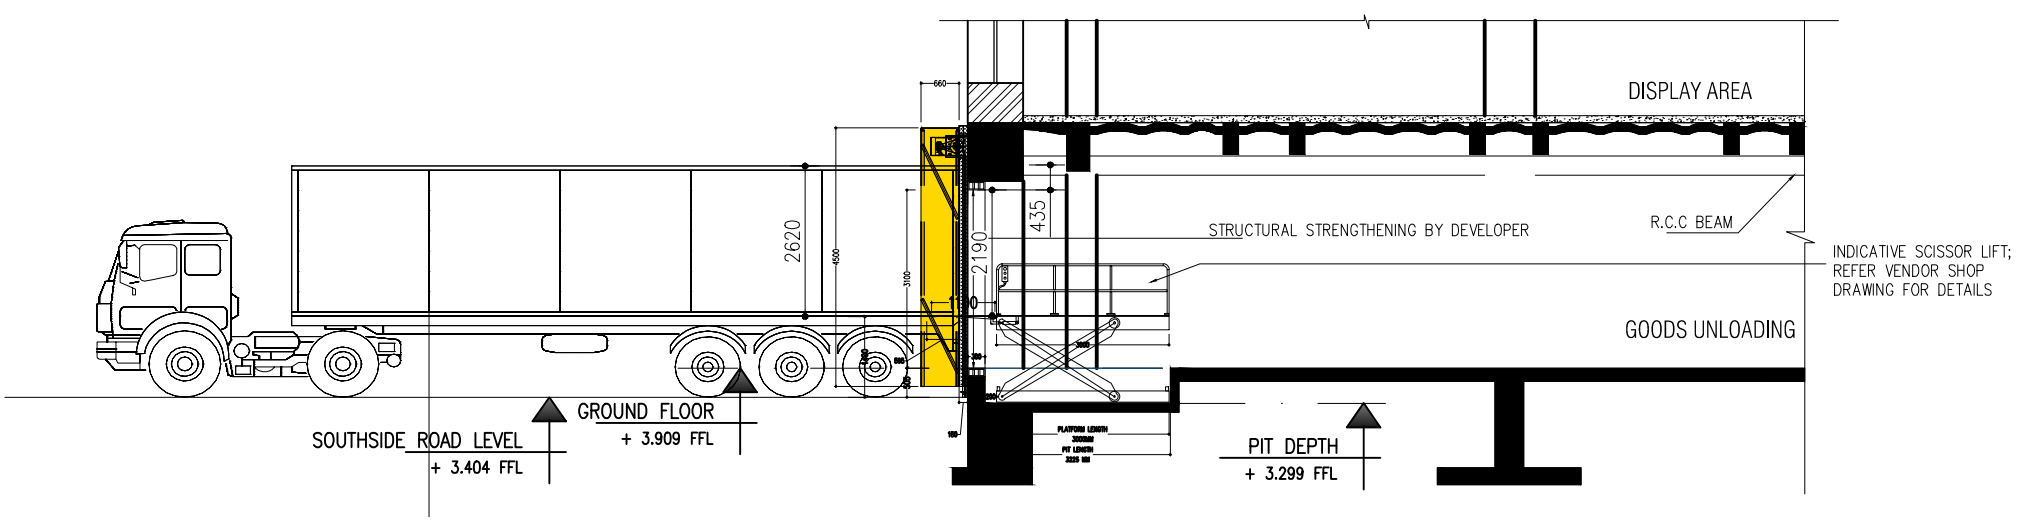

TRUCK
SCISSOR LIFT
DISPLAY AREA
R.C.C BEAM
STRUCTURAL STRENGTHENING BY DEVELOPER
INDICATIVE SCISSOR LIFT;
REFER VENDOR SHOP
DRAWING FOR DETAILS
GOODS UNLOADING
660
2620
435
2190
SOUTHSIDE ROAD LEVEL
+ 3.404 FFL
GROUND FLOOR
+ 3.909 FFL
PIT DEPTH
+ 3.299 FFL