



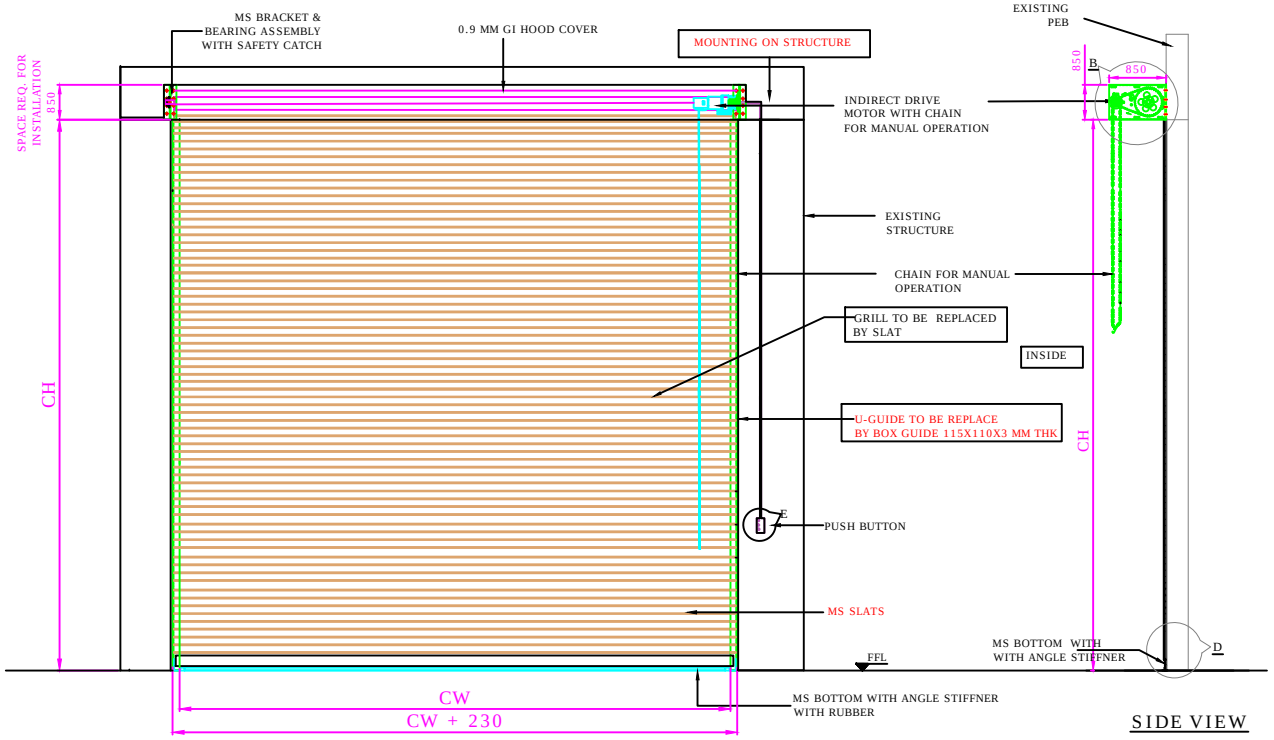


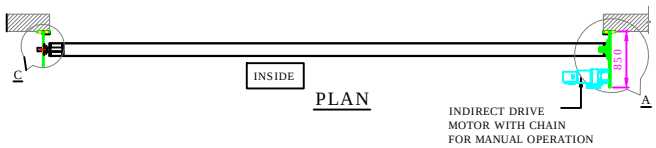

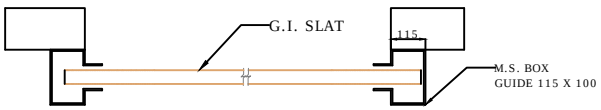


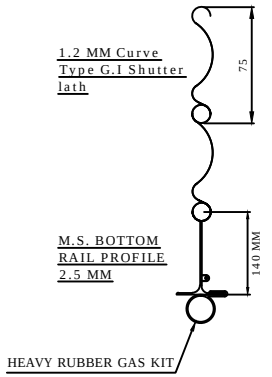


DETAILS : D

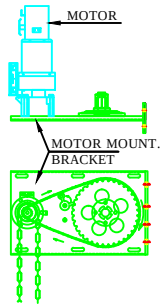

DETAILS : A & B

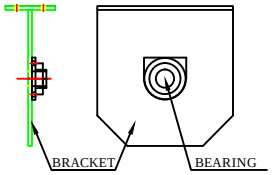

DETAILS : C

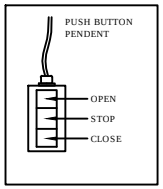

DETAILS : E

REV NO	DATE	DRAWN	REMARK

SR NO	CLEAR WIDTH(CW)	CLEAR HEIGHT(CH)	QTY	LOCATION	RAL CODE	MOTOR POSITION (LH/RH FROM INSIDE)
1	6000	6000	1	SHOP		RH

This drawing & design is the property of NIHVA TECHNOLOGIES. Not to be sold or copied to any other concern.

TITLE- GI SLAT MOTORIZED ROLLING SHUTTER

NIHVA TECHNOLOGIES PVT. LTD.

NIHVA TECHNOLOGIES PVT. LTD. PUNE
Tel : 020 66304033
Email:- info@nihva.com
Website:- www.nihva.com

	NAME	SIGN	DATE
DRAWN	SIDDHESHWAR		12.12.2020
CHECK	K.P.		12.12.2020
APPRD.	V.T.		12.12.2020

CLIENT - NIHVA TECHNOLOGIES PVT LTD

PROJECT - NIHVA TECHNOLOGIES PVT LTD

SITE LOCATION - PUNE

If any queries contact : projectsupport@nihva.com

DWG. NO. : NIHVA/20-21/0001 REV- R00

ALL DIMENSION ARE IN mm

SCALE: NTS WT: SHEET: