


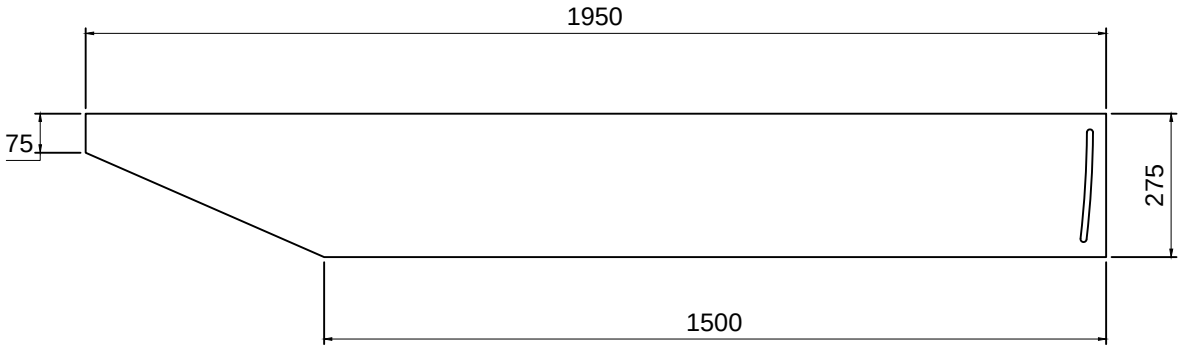


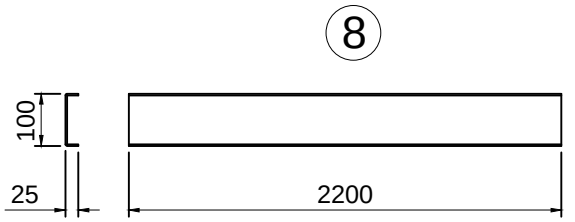

THK : 3 MM
QTY : 12 NOS

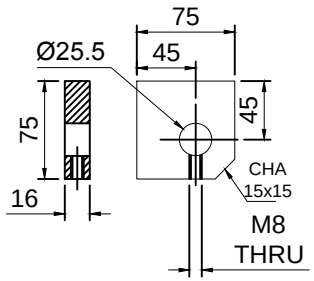

4

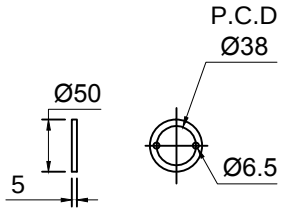

2. Ø50 X 8L = 2 NOS
ALLEN CSK M6 X 20L = 4 NOS

This drawing & design is the property of NIHVA TECHNOLOGIES. Not to be sold or copied to any other concern.

TITLE				
DECK DETAILS				NIHVA TECHNOLOGIES PVT. LTD.
	NAME	SIGN	DATE	
DRAWN	P.A		10.01.2020	CLIENT -
CHECK	G.J		10.01.2020	PROJECT -
APPRD.				SITE LOCATION -
If any queries contact : design@nihva.com				DWG. NO. : NIHVA/19-20/VDR/281
ALL DIMENSION ARE IN mm				SCALE: NTS / WT: / REV- 00

NIHVA TECHNOLOGIES PVT. LTD. PUNE
Tel : 020 66304033
Email:- info@nihva.com
Website:- www.nihva.com