
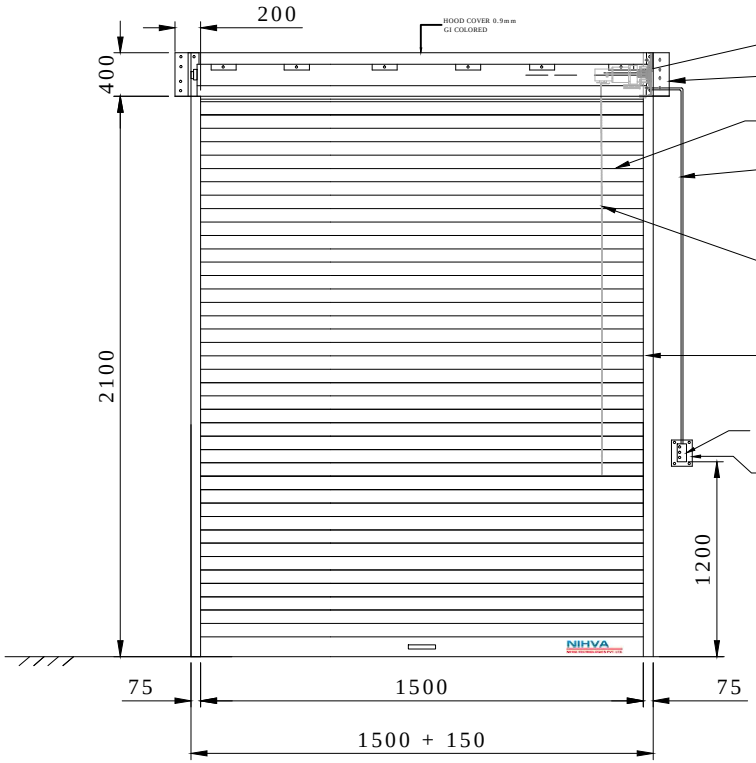
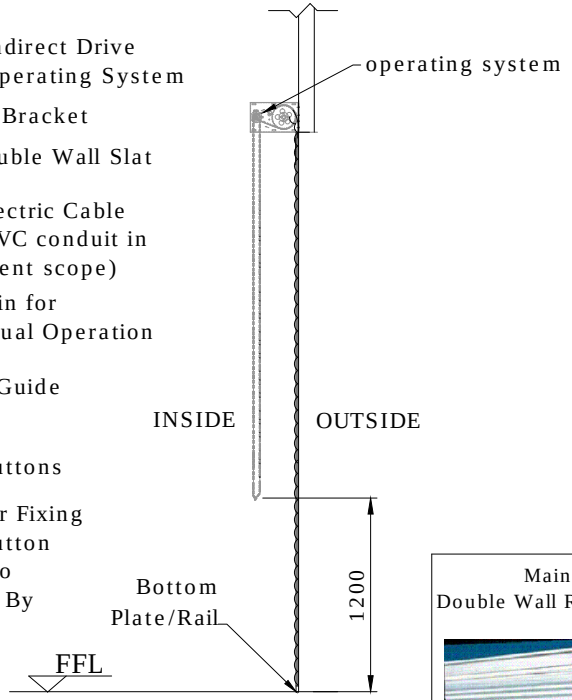
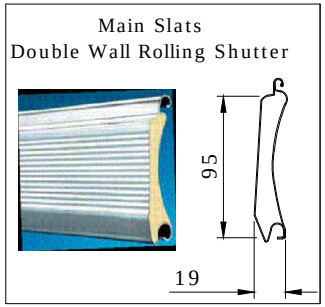
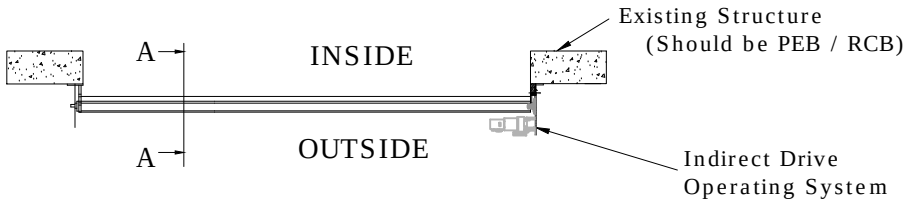



Section A-A

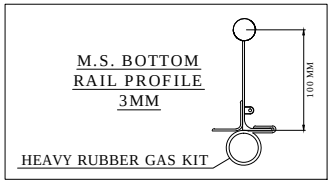


SHUTTER COLOR- RAL 9010 (PURE WHITE)

| CLEAR WIDTH (CW) | CLEAR HEIGHT (CH) | QUANTITY |
|---|---|---|
| 1500mm | 2100mm | 1 NOS |

DIMENSION :

| CLEAR WIDTH | CLEAR HEIGHT | QUANTITY |
|---|---|---|
| 1500mm | 2100mm | 1 NOS |

MATERIAL :

THICKNESS :

NIHVA TECHNOLOGY PVT. LTD. PUNE
Email:- info@nihva.com
Website:- www.nihva.com

TITLE:

DOUBLE WALL ROLLING SHUTTER

CLIENT'S APPROVAL :

CLIENT -

PROJECT -

SITE LOCATION -

DWG. NO. : NIHVA/17-18/VDR/0116

| SCALE: NTS | WT: | SHEET:1 OF 1 |
|---|---|---|

| | |
|---|---|
| DRAWN BY: OMKAR | DATE: 16-09-2017 |
| CHECKED BY : SHEKHAR | DATE: 16-09-2017 |
| APPROVED BY : SHEKHAR | DATE: 16-09-2017 |

If any queries contact : projects@nihva.com

NOTE: ALL DIMENSION ARE IN mm

THIS DRAWING & DESIGNING IS THE PROPERTY OF NIHVA TECHNOLOGIES. NOT BE SOLD OR COPY TO ANY OTHER CONCERN.