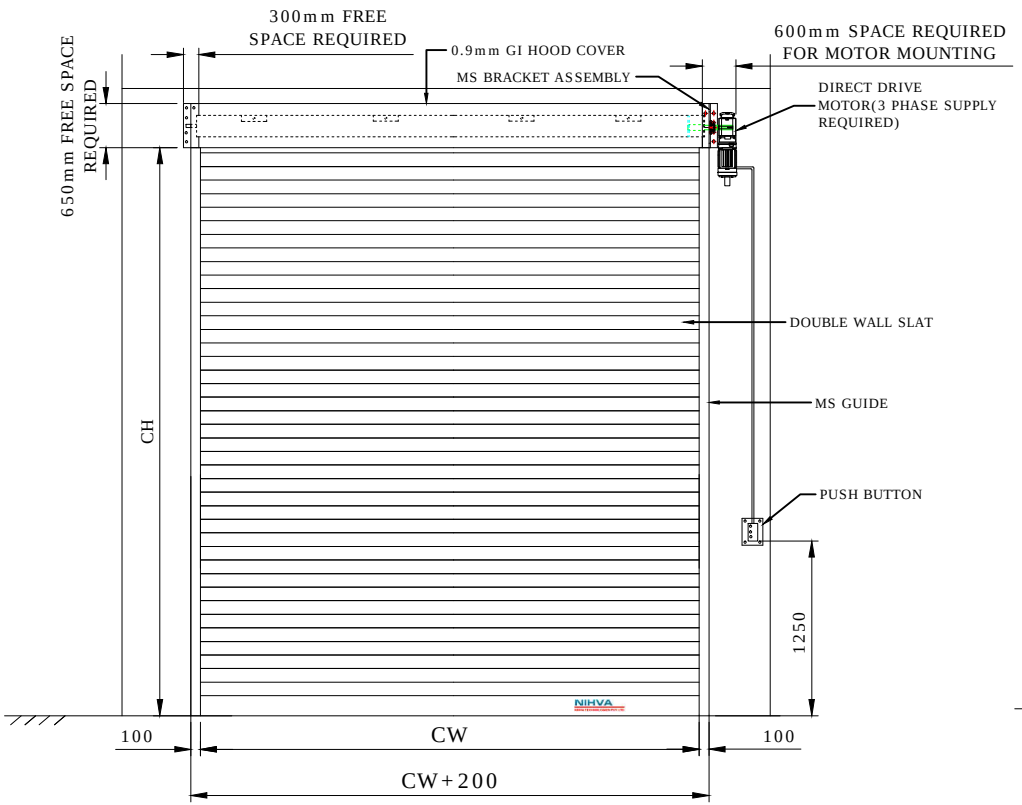

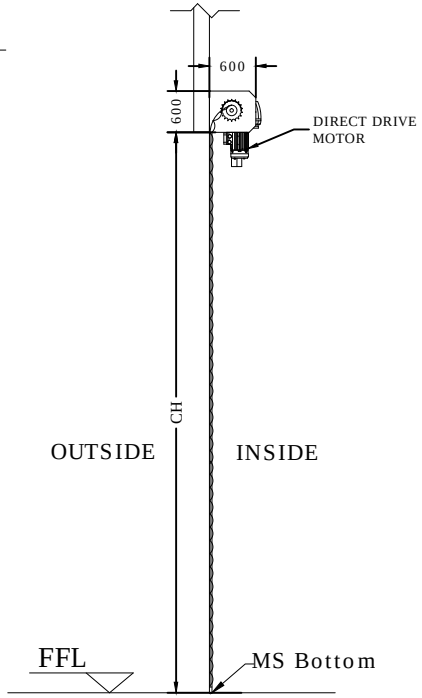

Section A-A

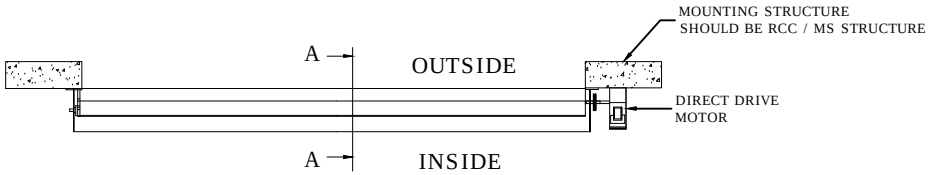

Main Slats
Double Wall Rolling Shutter

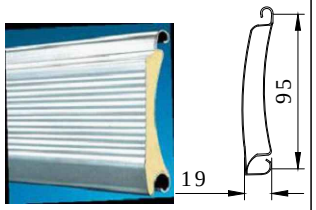

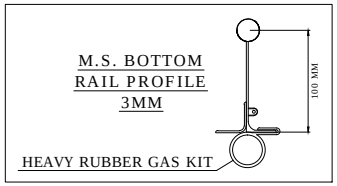

STANDARD COLOR OF SLATS & SHUTTER -RAL9002 (GRAY WHITE)

REV NO	DATE	DESCRIPTION
REV -0	03-02-2018	INITIAL DRAWING
REV -1	05-02-2018	SHUTTER HEIGHT & WIDTH REVISED LOCATIONS SPECIFIED

CLEAR WIDTH (CW)	CLEAR HEIGHT (CH)	LOCATION	QUANTITY
3000 mm	3500 mm	BWS 1 BALSA	1 NOS
2895 mm	3530 mm	BWS 2 BALSA	1 NOS

DIMENSION :

CLEAR WIDTH	CLEAR HEIGHT	QUANTITY
3000 mm	3500 mm	1 NOS
2895 mm	3530 mm	1 NOS

MATERIAL :

THICKNESS :

NOTE:-

1.STRUCTURE FOR SHUTTER FOR SHUTTER WILL BE IN CLIENT'S SCOPE.

2. 3 PHASE SUPPLY SHOULD BE PROVIDED.

NIHVA TECHNOLOGIES PVT. LTD. PUNE
Email:- info@nihva.com
Website:- www.nihva.com

TITLE:

DOUBLE WALL ROLLING SHUTTER

CLIENT'S APPROVAL :

CLIENT - LM WIND POWER BLADES (INDIA) PVT. LTD.

PROJECT -

SITE LOCATION - BANGALORE

DWG. NO. : NIHVA/17-18/0347 | REV- 1

SCALE: NTS | WT: | SHEET:1 OF 1

DRAWN BY: OMKAR | DATE: 03-02-2018

CHECKED BY: SHEKHAR | DATE: 03-02-2018

APPROVED BY : SHEKHAR | DATE: 03-02-2018

If any queries contact : projects@nihva.com

NOTE: ALL DIMENSIONS ARE IN mm

THIS DRAWING & DESIGN IS THE PROPERTY OF NIHVA TECHNOLOGIES. NOT TO BE SOLD OR COPIED TO ANY OTHER CONCERN.