

THIS PRINT IS THE PROPERTY OF NIHVA TECHNOLOGIES PVT LTD
RETURNED UPON REQUSETTHIS PART MUST NOT BE SOLD TO ANY OTHER CONCERN

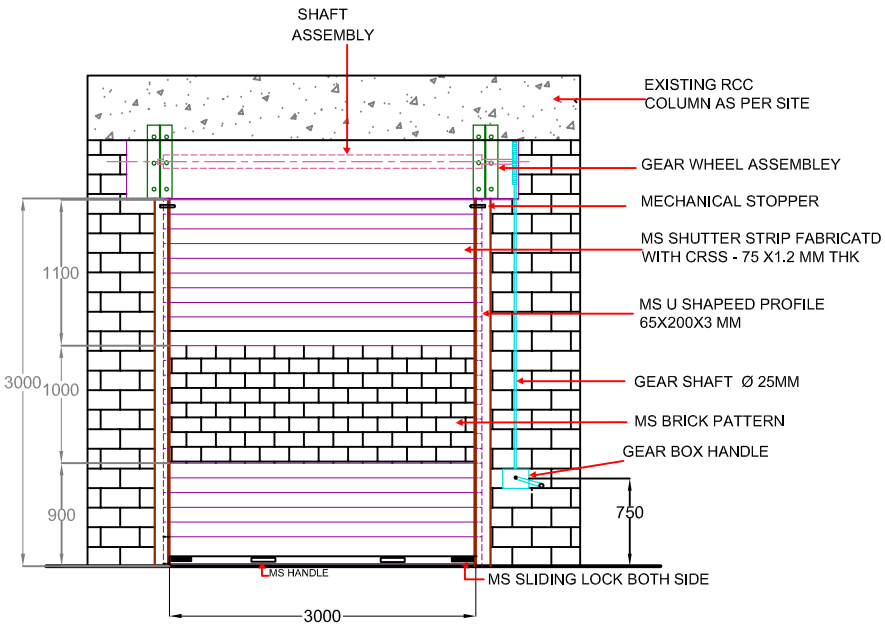


INSIDE ELEVATION


Clear Opening size:-
(W)3.0m x (H)3.0m

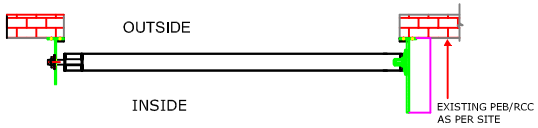


PLAN

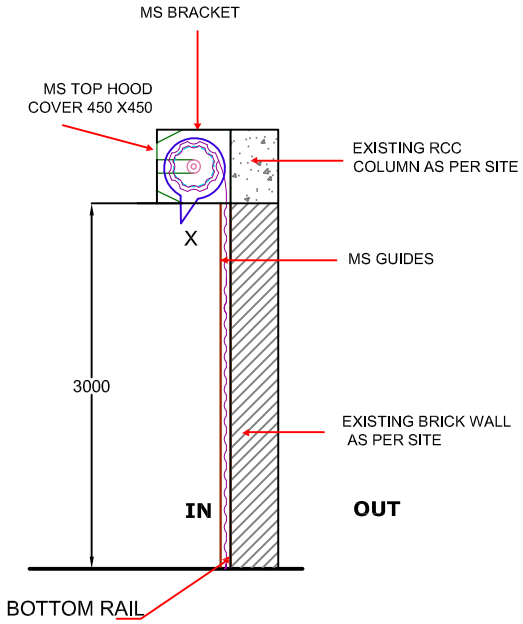

SIDE VIEW

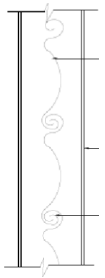

Curve Type Slat Profile

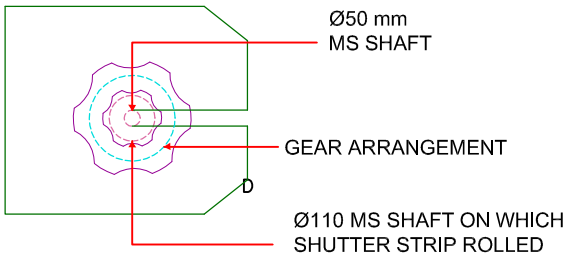

Bracket

NOTE :- Total no. of shutter is 20 nos.

Location :- Substation
Size :- 3.0m(W) X 3.0M (H)
Qty :- 10 nos

Location :- Fire sump
Size :- 3.0m(W) X 3.0M (H)
Qty :- 10 nos

TITLE: Grilled Manual Gear Operated Rolling Shutter	DO NOT SCALE DRAWING		NIHVA TECHNOLOGIES PVT. LTD. Pune:-411044
		SIGN	DATE	NIHVA TECHNOLOGIES PVT. LTD. Tel :- 020 66304033 Email :- info@nihva.com
CLIENTS APPROVEL:-	DRAWN	Anil		CLIENT: REWARD CONSTRUCTION
	CHECK			PROJECT / SITE: IR PROJECT/ NAROL - AHEMDABAAD
	ENG			PRODUCT NAME:
ALL DIMENSION ARE IN M.M.	APPRD.			DWG. NO.: NVA/REWARD/01
	PROD			REV.: 0
	MFG			SCALE: NTS WT: SHEET: 1 OF 1
	Ref. No.			