

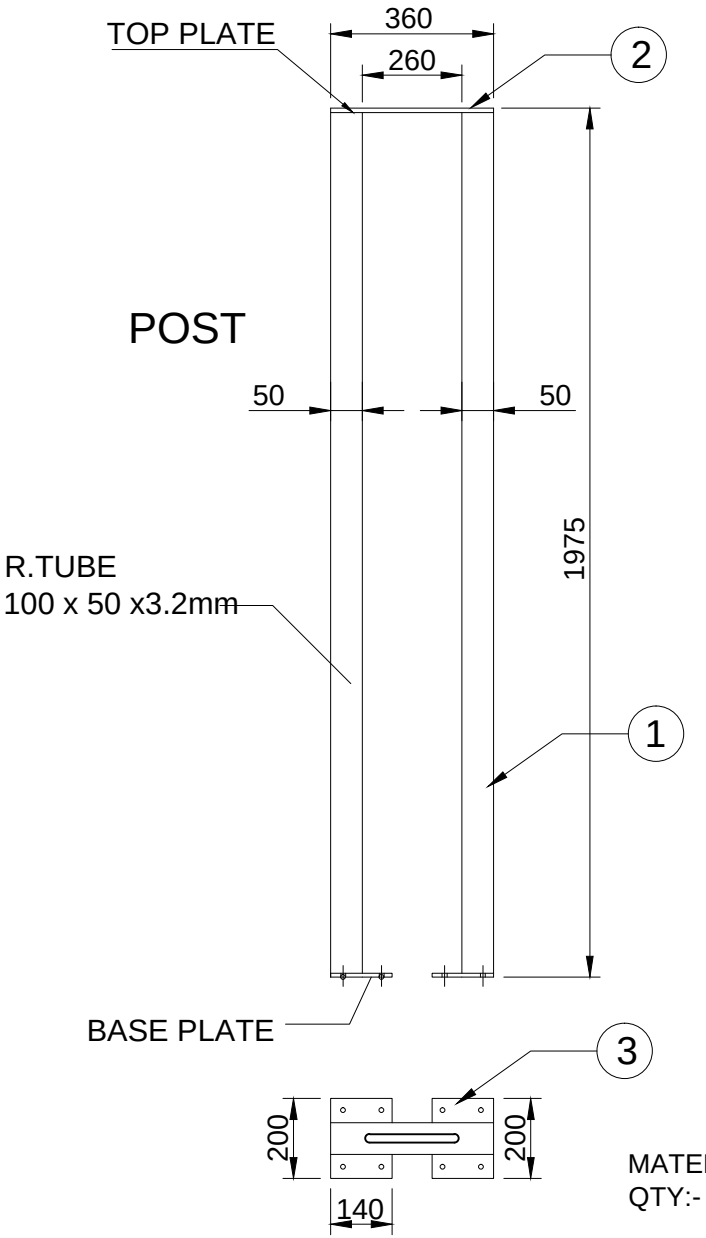


MATERIAL:-MS
QTY:- 04 NOS

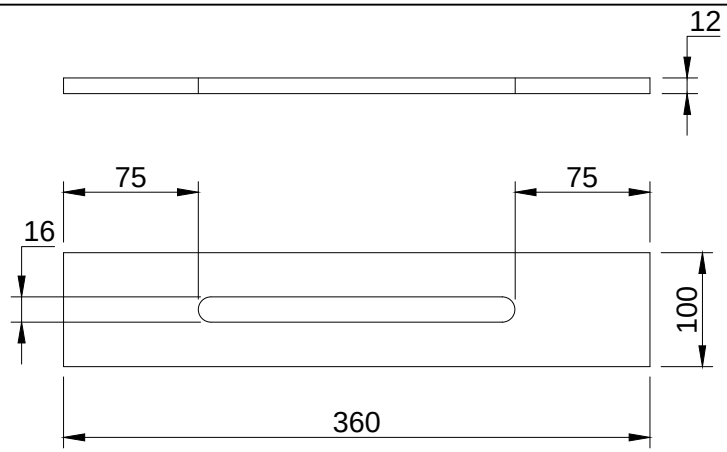

TOP PLATE

MATERIAL:-MS
THICKNESS:-12 mm
QTY:- 04 NOS

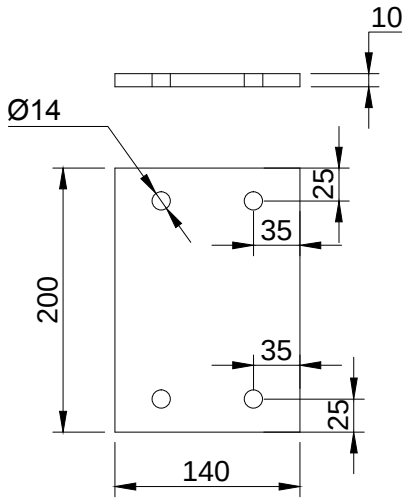

BASE PLATE

MATERIAL:-MS
THICKNESS:-10mm
QTY:- 08 NOS

SR NO	DESCRIPTION	SPECIFICATION	QTY
4	ANCHOR BOLT	M12 X 150L	32 NOS
3	FLAT	200 X 10 X 140L	8 NOS
2	PROFILE	100 X 12 X 360L	4 NOS
1	R.TUBE	100 X 50 X 3.2 THK X 1950L	8 NOS

TOLERANCE- ±2mm

This drawing & designing is the property of NIHVA TECHNOLOGIES. Not to be sold or copied to any other concern.

TITLE: SLIDING GATE POST DRAWING

	NAME	SIGN	DATE
DRAWN	P.A		30.01.20
CHECK	G.J		30.01.20
APPROVAL			

NIHVA TECHNOLOGIES PVT. LTD.
NIHVA TECHNOLOGIES PVT. LTD. PUNE
Tel : 020 66304033
Website:- www.nihva.com
Email:- info@nihva.com

CLIENT -
PROJECT -
SITE LOCATION -

If any queries contact : design@nihva.com
DWG. NO. : NIHVA/19-20/VDR/301
REV.:- 00
ALL DIMENSION ARE IN mm
SCALE: NTS
WT:
SHEET: 01 OF 01