
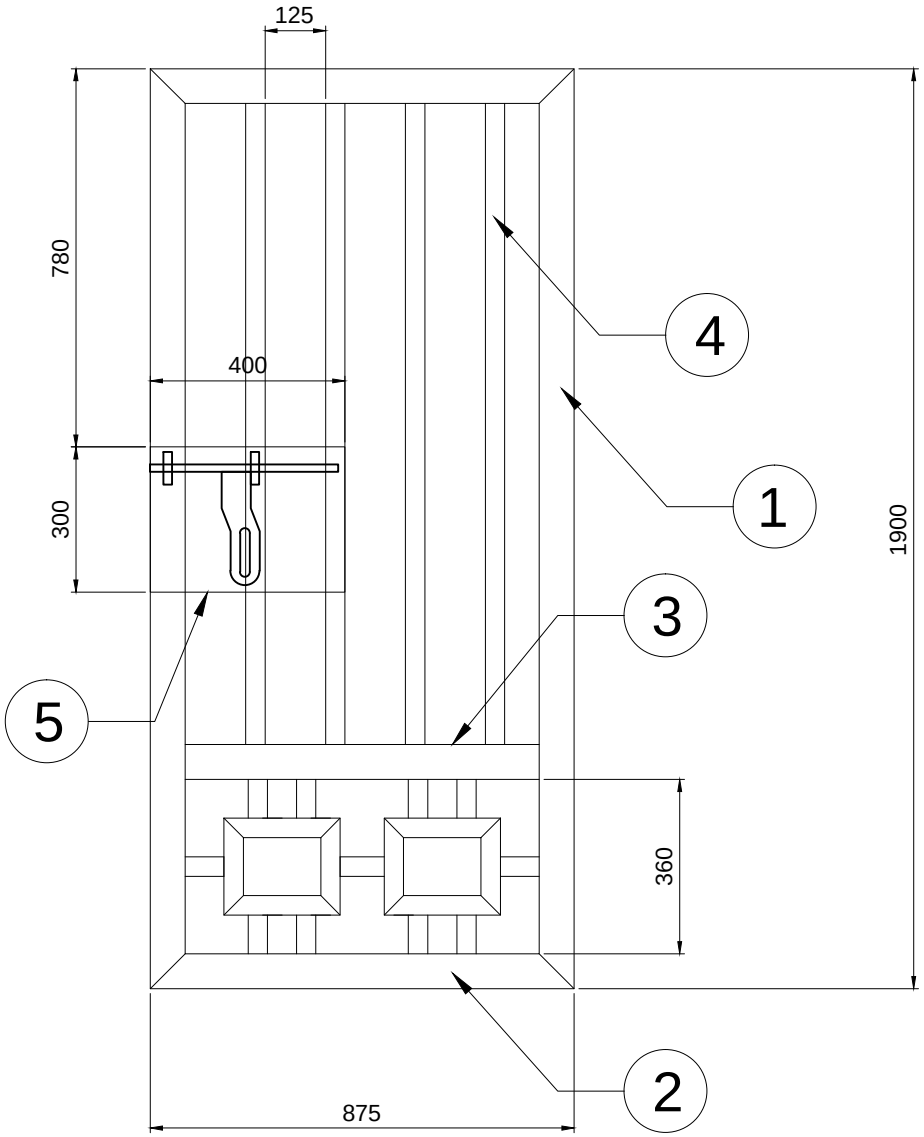


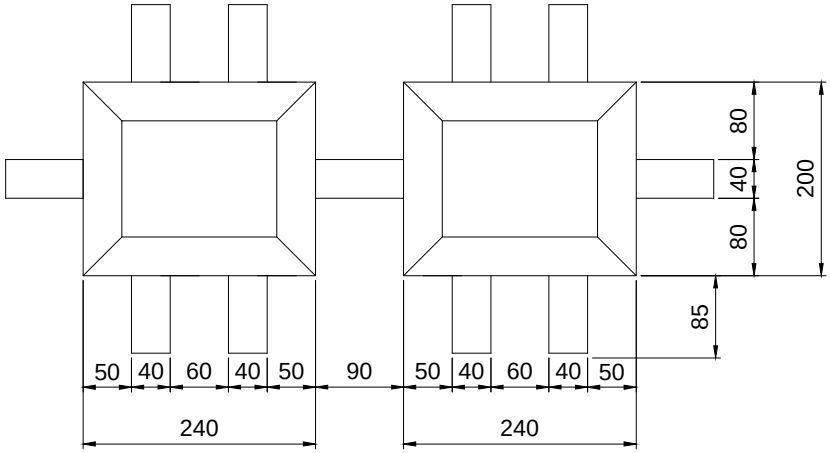

SR NO	DESCRIPTION	SPECIFICATION	QTY
5	PLATE	300 X 5 X 400L	2 NOS
4	SQ.TUBE	40 X 40 X 2.6 X 1325L	4 NOS
3	SQ.TUBE	72 X 72 X 3.2 THK X 730L	1 NO
2	SQ.TUBE	72 X 72 X 3.2 THK X 875L	2 NOS
1	SQ.TUBE	72 X 72 X 3.2 THK X 1900L	2 NOS

TOLERANCE - ±2mm

This drawing & design is the property of NIHVA TECHNOLOGIES. Not to be sold or copied to any other concern.

TITLE: WICKET GATE 02

NIHVA TECHNOLOGIES PVT. LTD.
NIHVA TECHNOLOGIES PVT. PUNE
Tel : 020 66304033
Email:- info@nihva.com
Website:- www.nihva.com

	NAME	SIGN	DATE
DRAWN	P.V.A		26.09.2019
CHECK	G.J		26.09.2019
APPRD.			

CLIENT -

PROJECT -

SITE LOCATION -

If any queries contact : design@nihva.com

DWG. NO. : NIHVA/19-20/VDR/160 | REV- 0

ALL DIMENSION ARE IN mm

SCALE: NTS | WT: | SHEET: 01 OF 01