


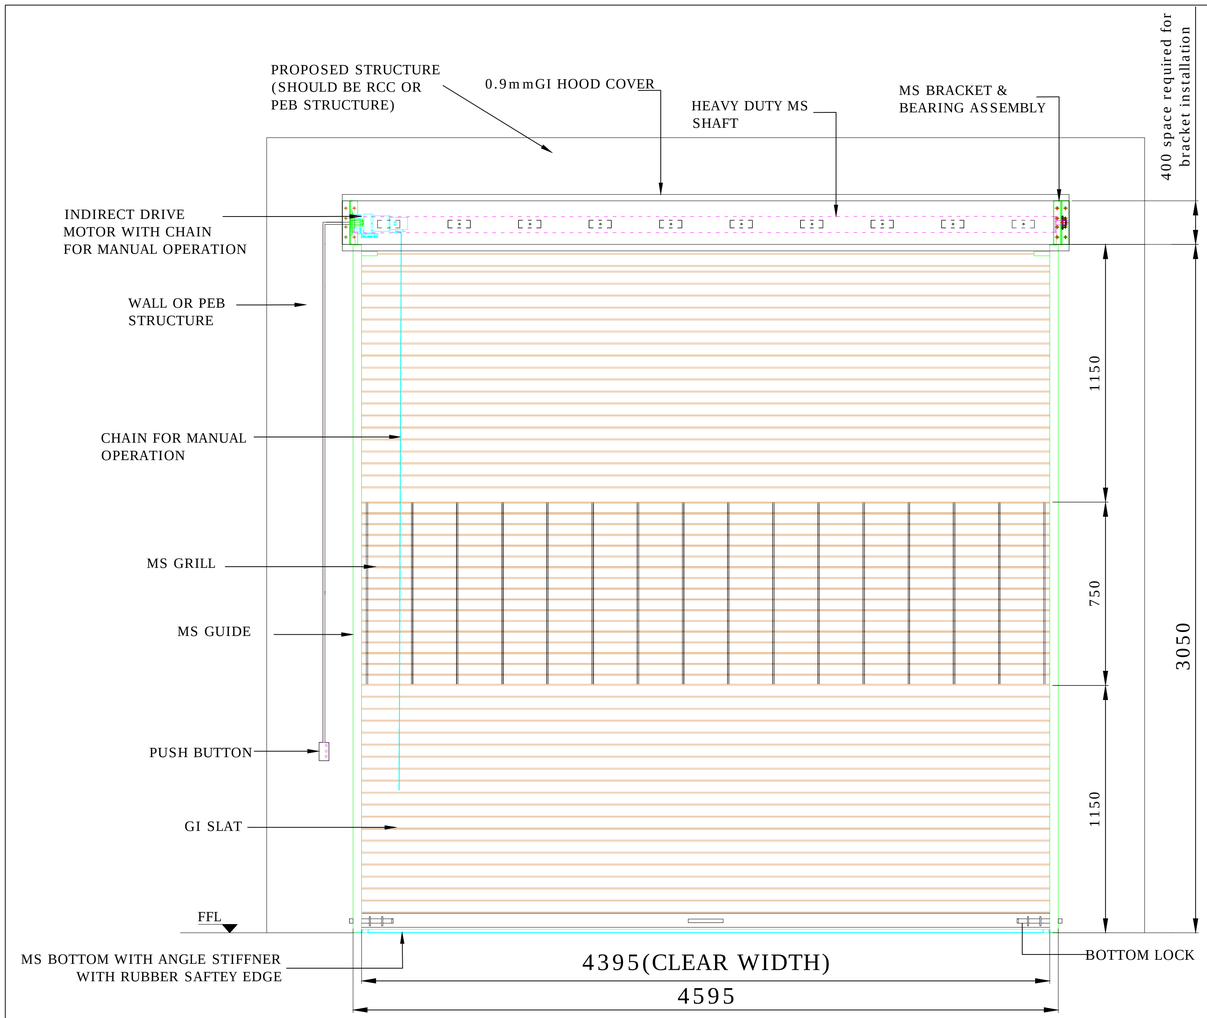


ELEVATION

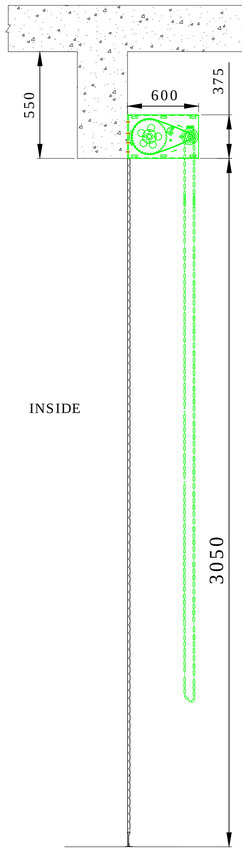


SIDE VIEW

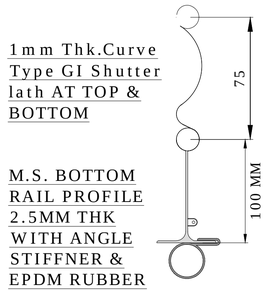


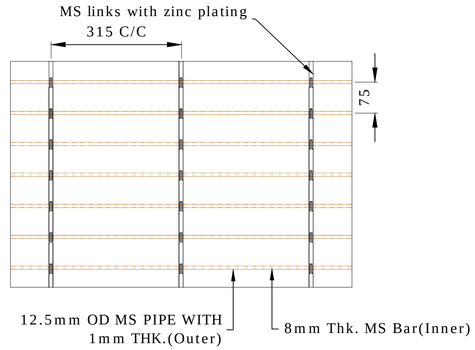


GRILL

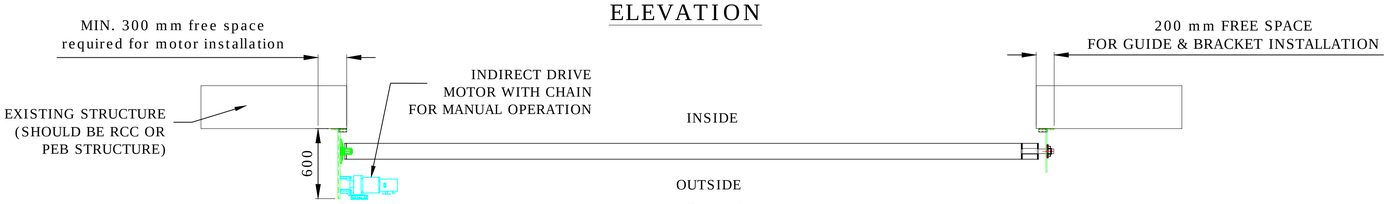

PLAN

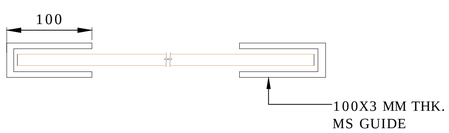

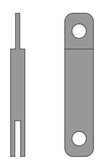

LINK/HINGE

SHOP NO-15

CLEAR WIDTH	CLEAR HEIGHT	QUANTITY
4395	3050	1

DIMENSION :		
CLEAR WIDTH	CLEAR HEIGHT	QUANTITY
4395	3050	1

MATERIAL :

THICKNESS :

NOTE-
1.Shutter will be powder coated with approved color shade.
2. Revision 2- Pattern of grill has been revised or changed.

NIHVA TECHNOLOGIES PVT. LTD.
NIHVA TECHNOLOGIES PVT. LTD. PUNE
Email:- info@nihva.com
Website:- www.nihva.com

TITLE:

G.A. MOTORIZED GRILLED ROLLING SHUTTER

CLIENT'S APPROVAL :

CLIENT - ADANI

PROJECT - WESTERN HEIGHTS PROJECT

SITE LOCATION - MUMBAI

DWG. NO. : NIHVA/17-18/0093

SCALE: NTS	WT:	SHEET:1 OF 1

DRAWN BY: SURAJ	DATE: 29-05-2017
CHECK : SAGAR P.	DATE: 29-05-2017
APPROVED : S.S	DATE: 29-05-2017

If any queries contact : projects@nihva.com

NOTE: ALL DIMENSIONS ARE IN mm

THIS DRAWING & DESIGN IS THE PROPERTY OF NIHVA TECHNOLOGIES. NOT TO BE SOLD OR COPY TO ANY OTHER CONCERN.