




SECTION U - U
1:80

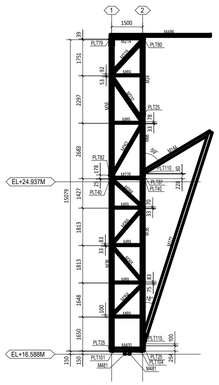


SECTION T - T
1:80

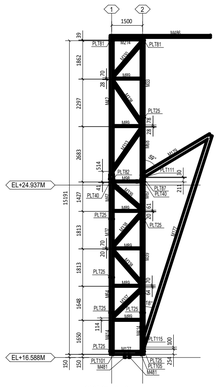


SECTION S - S
1:80

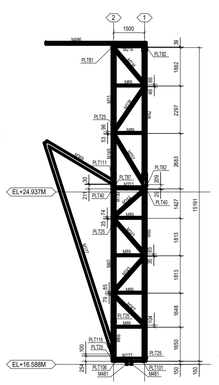


SECTION J - J
1:80

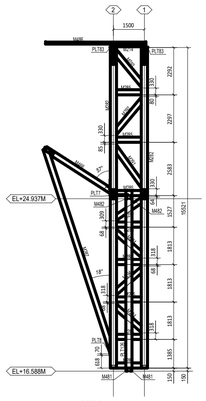


SECTION H - H
1:80

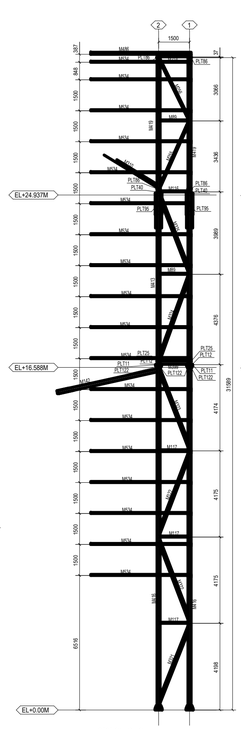


SECTION G - G
1:80

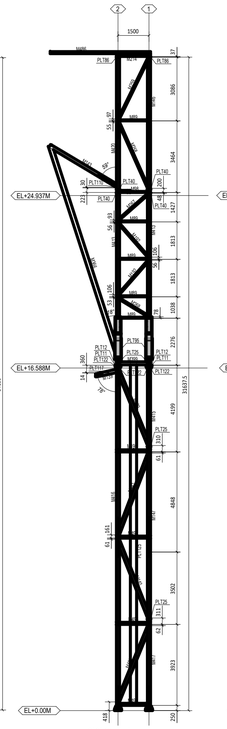


SECTION F - F
1:80

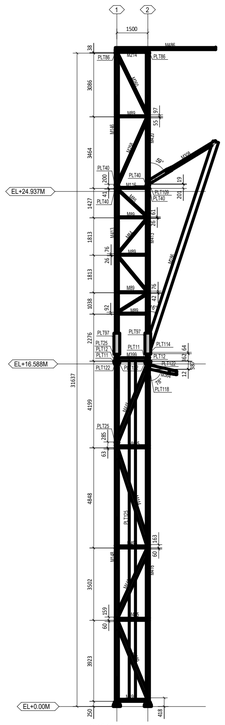


SECTION E - E
1:80

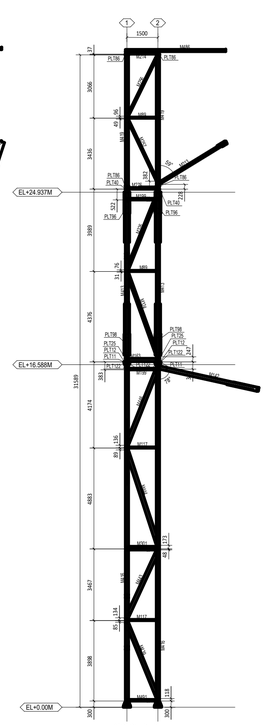


SECTION D - D
1:80

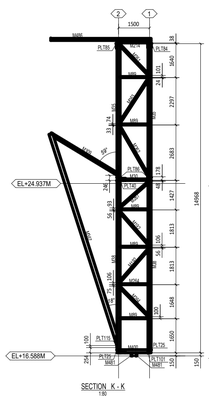


SECTION K - K
1:80

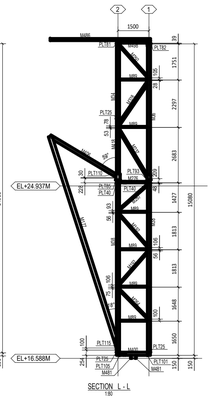


SECTION L - L
1:80

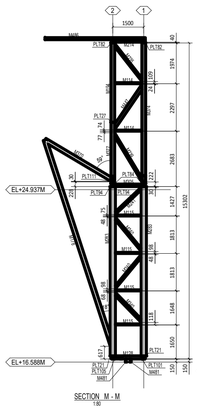


SECTION M - M
1:80

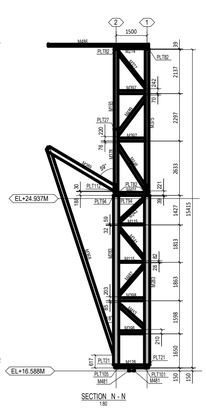


SECTION N - N
1:80

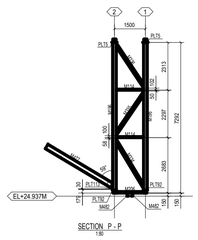


SECTION P - P
1:80

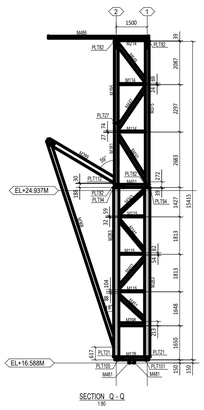

SECTION Q - Q
1:80

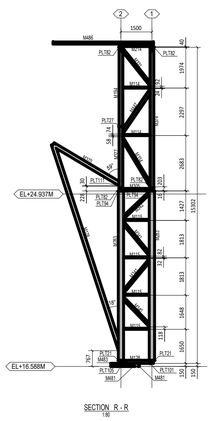

SECTION R - R
1:80

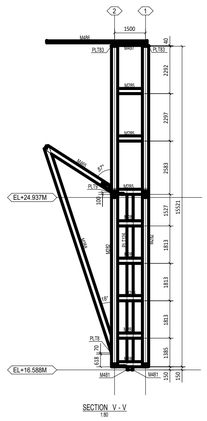

SECTION V - V
1:80

0	ISSUED FOR APPROVAL	05.11.22	IMS	HAB	HAB
REV.NO.	DESCRIPTION.	REV.DATE	DRAWN.	CHKD.	APPD.

DWG.TITLE :- DETAIL DRAWING FOR 84MTR

PROJECT	MEGADOOR INSTALLATION AT HYDRABAD AIRPORT
CLIENT	GMR

SALT Design Services
NIHVA NIHVA TECHNOLOGIES PVT. LTD.

SALT DESIGN SERVICES

NIHVA TECHNOLOGIES PVT. LTD. PUNE
Tel : 020 66304033
Email:- info@nihva.com
Website:- www.nihva.com

DRAWN :RRK	CHECKED : HAB	SCALE: 1:100
APPROVED : HAB	JOB CODE. : 1729	DATE: 05.11.2022
DWG.NO: SALT_1729_FDN_01_R0	(SH-1OF1)	REV. - R0
		SIZE. - A1

A1 [841 x 594]