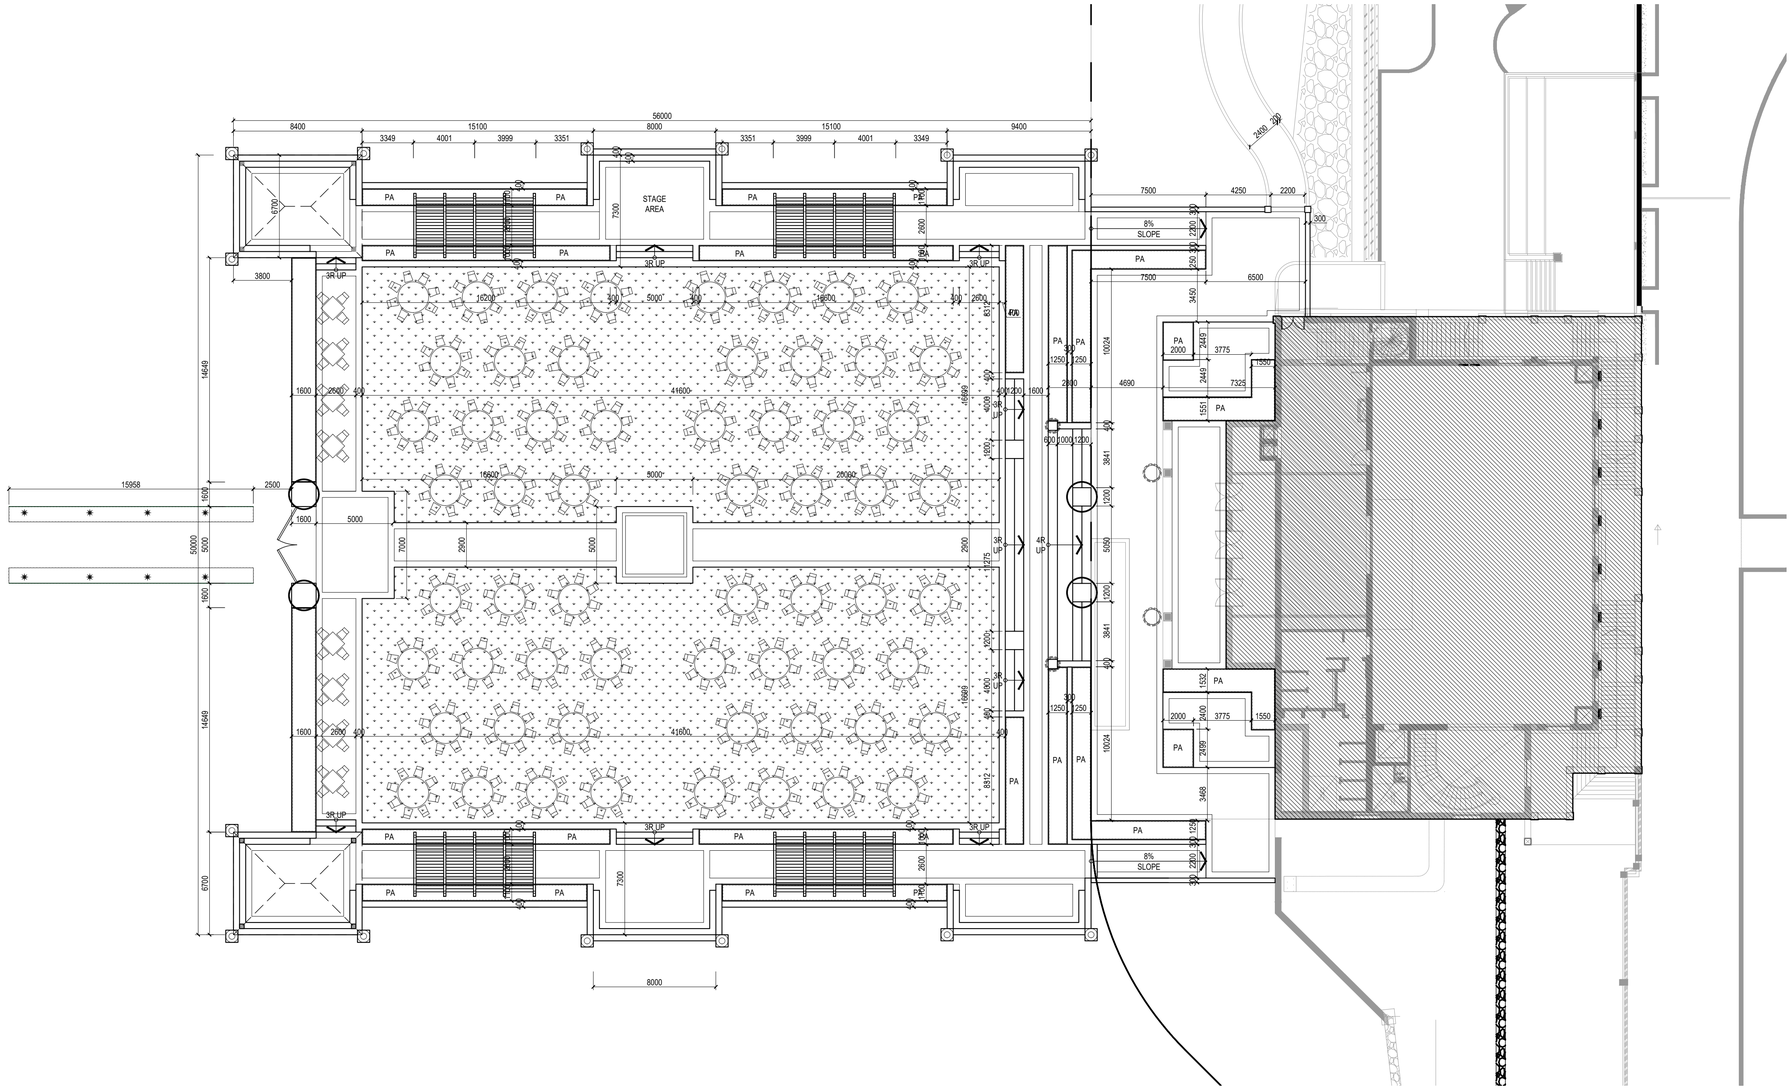


1 / 1300 SETTING OUT PLAN
SCALE: 1:200

The copyright of this drawing remains with the SQM Design and may not be reproduced without prior written consent.

Figured Dimensions are to be used in preferences to scaled sizes.

All Dimensions must be checked before commencing work on site.

This Drawing is to be read in conjunction with all other relevant Drawings.

All Proposed works to be carried out in accordance with SQM Design technical specification for landscape architectural works.

KEY PLAN:

LEGEND:

Setting Out Reference Line

Setting Out Starting Point

rev.	date	name	description
0	21-12-10	DD	100% DETAIL DESIGN

Lead Consultant:

KKD

Design Consultant:

SQUARE M DESIGN
P.O.BOX 36415, DUBAI, TEL: +971-43887158

Client:

KEF HOLDINGS

Project Name:
CHELAMBRA RESORT
INDIA

Drawing Title:
SETTING OUT PLAN

Scale:	Size:	Drawn By:	Date:	Status:
1:200	A1	RI	10 DEC 2021	DD

Drawing No.

NKDG	1140	LA	DG	1300	0
Project	Project Number	Discipline	File Type	Drawing No.	Revision