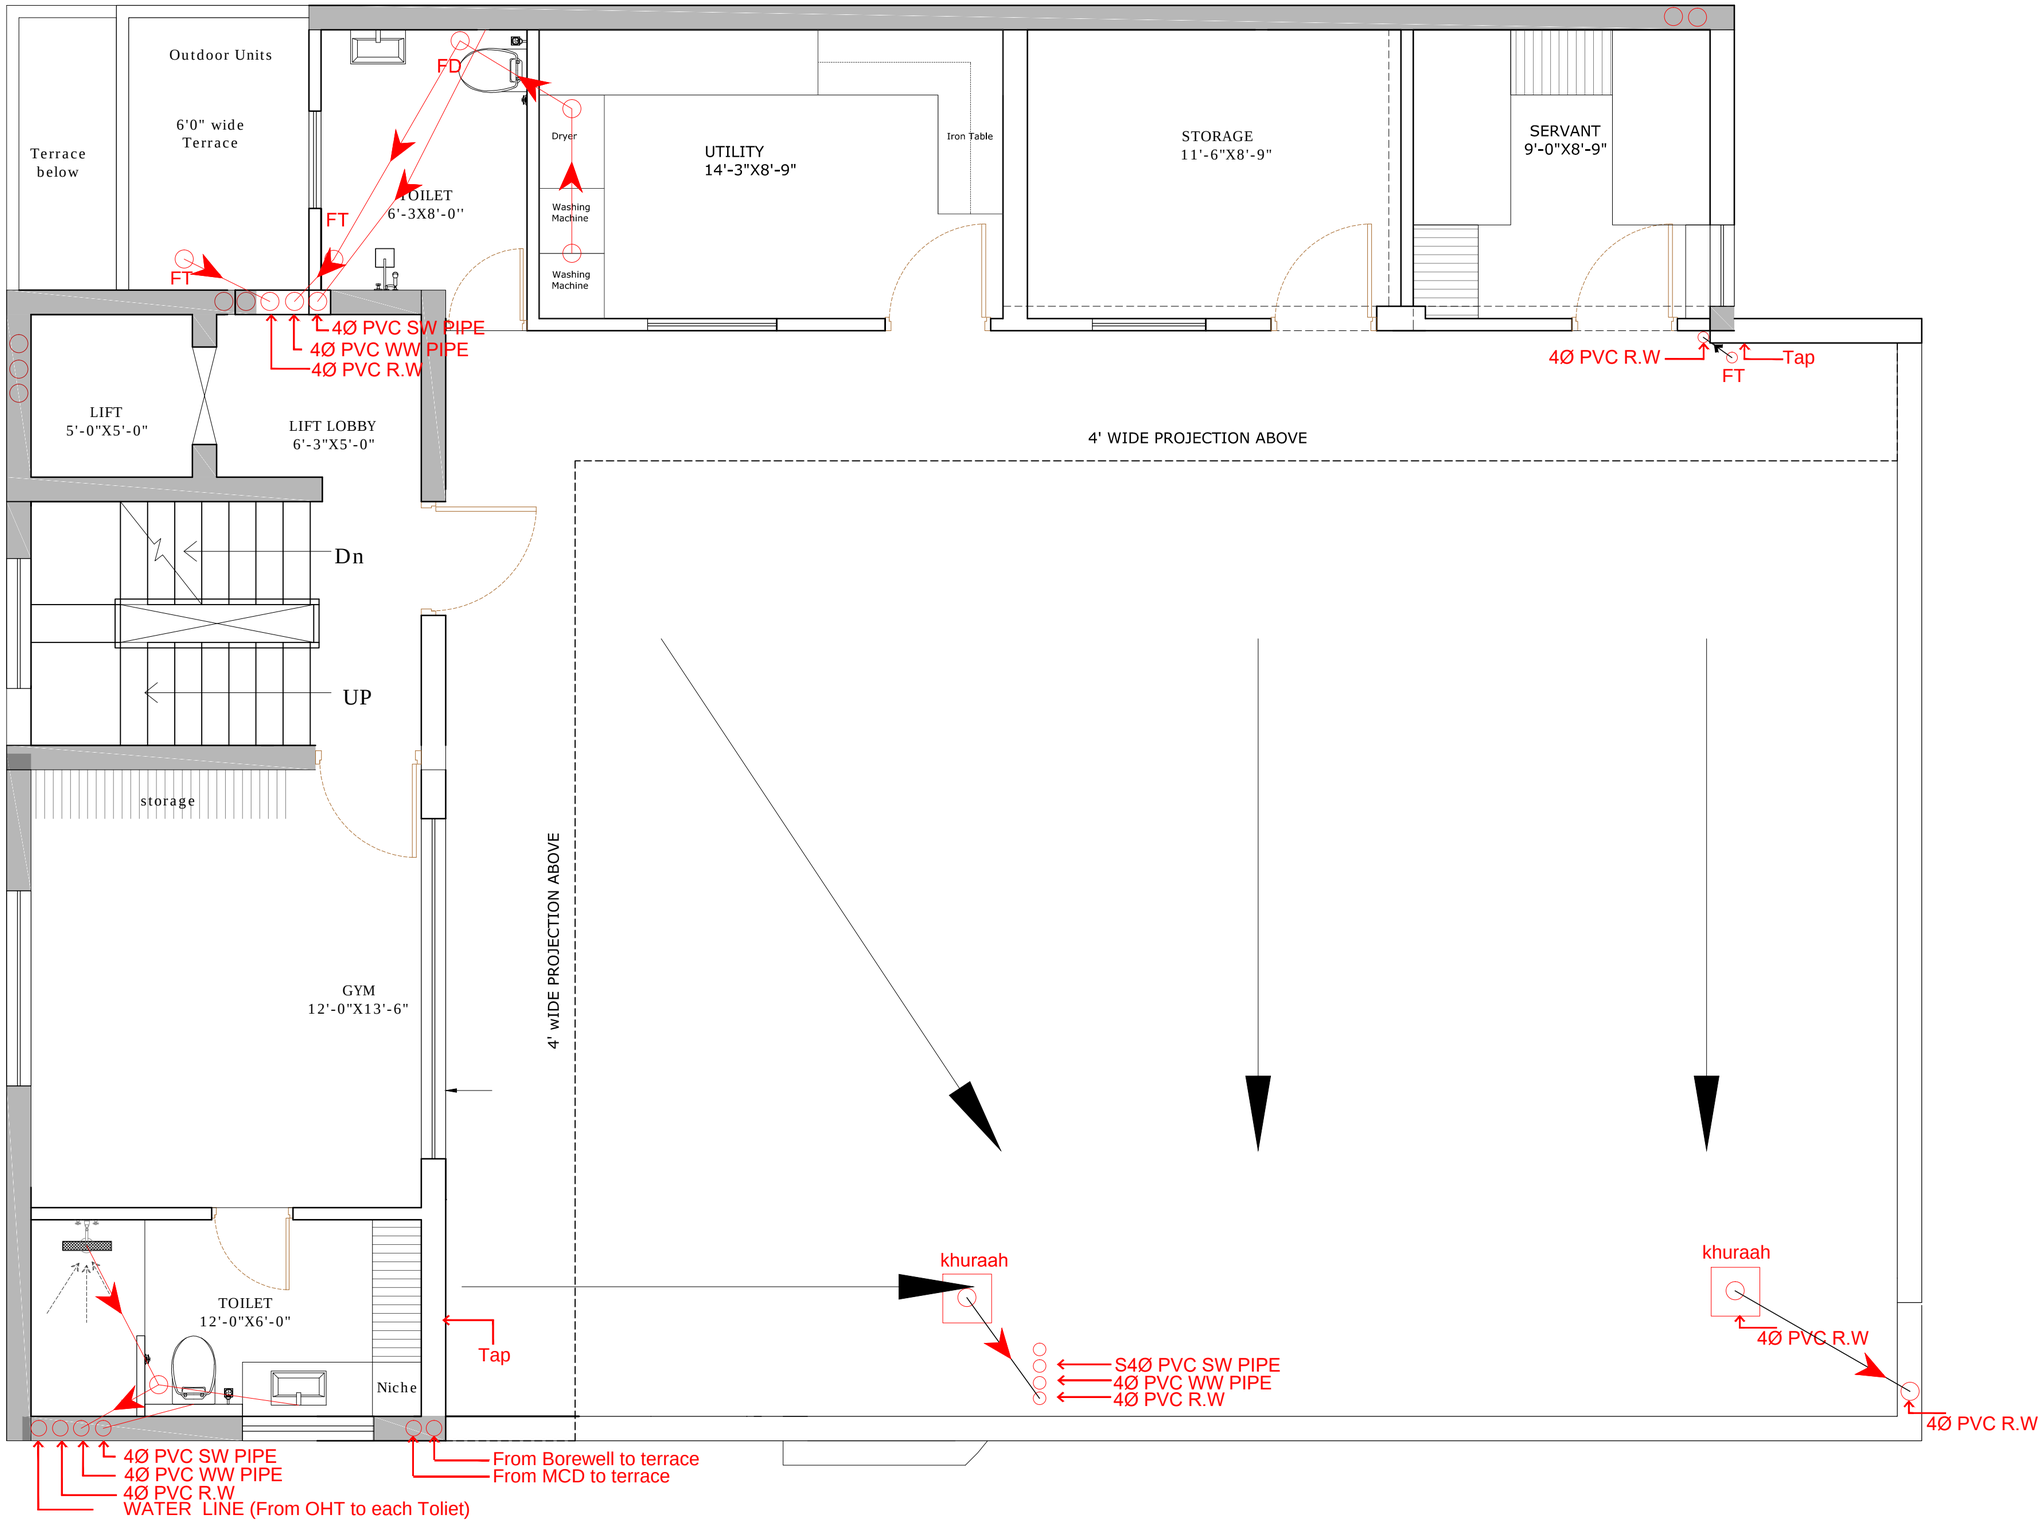


R3	---	210416
R2	---	210412
R1	---	210324
R0	---	ISSUE
No	ISSUE	DATE

210416

PROJECTCODE

PROJECT
RESIDENCE FOR
MR. NAKSH JAIN
SHAKTI NAGAR | DELHI

SHEET TITLE
Drainage layout plan _ terrace floor

TITLE4

Architect
DIVYA GOEL
arch.divyagoel@gmail.com
+91 9999882520

TITLE3 TITLE7

TITLE2 TITLE6

TITLE1 TITLE5

NOTES
1. THIS DRAWING IS THE PROPERTY OF THE DESIGNERS. NO PORTION MAY BE REPRODUCED WITHOUT THE WRITTEN PERMISSION.
2. ALL DIMENSIONS ARE TO BE VERIFIED ON THE SITE BY THE CONTRACTOR. ANY DISCREPANCIES ARE TO BE REPORTED TO THE DESIGNERS BEFORE EXECUTION.
3.THIS DRAWING IS TO BE READ IN CONJUGATION WITH THE DESIGNERS DRAWINGS AND OTHER CONSULTANTS DRAWINGS.
4. DRAWINGS NOT SHOWING THE LATEST REVISIONS TO BE CANCELLED.
5. DO NOT SCALE DRAWING. USE FIGURED DIMENSIONS ONLY.
6. ALL INDICATED LEVELS ARE FINISHED LEVELS.