


ELEVATION VIEW

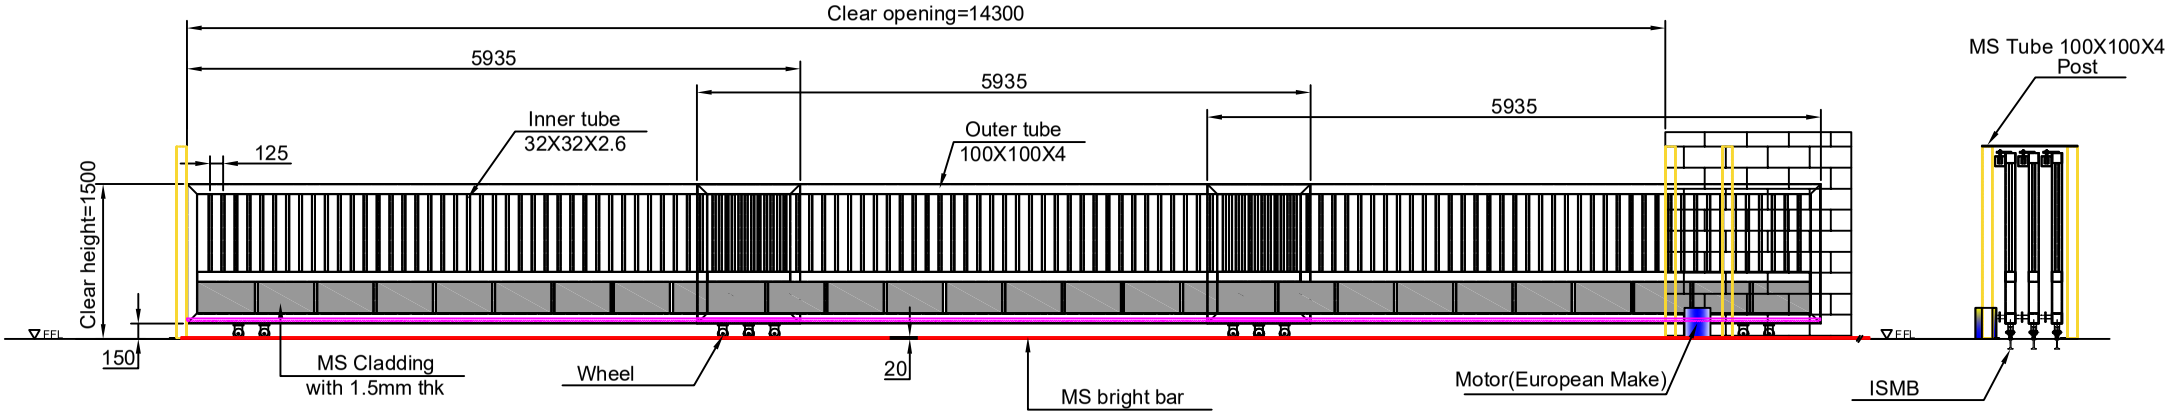

TECHNICAL SPECS FOR SWING GATE		
SL NO.	SPECIFICATION	
1	OPENING LENGTH	14300MM
2	OPENING HEIGHT	1500MM
3	OUTER TUBE	100X100X4
4	INNER TUBE	32X32X2.6
5	OPERATION	MOTORIZED

OUTSIDE
OPENING DIRECTION

Note:-
1. All dimension are in mm
2. All civil work is in client scope

Rev No.	Revision	Date	Revised By
1.	Clear Opening of the changed 15500mm to 14300mm	08/01/2022	Sujata
2.	Clear Height of the changed 1800mm to 1500mm	08/01/2022	Sujata

This drawing & design is the property of NIHVA TECHNOLOGIES. Not to be sold or copied to any other concern.

TITLE:- TELESCOPIC SLIDING GATE

NIHVA
NIHVA TECHNOLOGIES PVT. LTD.

NIHVA TECHNOLOGIES PVT. LTD. PUNE
Tel : 020 66304033
Email:- info@nihva.com
Website:- www.nihva.com

	NAME	DATE	SIGN
DRAWN	SUJATA.B	03/01/2022	
CHECK	G.PATIL	03/01/2022	
APPRD.	A.K	03/01/2022	

CLIENT - Fanidhar Mega Food Park Private Limited
LOCATION - GUJARAT
PRODUCT - TEL.SLIDING GATE
If any queries contact : design@nihva.com
DWG NO:-NIHVA/21-22/CLT/0298 REV- 0
ALL DIMENSION ARE IN mm
SCALE: NTS SCALE:-- 1:1 SHEET: 01 OF 01