



SR NO	DESCRIPTION	SPECIFICATION	QTY
1	ISMC	200 X 75 X 2010L	4 NOS
2	ISMC	200 X 75 X 1950L	1 NO
3	ISMC	200 X 75 X 1070L	2 NOS
4	ISMC	75 X 40 X 1070L	1 NO
5	ISMC	75 X 40 X 125L	4 NOS
6	R.TUBE	96 X 48 X 4.8 THK X 2025L	2 NOS
7	R.TUBE	96 X 48 X 4.8 THK X 150L	12 NOS
8	PROFILE	750 X 20 THK X 1220L	1 NO
9	PROFILE	150 X 16 THK X 200L	4 NOS
10	ISA	75 X 8 X 75L	8 NOS
11	PROFILE	350 X 16 THK X 2025L	2 NOS
12	PROFILE	435 X 16 THK X 2025L	2 NOS

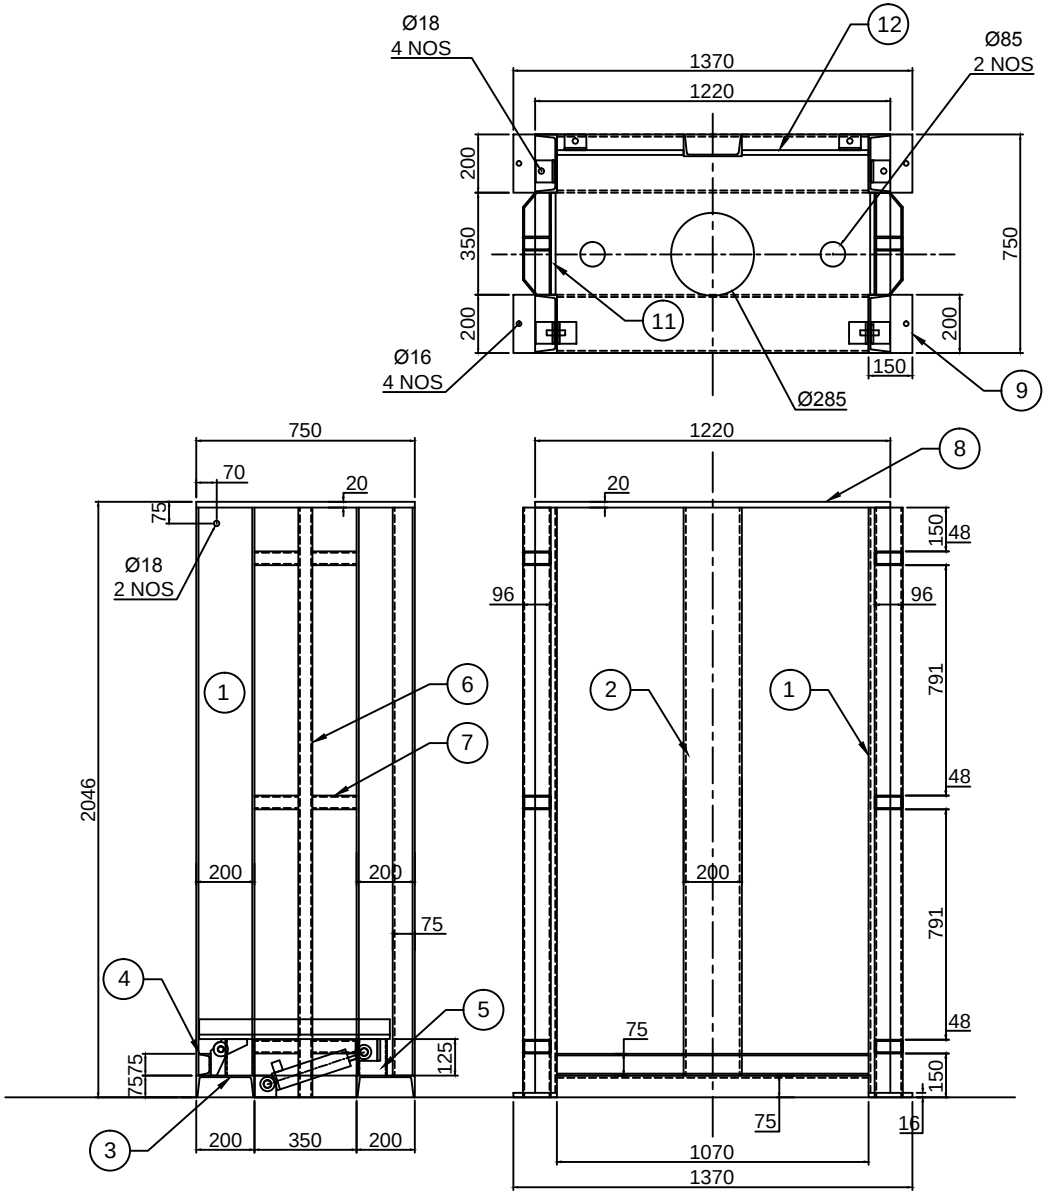

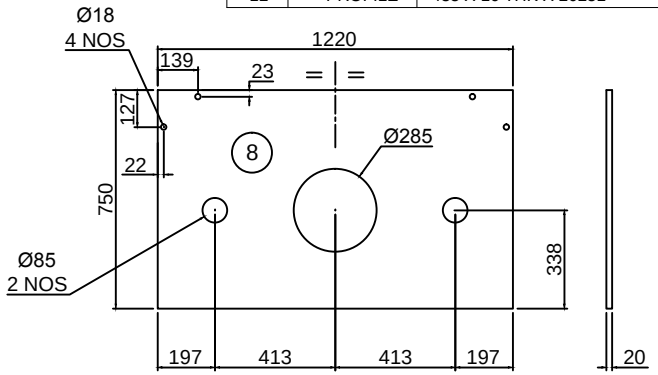

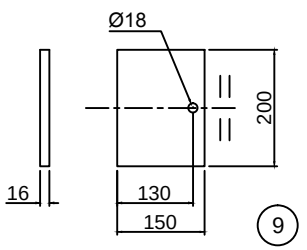

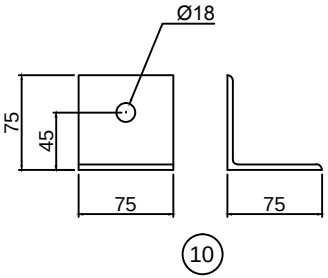

This drawing & design is the property of NIHVA TECHNOLOGIES. Not to be sold or copied to any other concern.

TITLE: MAIN BODY FRAME

	NAME	SIGN	DATE
DRAWN	P.A		22.10.2019
CHECK	G.J		22.10.2019
APPRD.			

If any queries contact : design@nihva.com

ALL DIMENSION ARE IN mm

NIHVA TECHNOLOGIES PVT. LTD.

NIHVA TECHNOLOGIES PVT. LTD, PUNE
Tel : 020 66304033
Email:- info@nihva.com
Website:- www.nihva.com

CLIENT -

PROJECT -

SITE LOCATION -

DWG. NO. :NIHVA/19-20/VDR/192 | REV- R00

SCALE: NTS | WT: | SHEET: 01 OF 01