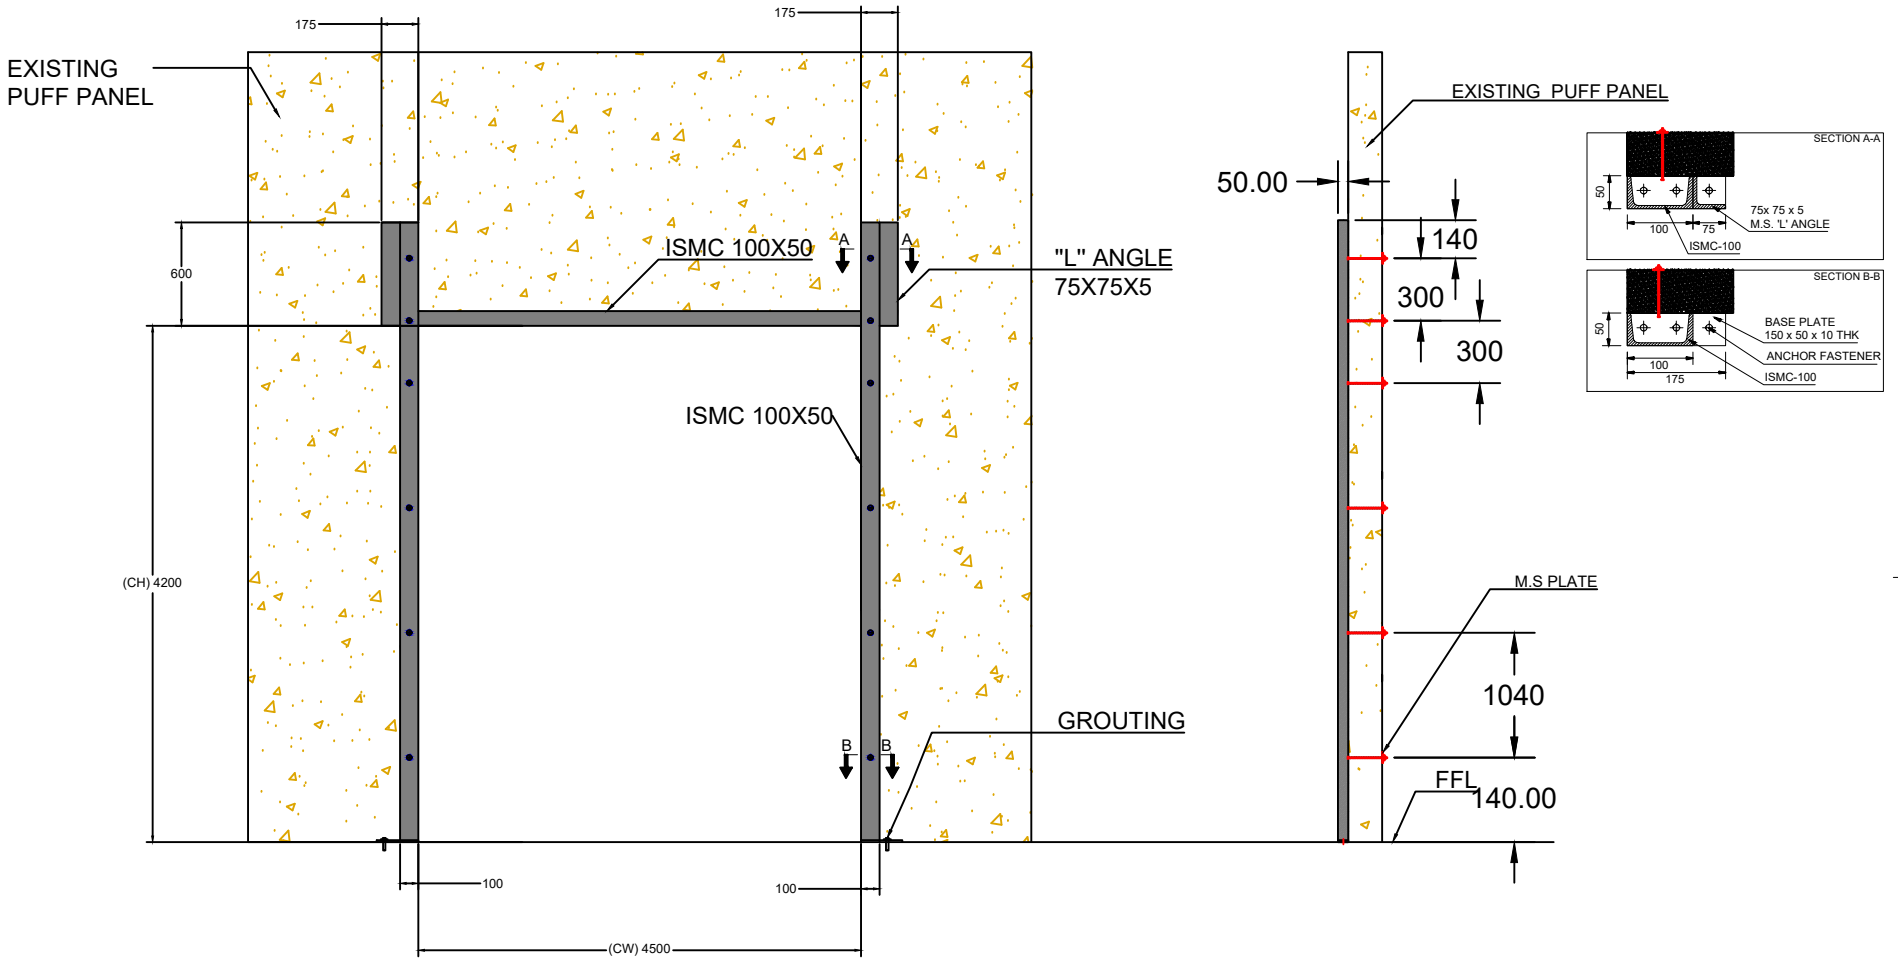



M.S. STRUCTURE DETAILS

| Sr | Description | Clear Width (CW) | Clear Height (CH) | QTY |
|---|---|---|---|---|
| 1 | HSD Without Sensor | **4500** | **4200** | 5 |

This drawing & design is the property of NIHVA TECHNOLOGIES. Not to be sold or copied to any other concern.

| TITLE | HIGH SPEED DOOR STRUCTURE DRAWING | | | NIHVA TECHNOLOGIES PVT. LTD. PUNE<br>Tel : 020 66304033<br>Email:- info@nihva.com<br>Website:- www.nihva.com |
|---|---|---|---|---|
| | NAME | SIGN | DATE | |
| DRAWN | S.J | | 18.01.2024 | CLIENT - RINAC |
| CHECK | A.K | | 18.01.2024 | PROJECT - HIGH SPEED DOOR ST. |
| APPRD. | V.T | | 18.01.2024 | FORMAT NO - NIHVA-DD-F-03 |
| If any queries contact : projectsupport@nihva.com | | | | DWG. NO. : NIHVA/23-24/00XX / REV- R00 |
| ALL DIMENSION ARE IN mm | | | | SCALE: NTS / WT: / SHEET: |