




ELEVATION

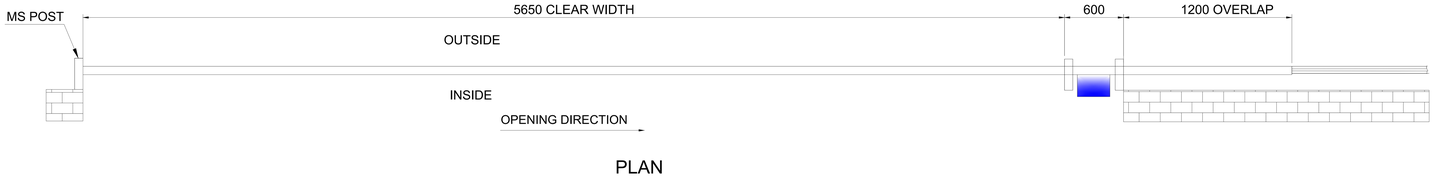

PLAN

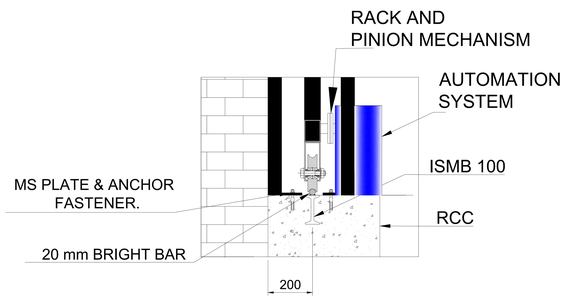

DETAIL VIEW OF A

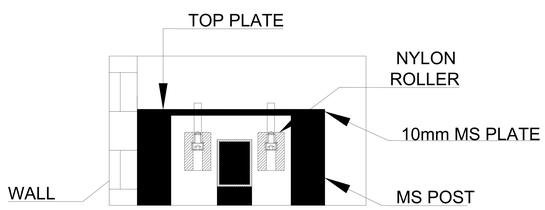

DETAIL VIEW OF B

REV NO	REV DATE	DRAWN	REMARK
03	31.07.2019	P.V.A	1. CLEAR WIDTH CHANGE
02	12.07.2019	P.V.A	1. GATE DESIGN CHANGE.
01	12.07.2019	P.V.A	1. PERFORATED SHEET ADDED

SR.NO	RAL CODE	RAL COLOR
01	RAL 9002	GREY WHITE

DIMENSION :

CLEAR WIDTH	CLEAR HEIGHT	QUANTITY
6250 mm	2100mm	1 NO

MATERIAL: MS

THICKNESS :

NOTE-
1. ALL REQUIRED CIVIL WORK WILL BE IN CLIENTS SCOPE.
2.IN NECESSARY GATE LEAF WILL BE IN TWO PARTS FOR TRANSPORTATION AND WILL BE WELDED TOGETHER ON SITE.

TOLERANCE:- ± 05mm

NIHVA
NIHVA TECHNOLOGIES PVT. LTD.
Website:- www.nihva.com
NIHVA TECHNOLOGIES PVT. LTD. PUNE
Email:- info@nihva.com
TEL :020 66304033

TITLE:

AUTOMATIC SINGLE LEAF SLIDING GATE

CLIENT'S APPROVAL :

CLIENT - OC SPECILITIES PVT LTD

PROJECT -

SITE LOCATION -

DWG. NO. : NIHVA/19-20/0049/R03 | REV. : R03

SCALE: NTS | WT: | SHEET:1 OF 1

DRAWN	P.V.A		12.07.2019
CHECK	V.M.T		12.07.2019
APPROVED			

IF ANY QUERIES CONTACT:- design@nihva.com

NOTE: ALL DIMENSIONS ARE IN mm

THIS DRAWING & DESIGN IS THE PROPERTY OF NIHVA TECHNOLOGIES. NOT TO BE SOLD OR COPIED TO ANY OTHER CONCERN.