

PRODUCED BY AN AUTODESK EDUCATIONAL PRODUCT


PRODUCED BY AN AUTODESK EDUCATIONAL PRODUCT

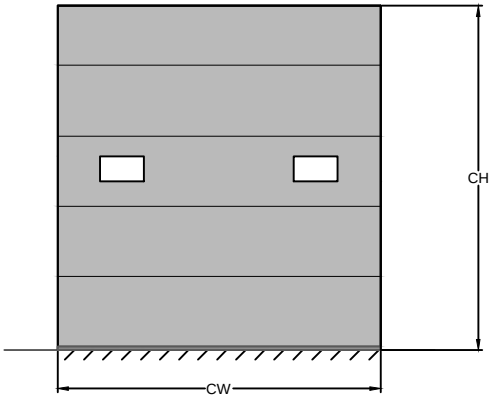


OUTSIDE ELEVATION

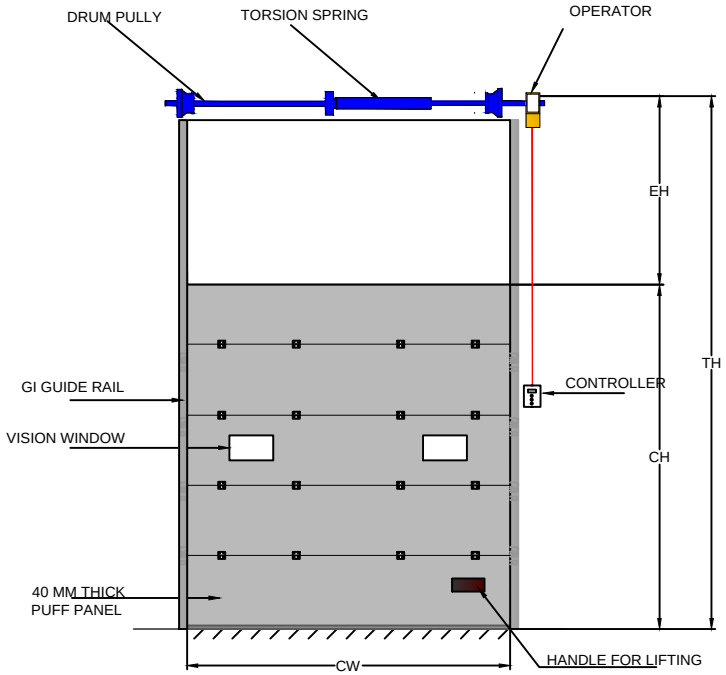


INSIDE ELEVATION

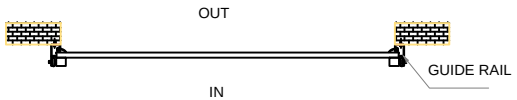

PLAN

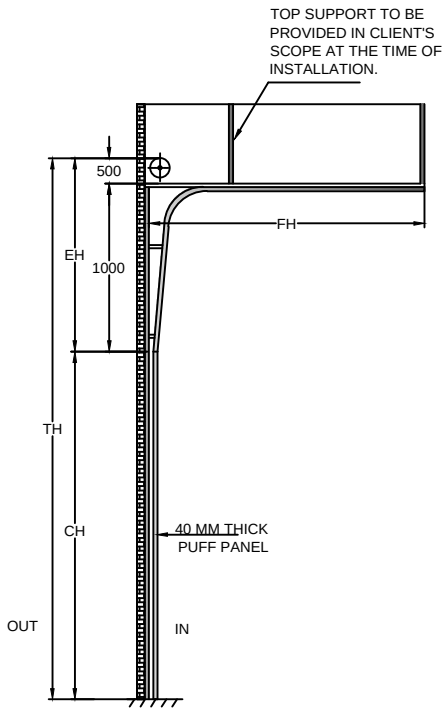

SIDE VIEW

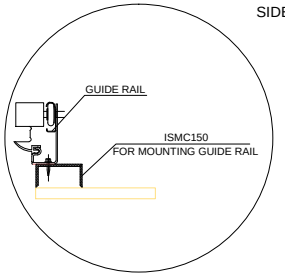

SR NO	CLEAR WIDTH (CW)	CLEAR HEIGHT (CH)	QUANTITY	EH	FH	TH
1	2400	3000	1	1500	2800	4500

NOTE- 1. STRUCTURE REQUIRED FOR SECTIONAL DOOR SHALL BE IN CLIENT'S SCOPE.
2. COLOR FOR SECTIONAL DOOR PANEL WOULD BE AS PER CLIENT APPROVED RAL CODE.

TOLERANCE: 10mm

This drawing & design is the property of NIHVA TECHNOLOGIES. Not to be sold or copied to any other concern.

TITLE: SECTIONAL DOOR (HL) STRUCTURE

NIHVA TECHNOLOGIES PVT. LTD.
NIHVA TECHNOLOGIES PVT. LTD. PUNE
Tel : 020 66304033
Email:- info@nihva.com
Website:- www.nihva.com

	NAME	SIGN	DATE
DRAWN	P.A		25.06.20
CHECK	G.J		25.06.20
APPROVAL			

CLIENT - RMK INFRASTRUCTURE
PROJECT -
SITE -
If any queries contact : design@nihva.com
DWG. NO. : NIHVA/20-21/0028
REV: R00
ALL DIMENSION ARE IN mm
SCALE: NTS
WT:
SHEET: 01 OF 01

PRODUCED BY AN AUTODESK EDUCATIONAL PRODUCT