


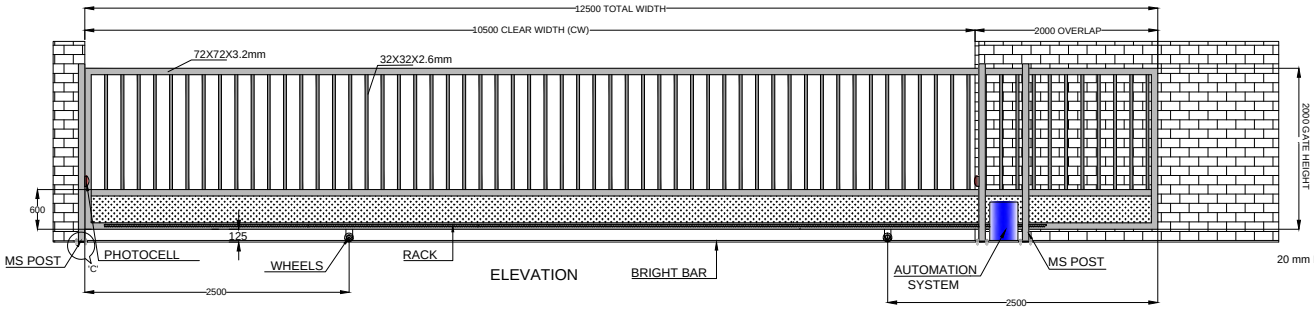


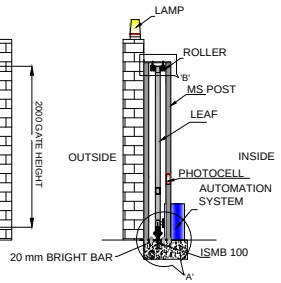


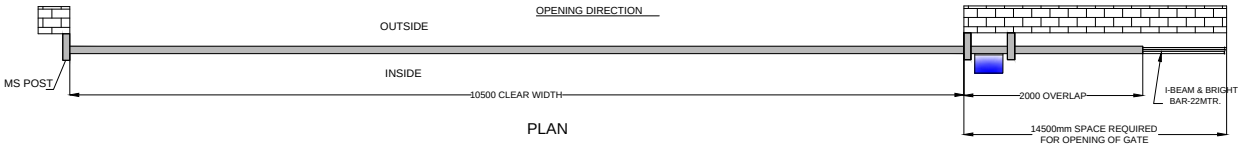


PLAN

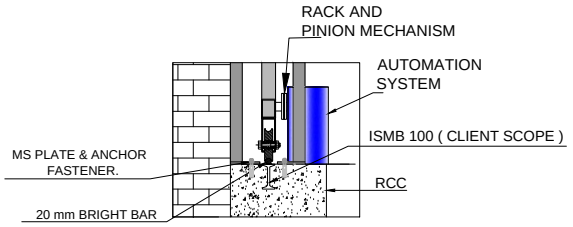

DETAIL VIEW OF A

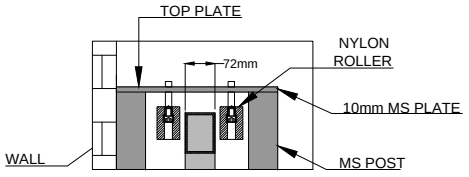

DETAIL VIEW OF B

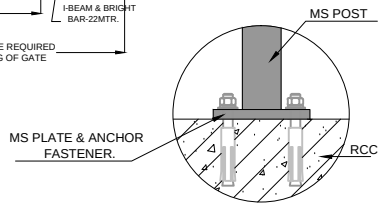

DETAIL VIEW OF C
(FIXING DETAILS)

SR NO	TUBE SPECIFICATION	
1	72X72X3.2mm MS TUBE	OUTER FRAME
2	32X32X2mm MS TUBE	INNER PATTERN
3	GAP BETWEEN TUBES	150mm
4	MS SHEET	MS SHEET
5	72X72X3.2mm MS TUBE	FOR POST

SR.NO	RAL CODE	RAL COLOR
04	RAL 7035	LIGHT GREY
03	RAL 5002	ULTRAMARINE BLUE
02	RAL 9002	GREY WHITE
01	RAL 1004	GOLDEN YELLOW

TOLERANCE:- ± 10mm

CLEAR WIDTH (CW)	CLEAR HEIGHT (CH)	QUANTITY
10500mm	2000mm	1 NO

DIMENSION :

CLEAR WIDTH	CLEAR HEIGHT	QUANTITY
10500mm	2000mm	1 NO

MATERIAL: MS

THICKNESS :

NOTE-
1. ALL REQUIRED CIVIL WORK WILL BE IN CLIENTS SCOPE.
2.ONE COAT OF RED OXIDE & TWO COAT OF APPROVED RAL SHADE WILL BW GIVEN TO THE GATE
3.IN NECESSARY GATE LEAF WILL BE IN TWO PART FOR TRANSPORTATION AND ILL BE WELDED TOGETHER ON SITE

NIHVA
NIHVA TECHNOLOGIES PVT. LTD.
Website:- www.nihva.com
NIHVA TECHNOLOGIES PVT. LTD. PUNE
Email:- info@nihva.com
TEL :020 66304033

TITLE:

AUTOMATIC SINGLE LEAF SLIDING GATE

CLIENT'S APPROVAL :

CLIENT - SCON PROJECT.

PROJECT - COCA COLA

SITE LOCATION -GOA.

DWG. NO. : NIHVA/18-19/0273	REV. : 00
SCALE: NTS	WT: SHEET:1 OF 1

DRAWN	P.V.A		DATE: 16.02.19
CHECK	V.M.T		DATE: 16.02.19
APPROVED			

IF ANY QUERIES CONTACT:- design@nihva.com

NOTE: ALL DIMENSIONS ARE IN mm

THIS DRAWING & DESIGN IS THE PROPERTY OF NIHVA TECHNOLOGIES. NOT TO BE SOLD OR COPIED TO ANY OTHER CONCERN.