

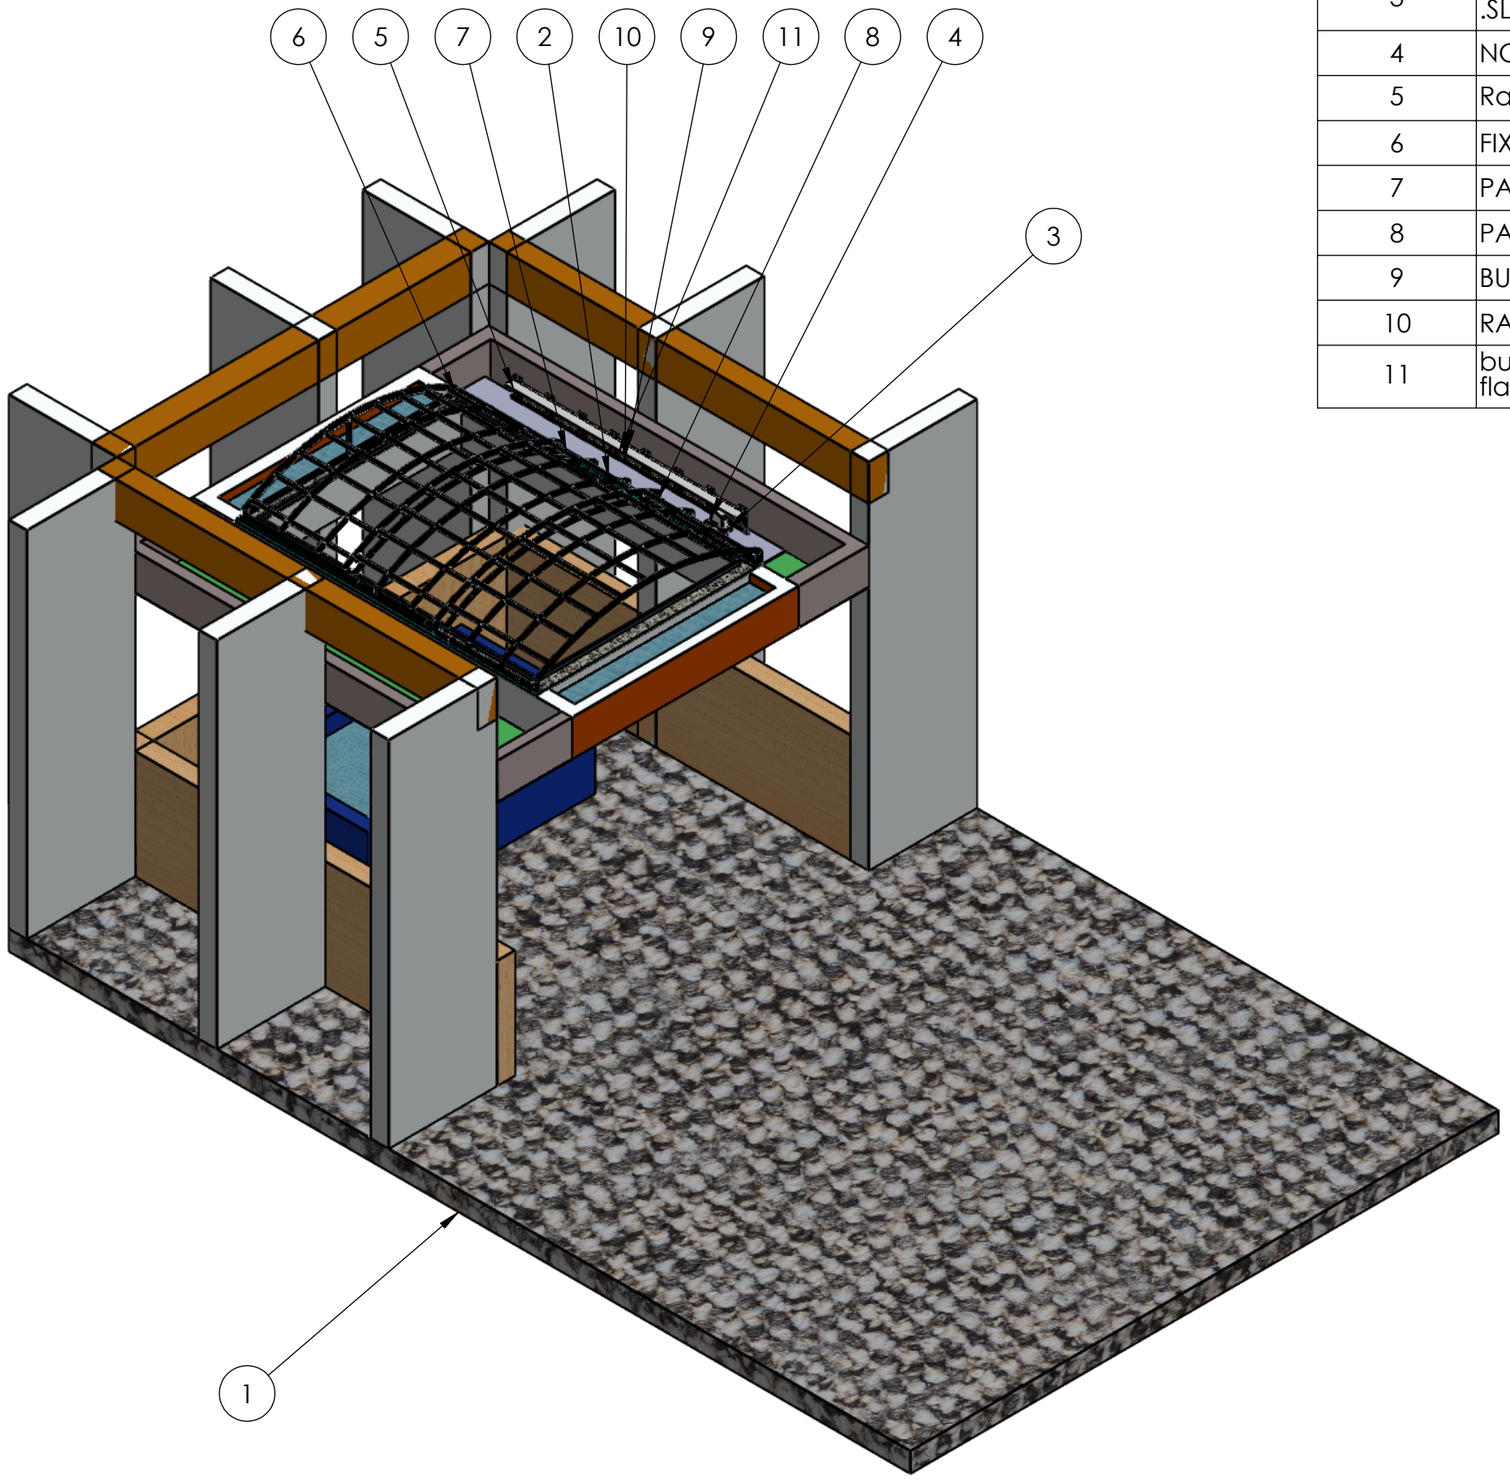



ITEM NO.	PART NUMBER	DESCRIPTION	QTY.
1	new BASE CIVIL	CLIENT SCOPE	1
2	GUIDE RAILS-T89-1B_NTPL236	STD	4
3	Motor mtg bracket .SLDDRW	OUTSOURCE (STD LOOSE PART)	1
4	NCE_RUN_1800KG	STD	1
5	Rack support_01	OUTSOURCE (STD LOOSE PART)	8
6	FIX PANEL_01	INHOUSE	1
7	PANEL_02	INHOUSE	1
8	PANEL_03	INHOUSE	1
9	BUSBAR_NTPL236	STD	1
10	RACK_NTPL236	STD	1
11	busbar flashing_NTPL236	OUTSOURCE	1

CLIENT:- DR. PALAVE NAGAR				NIHVA TECHNOLOGIES PVT.LTD.PUNE Website - www.nihva.com	
	NAME	SIGN	DATE	TITLE :- RETRACTABLE SLIDING ROOF ASM	
DRAWN	S.W		13.07.2024	MATERIAL:-	TREATMENT:-
CHK'D	P.M.		13.07.2024	PROJECT CODE: - PRJ 24-25 NTPL_236	
APPV'D	V.T.		13.07.2024	DRAWING NO: - PRJ 24-25 NTPL_236-0100-00-000	
if any queries contact - supportautomation@nihva.com				PROJECT NAME - RETRACTABLE SLIDING ROOF	
ALL DIMENSION ARE IN mm	A3			SCALE - 1.1	QTY:- SHEET 1 OF 19

ITEM NO.	PART NUMBER	DESCRIPTION	QTY.
1	ENCLOUSER ASM FIX PANEL	GNT_006	1
2	P1.4	GNT_006	2
3	PF_1.1	GNT_006	1
4	PF_1.2	GNT_006	2
5	SQ TUBE 50X50X1.5 MM L-960		27

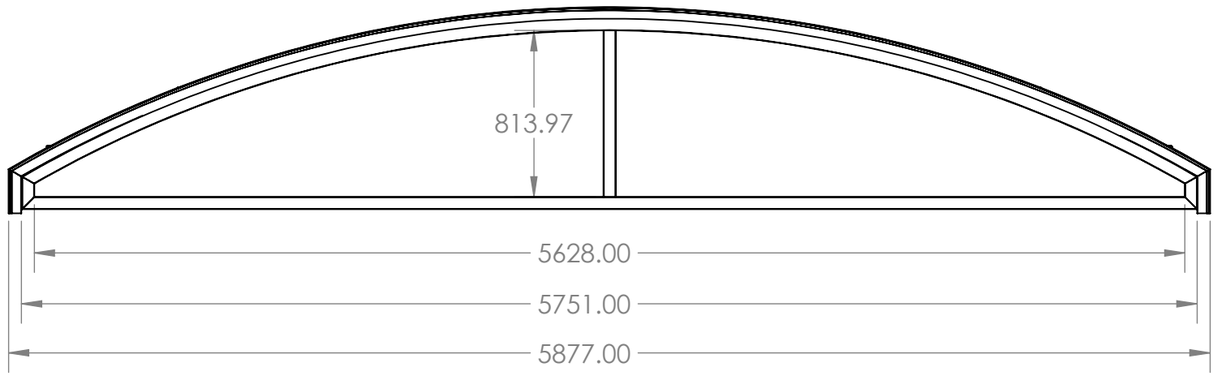


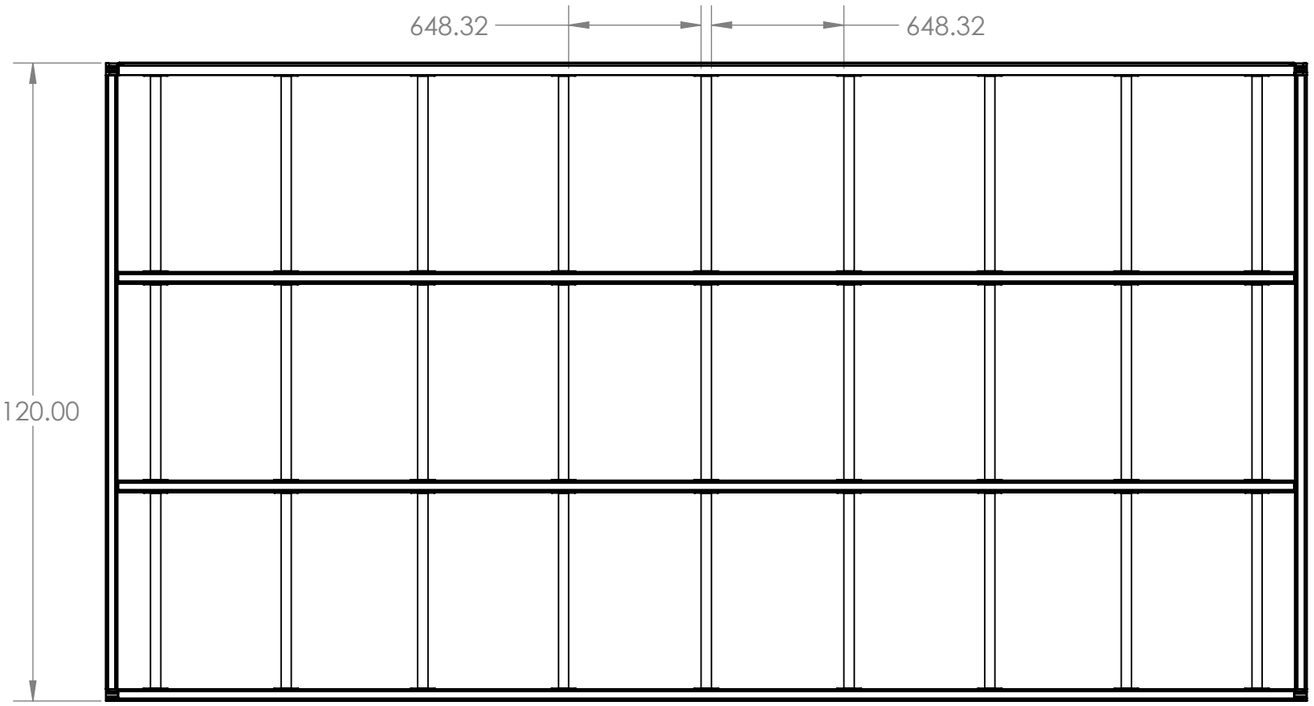


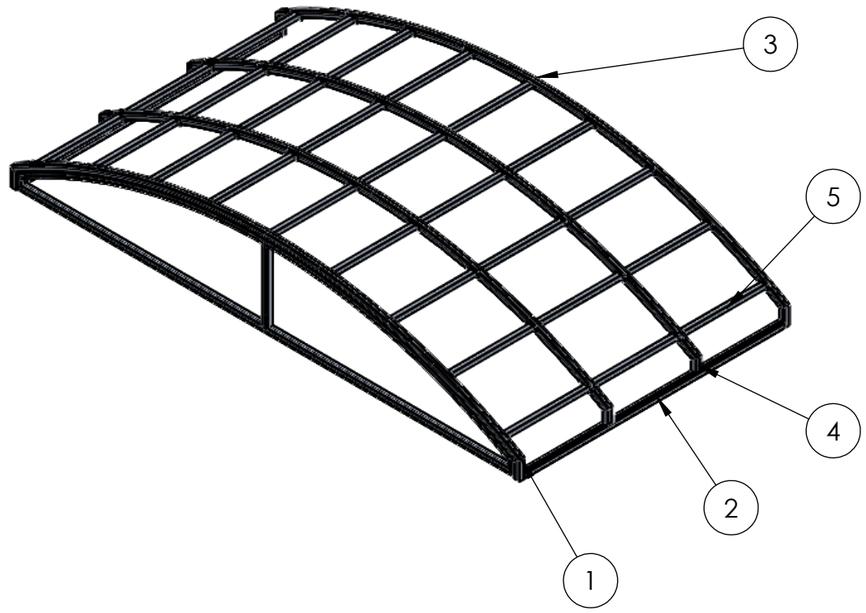


CLIENT:-	DR. PALAVE NAGAR			NIHVA TECHNOLOGIES PVT.LTD.PUNE Website - www.nihva.com	
	NAME	SIGN	DATE	TITLE :- FIX PANEL _01 ASM	
DRAWN	S.W		13.07.2024	MATERIAL:-	TREATMENT:-
CHK'D	P.M.		13.07.2024	PROJECT CODE: - PRJ 24-25 NTPL_236	
APPV'D	V.T.		13.07.2024	DRAWING NO: - PRJ-24-25 NTPL_236-0101-00-000	
if any queries contact - supportautomation@nihva.com				PROJECT NAME - RETRACTABLE SLIDING ROOF	
ALL DIMENSION ARE IN mm	A3			SCALE - 1.1 QTY:-	SHEET 2 OF 19

ITEM NO.	PART NUMBER	DESCRIPTION	QTY.
1	PF_1.1	GNT_006	1
2	PF_1.3 (ENCLOUSER)	GNT_006	1

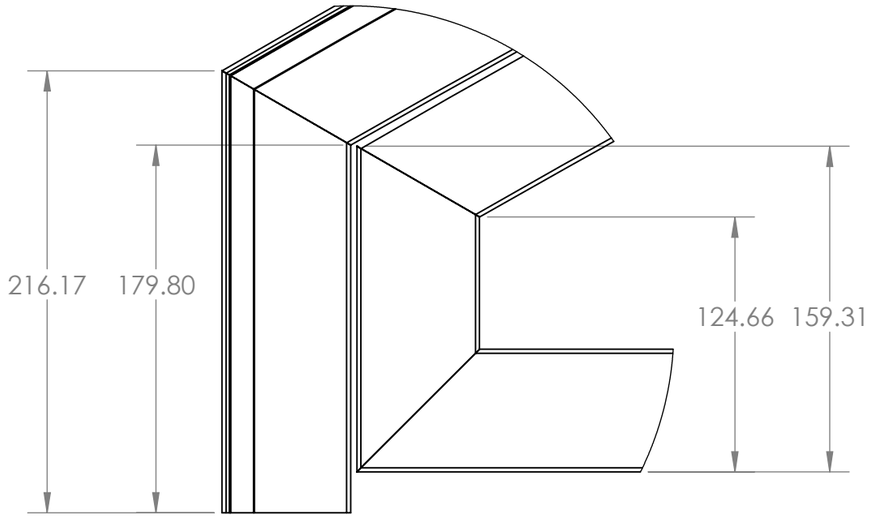

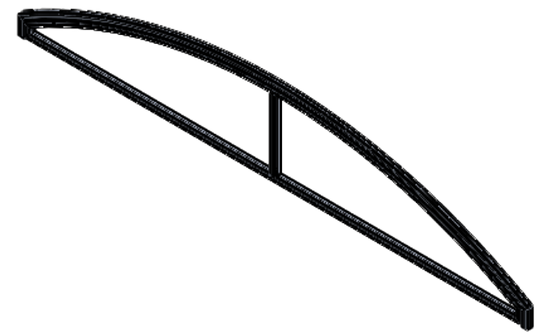


DETAIL D
SCALE 1 : 3

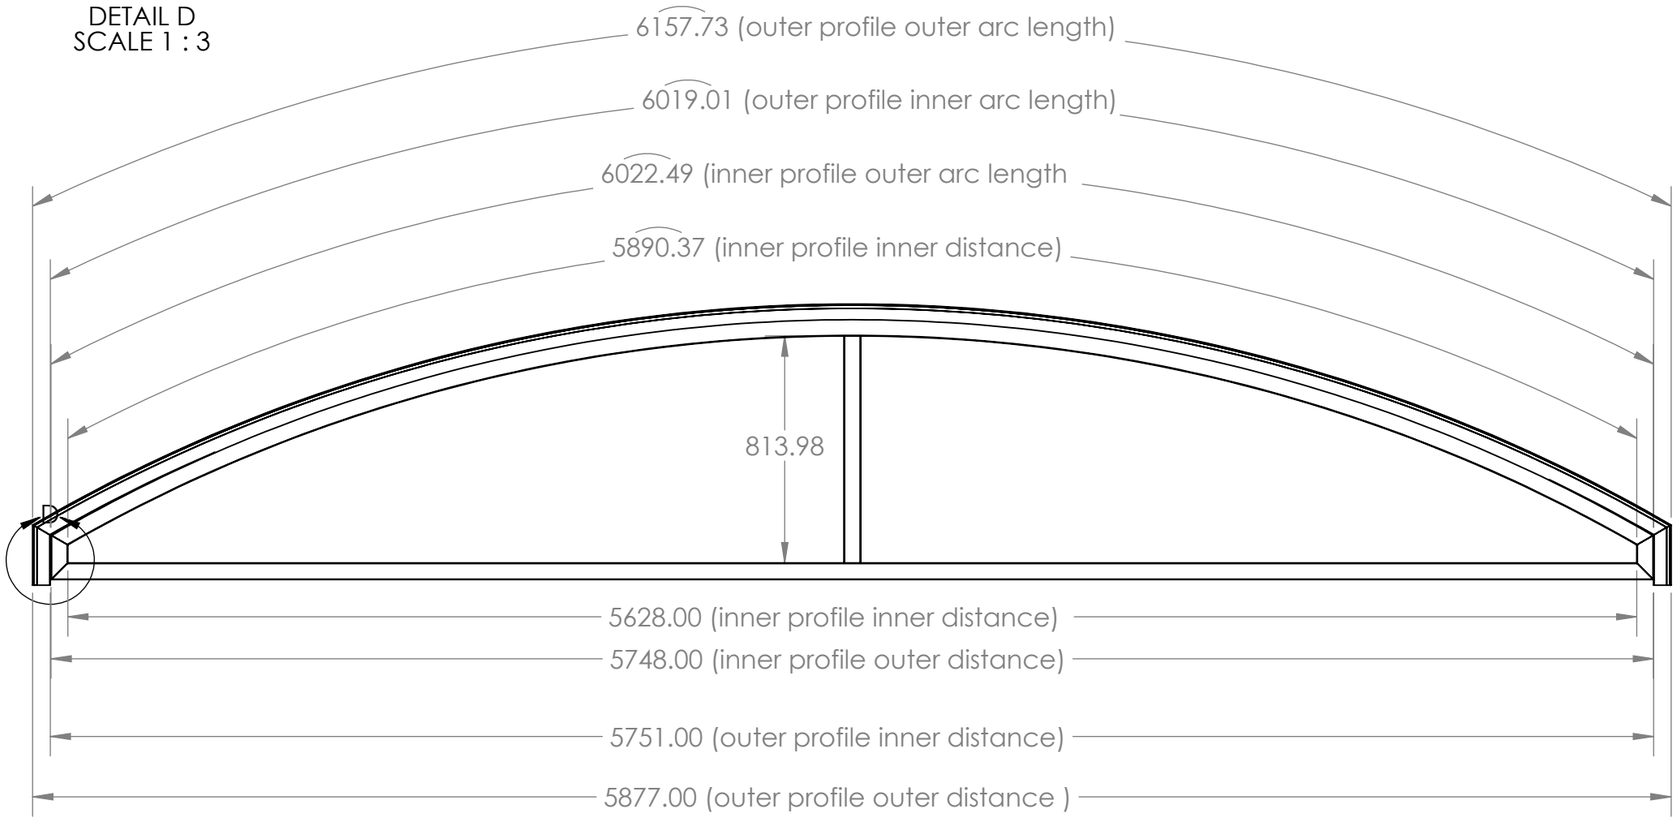

CLIENT:- **DR. PALAVE NAGAR**				NIHVA TECHNOLOGIES PVT.LTD.PUNE Website - www.nihva.com	
	NAME	SIGN	DATE	TITLE :- FIX PANEL ENCLOUSER ASM	
DRAWN	S.W		13.07.2024	MATERIAL:- AL GNT_006	TREATMENT:- POWDER COATING
CHK'D	P.M.		13.07.2024	PROJECT CODE: - PRJ 24-25 NTPL_236	
APPV'D	V.T.		13.07.2024	DRAWING NO: - PRJ 24-25 NTPL_236-0101-01-000	
if any queries contact - supportautomation@nihva.com				PROJECT NAME - RETRACTABLE SLIDING ROOF	
ALL DIMENSION ARE IN mm	A3			SCALE - 1.1 QTY:-	SHEET 3 OF 19


ITEM NO.	PART NUMBER	DESCRIPTION	QTY.
1	P1.4	GNT_006	2



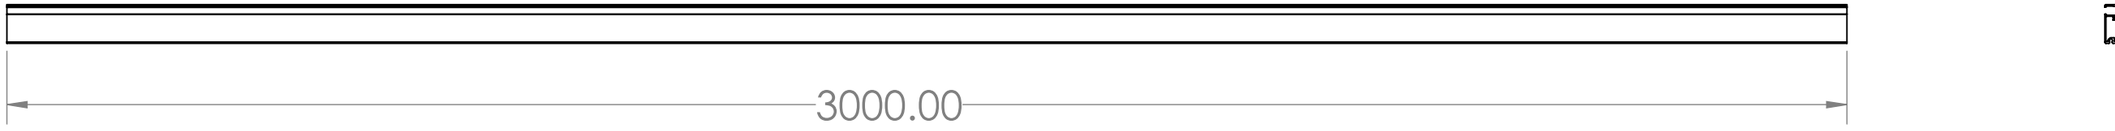


CLIENT:- **DR. PALAVE NAGAR**				NIHVA Technologies Pvt. Ltd	NIHVA TECHNOLOGIES PVT.LTD.PUNE Website - www.nihva.com
	NAME	SIGN	DATE	TITLE :- FIX PANEL ENCLOUSER ASM _P1.4	
DRAWN	S.W		13.07.2024	MATERIAL:- AL GNT_006	TREATMENT:- POWDER COATING
CHK'D	P.M.		13.07.2024	PROJECT CODE: - PRJ 24-25 NTPL_236	
APPV'D	V.T.		13.07.2024	DRAWING NO: - PRJ 24-25 NTPL_236-0101-01-000	
if any queries contact - supportautomation@nihva.com				PROJECT NAME - RETRACTABLE SLIDING ROOF	
ALL DIMENSION ARE IN mm	A3			SCALE - 1.1 QTY:-	SHEET 4 OF 19

ITEM NO.	PART NUMBER	DESCRIPTION	QTY.
1	PF_1.1	GNT_006	1

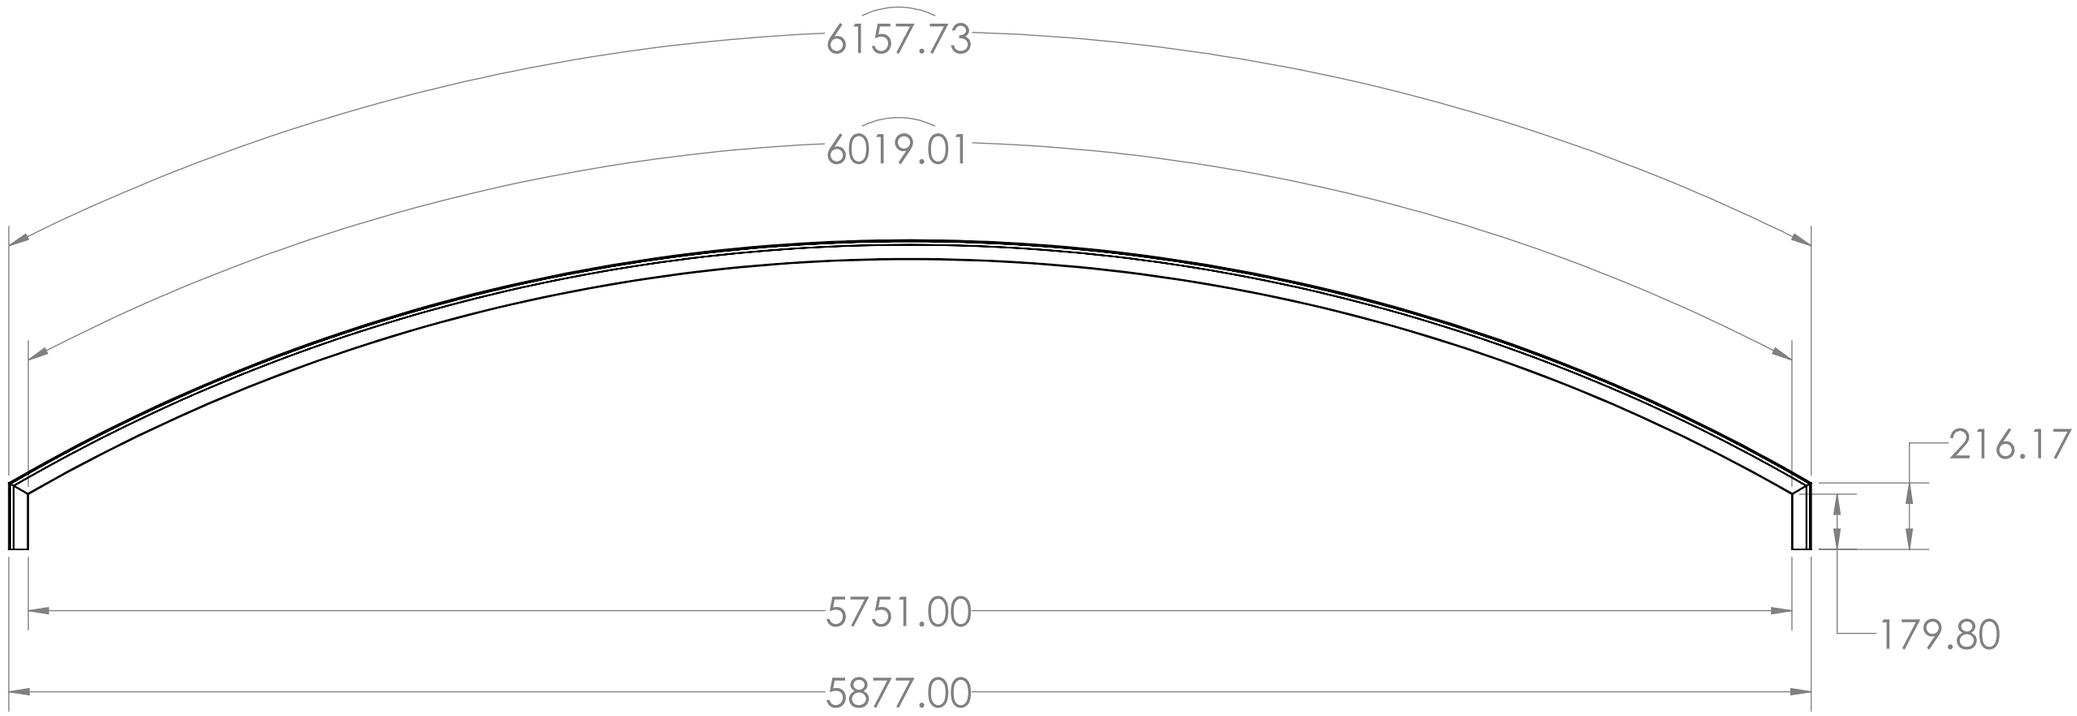


CLIENT:- DR. PALAVE NAGAR				NIHVA TECHNOLOGIES PVT.LTD.PUNE Website - www.nihva.com	
	NAME	SIGN	DATE	TITLE :- FIX PANEL ENCLOUSER ASM -PF_1.1	
DRAWN	S.W		13.07.2024	MATERIAL:- AL GNT_006	TREATMENT:- POWDER COATING
CHK'D	P.M.		13.07.2024	PROJECT CODE: - PRJ 24-25 NTPL_236	
APPV'D	V.T.		13.07.2024	DRAWING NO: - PRJ 24-25 NTPL_236-0101-01-002	
if any queries contact - supportautomation@nihva.com				PROJECT NAME - RETRACTABLE SLIDING ROOF	
ALL DIMENSION ARE IN mm	A3			SCALE - 1.1 QTY:-	SHEET 5 OF 19


ITEM NO.	PART NUMBER	DESCRIPTION	QTY.
1	PF_1.2	GNT_006	1

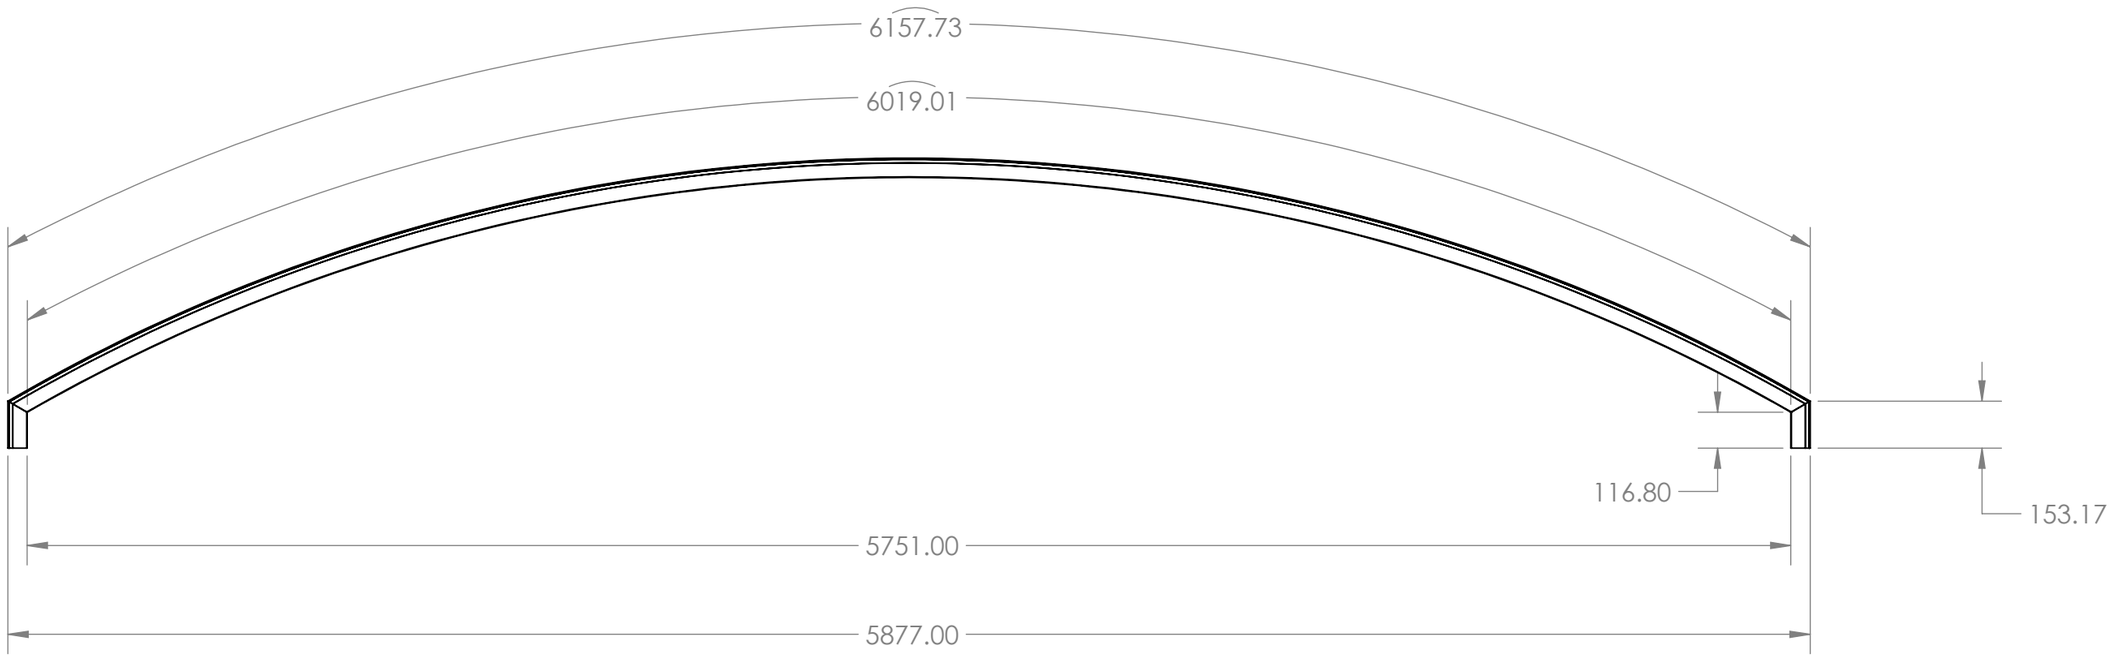


CLIENT:- DR. PALAVE NAGAR				NIHVA TECHNOLOGIES PVT.LTD.PUNE Website - www.nihva.com	
	NAME	SIGN	DATE	TITLE :- FIX PANEL ENCLOUSER ASM-PF_1.2	
DRAWN	S.W		13.07.2024	MATERIAL:- AL GNT_006	TREATMENT:- POWDER COATING
CHK'D	P.M.		13.07.2024	PROJECT CODE: - PRJ 24-25 NTPL_236	
APPV'D	V.T.		13.07.2024	DRAWING NO: - PRJ 24-25 NTPL_236-0101-01-003	
if any queries contact - supportautomation@nihva.com				PROJECT NAME - RETRACTABLE SLIDING ROOF	
ALL DIMENSION ARE IN mm	A3			SCALE - 1.1 QTY:-	SHEET 6 OF 19

ITEM NO.	PART NUMBER	DESCRIPTION	QTY.
1	SQ TUBE 50X50X1.5 MM L-960		27

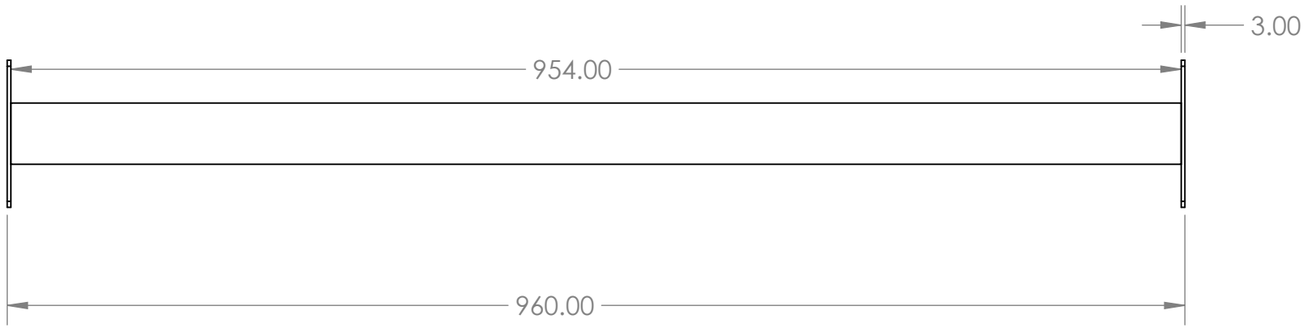


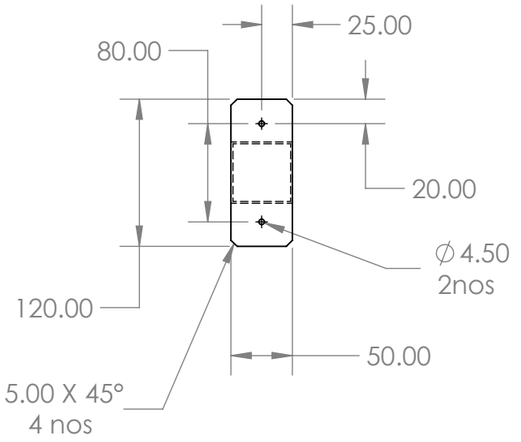


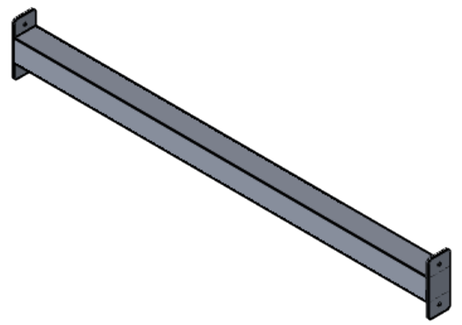


CLIENT:- DR. PALAVE NAGAR				NIHVA TECHNOLOGIES PVT.LTD.PUNE Website - www.nihva.com
	NAME	SIGN	DATE	TITLE :- FIX PANEL ENCLOUSER ASM - SUPPORT SQ TUBE
DRAWN	S.W		13.07.2024	MATERIAL:- MS / TREATMENT:- POWDER COATING
CHK'D	P.M.		13.07.2024	PROJECT CODE: - PRJ 24-25 NTPL_236
APPV'D	V.T.		13.07.2024	DRAWING NO: - PRJ 24-25 NTPL_236-0101-01-004
if any queries contact - supportautomation@nihva.com				PROJECT NAME - RETRACTABLE SLIDING ROOF
ALL DIMENSION ARE IN mm	A3			SCALE - 1.1 QTY:- / SHEET 7 OF 19

ITEM NO.	PART NUMBER	DESCRIPTION	QTY.
1	P2.1	GNT_006	2
2	P3.2	GNT_006	2
3	P2.2	GNT_006	2
4	SQ TUBE 50X50X1.5 MM L-875	INHOUSE +STD	27
5	lift track assembely block	MACHINING PART	8

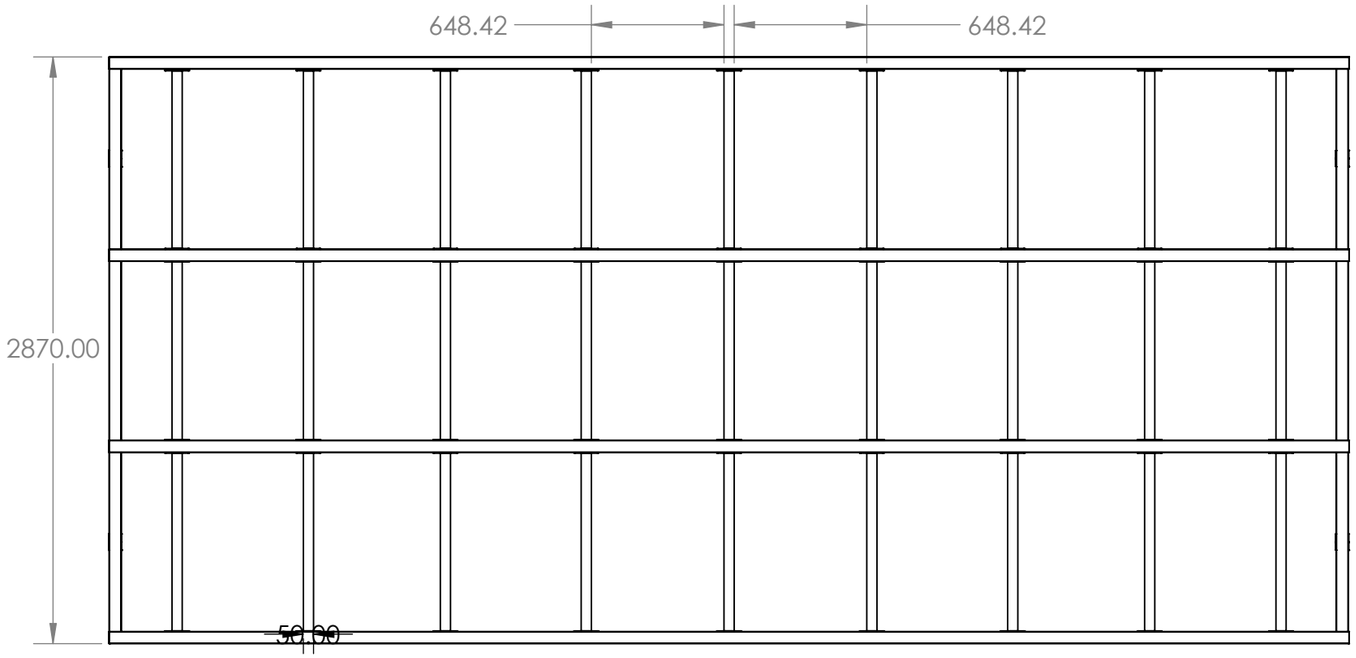


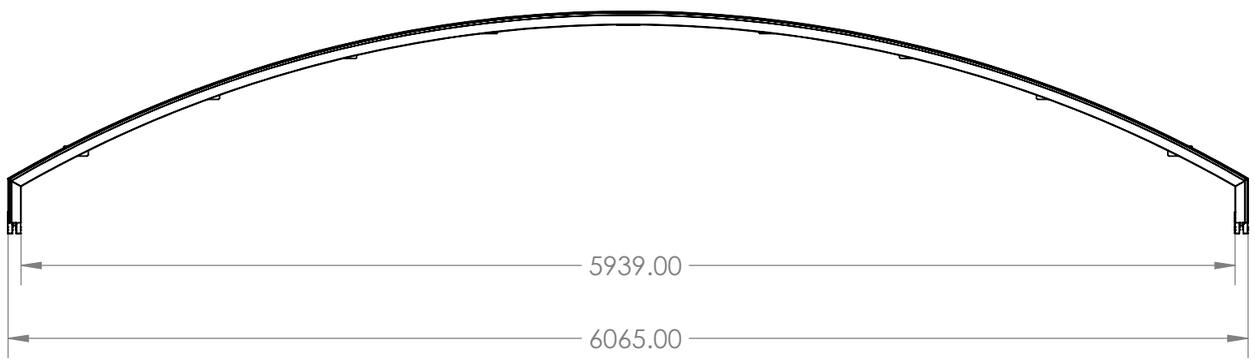


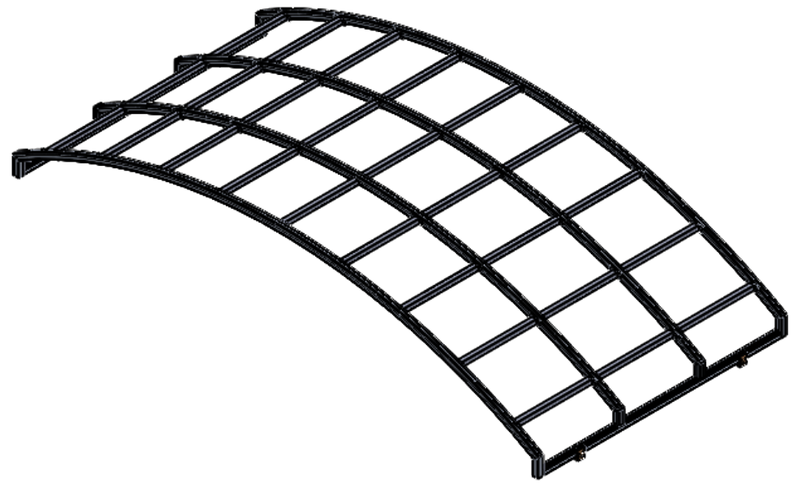

CLIENT:- **DR. PALAVE NAGAR**				NIHVA TECHNOLOGIES PVT.LTD.PUNE Website - www.nihva.com	
	NAME	SIGN	DATE	TITLE :- PANEL_02	
DRAWN	S.W		13.07.2024	MATERIAL:- AL GNT_006	TREATMENT:- POWDER COATING
CHK'D	P.M.		13.07.2024	PROJECT CODE: - PRJ 24-25 NTPL_236	
APPV'D	V.T.		13.07.2024	DRAWING NO: - PRJ 24-25 NTPL_236-0101-02-000	
if any queries contact - supportautomation@nihva.com				PROJECT NAME - RETRACTABLE SLIDING ROOF	
ALL DIMENSION ARE IN mm	A3			SCALE - 1.1 QTY:-	SHEET 8 OF 19


ITEM NO.	PART NUMBER	DESCRIPTION	QTY.
1	P2.1	GNT_006	2

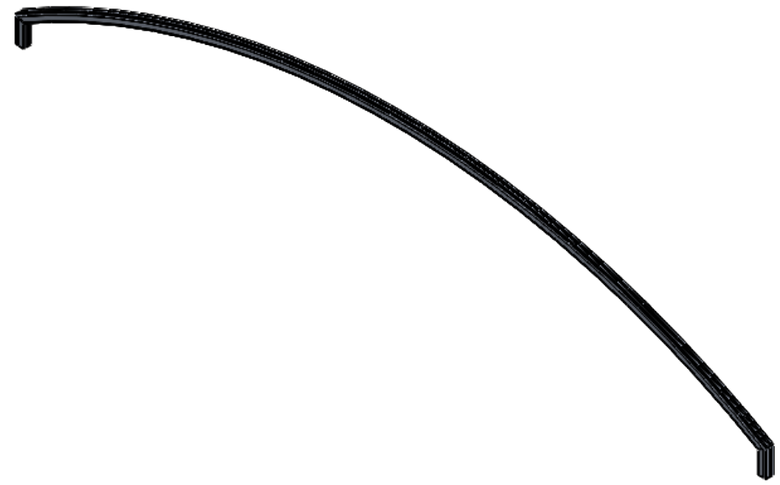

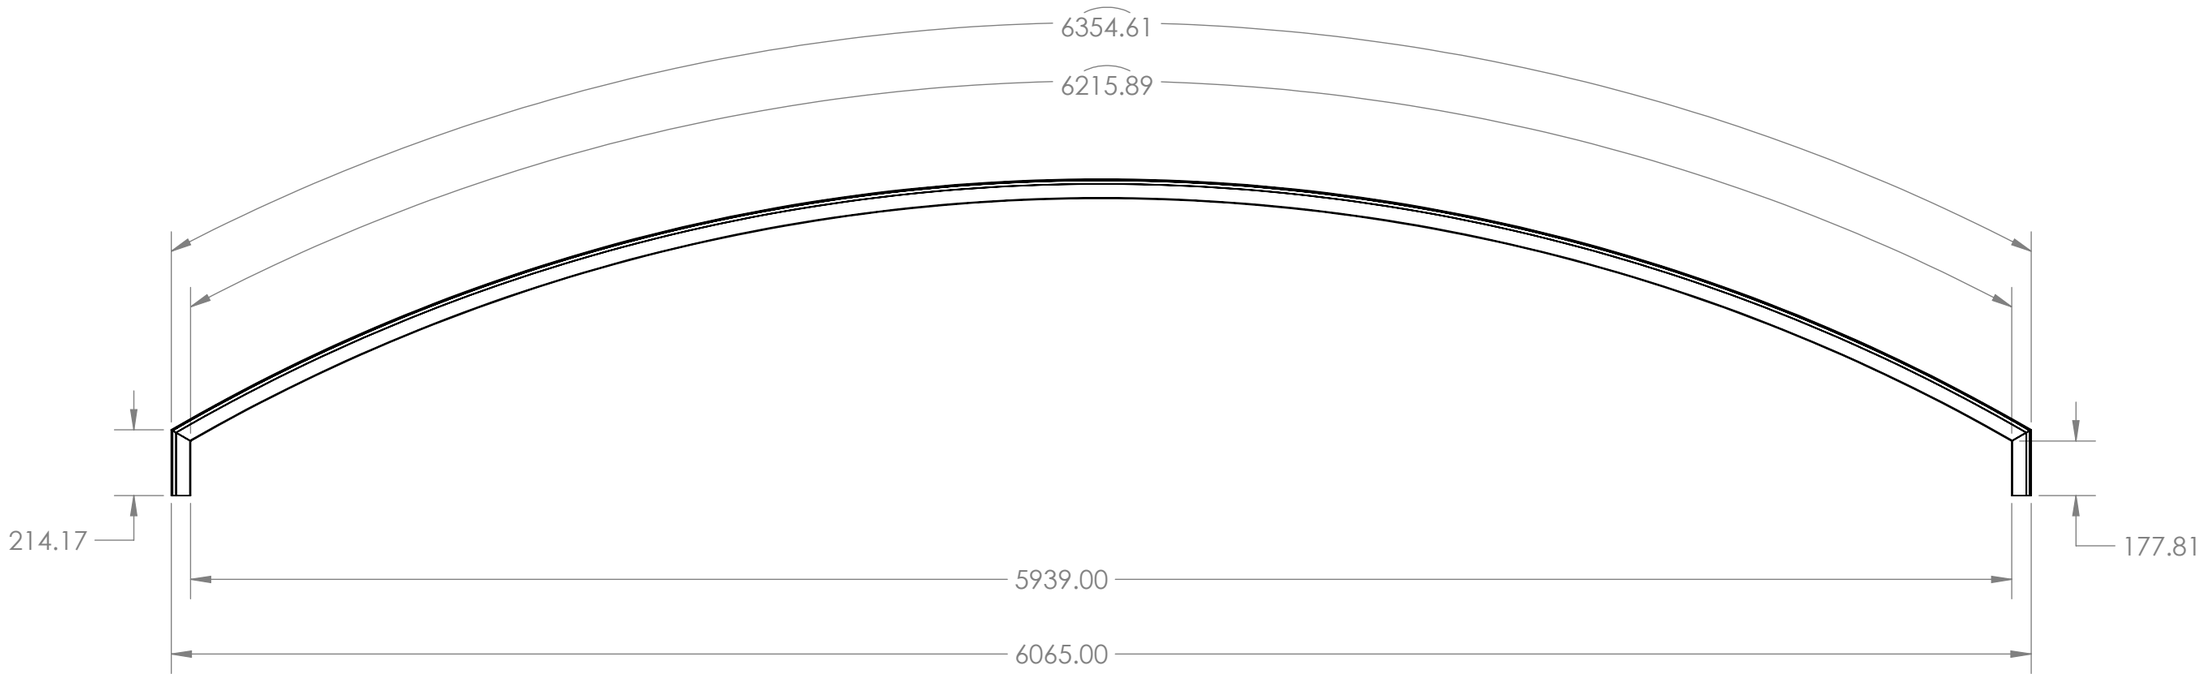

CLIENT:- **DR. PALAVE NAGAR**				NIHVA TECHNOLOGIES PVT.LTD.PUNE Website - www.nihva.com	
	NAME	SIGN	DATE	TITLE :- PANEL_02-P2.1	
DRAWN	S.W		13.07.2024	MATERIAL:- AL GNT_006	TREATMENT:- POWDER COATING
CHK'D	P.M.		13.07.2024	PROJECT CODE: - PRJ 24-25 NTPL_236	
APPV'D	V.T.		13.07.2024	DRAWING NO: - PRJ 24-25 NTPL_236-0101-02-001	
if any queries contact - supportautomation@nihva.com				PROJECT NAME - RETRACTABLE SLIDING ROOF	
ALL DIMENSION ARE IN mm		A3		SCALE - 1.1 QTY:-	SHEET 9 OF 19


ITEM NO.	PART NUMBER	DESCRIPTION	QTY.
1	P3.2	GNT_006	4

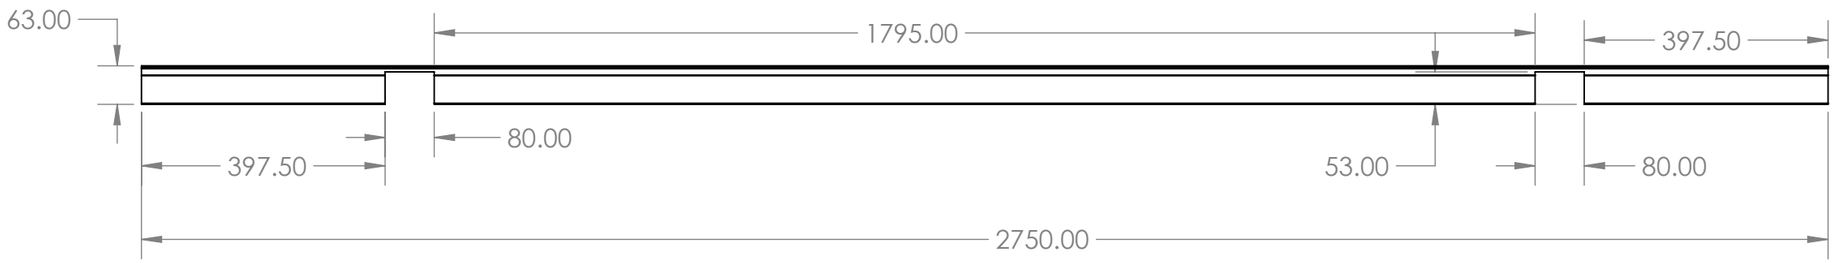




CLIENT:- **DR. PALAVE NAGAR**				NIHVA Technologies Pvt. Ltd	NIHVA TECHNOLOGIES PVT.LTD.PUNE Website - www.nihva.com
	NAME	SIGN	DATE	TITLE :- PANEL_02-P3.2	
DRAWN	S.W		13.07.2024	MATERIAL:- AL GNT_006	TREATMENT:- POWDER COATING
CHK'D	P.M.		13.07.2024	PROJECT CODE: - PRJ 24-25 NTPL_236	
APPV'D	V.T.		13.07.2024	DRAWING NO: - PRJ 24-25 NTPL_236-0101-02-002	
if any queries contact - supportautomation@nihva.com				PROJECT NAME - RETRACTABLE SLIDING ROOF	
ALL DIMENSION ARE IN mm	A3			SCALE - 1.1 QTY:-	SHEET 10 OF 19


ITEM NO.	PART NUMBER	DESCRIPTION	QTY.
1	P2.2	GNT_006	2

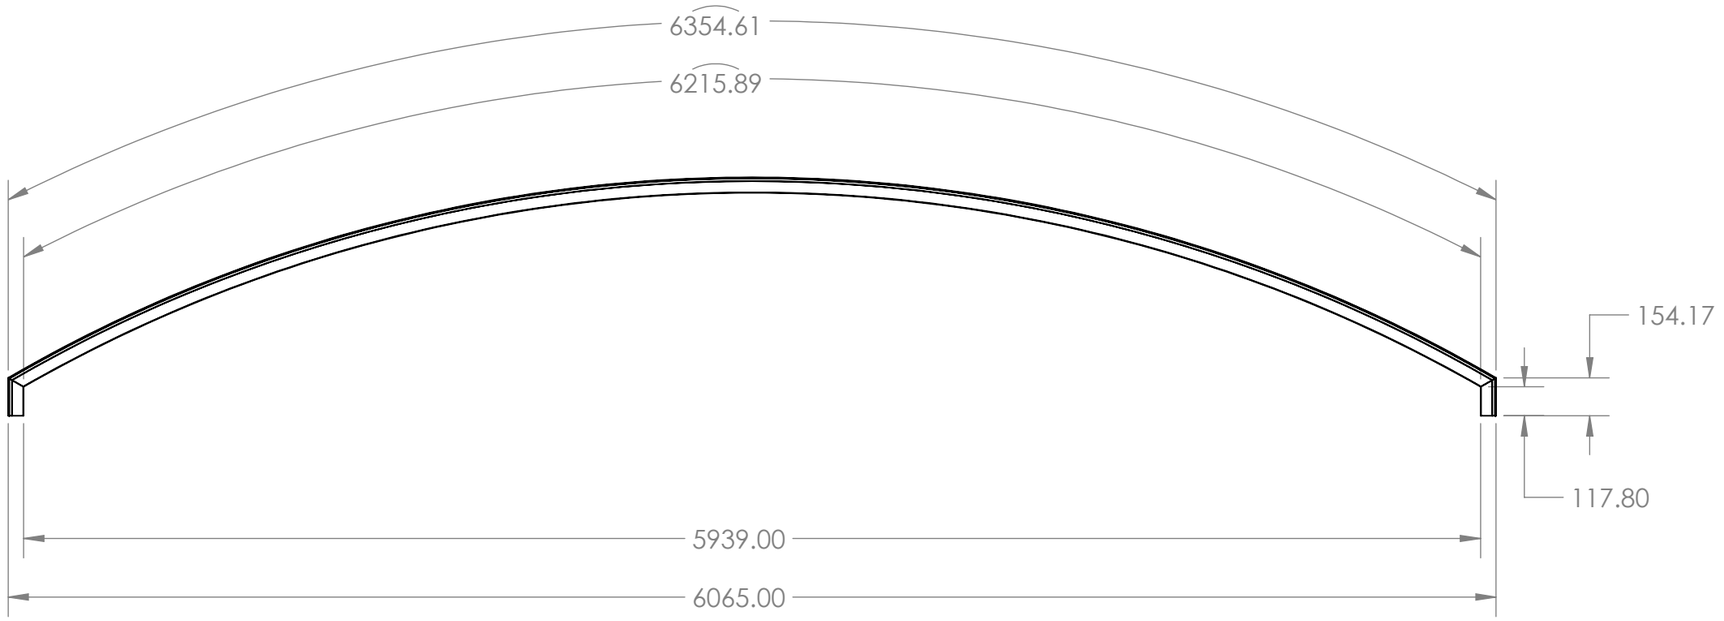


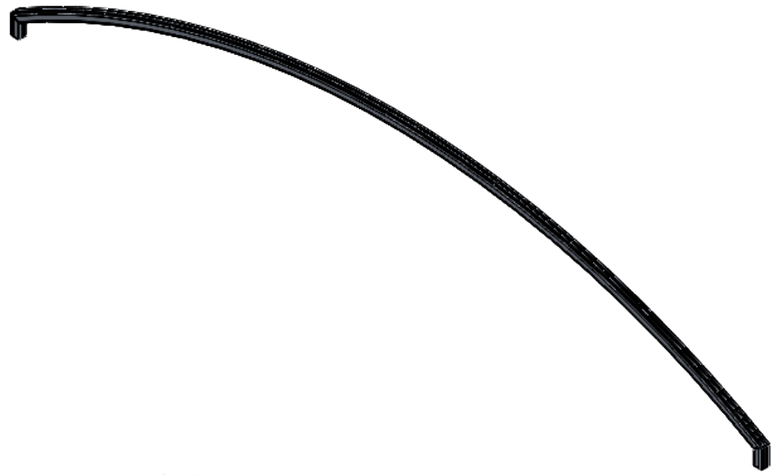

CLIENT:- **DR. PALAVE NAGAR**				NIHVA TECHNOLOGIES PVT.LTD.PUNE Website - www.nihva.com	
	NAME	SIGN	DATE	TITLE :- PANEL_02 -P2.2	
DRAWN	S.W		13.07.2024	MATERIAL:- AL GNT_006	TREATMENT:- POWDER COATING
CHK'D	P.M.		13.07.2024	PROJECT CODE: - PRJ 24-25 NTPL_236	
APPV'D	V.T.		13.07.2024	DRAWING NO: - PRJ 24-25 NTPL_236-0101-02-003	
if any queries contact - supportautomation@nihva.com				PROJECT NAME - RETRACTABLE SLIDING ROOF	
ALL DIMENSION ARE IN mm		A3		SCALE - 1.1 QTY:-	SHEET 11 OF 19


ITEM NO.	PART NUMBER	DESCRIPTION	QTY.
1	SQ TUBE 50X50X1.5 MM L-875	INHOUSE +STD	27

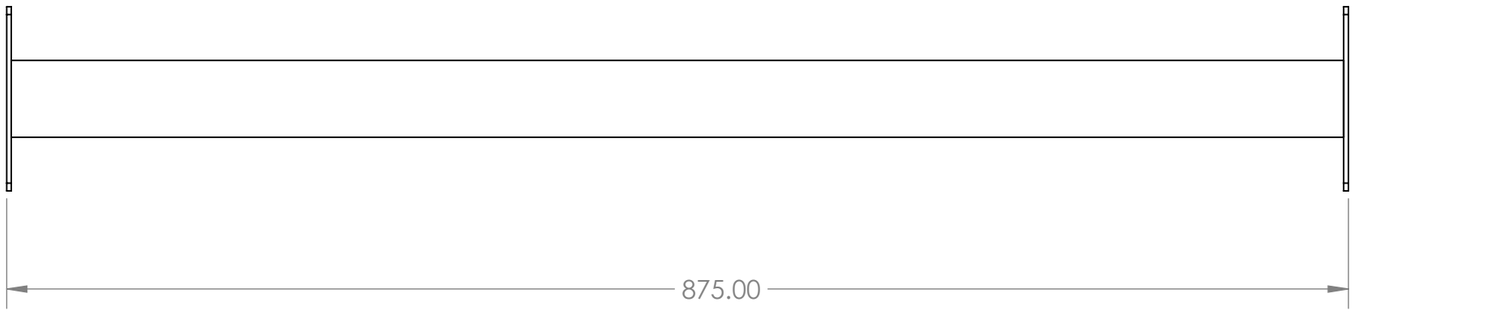


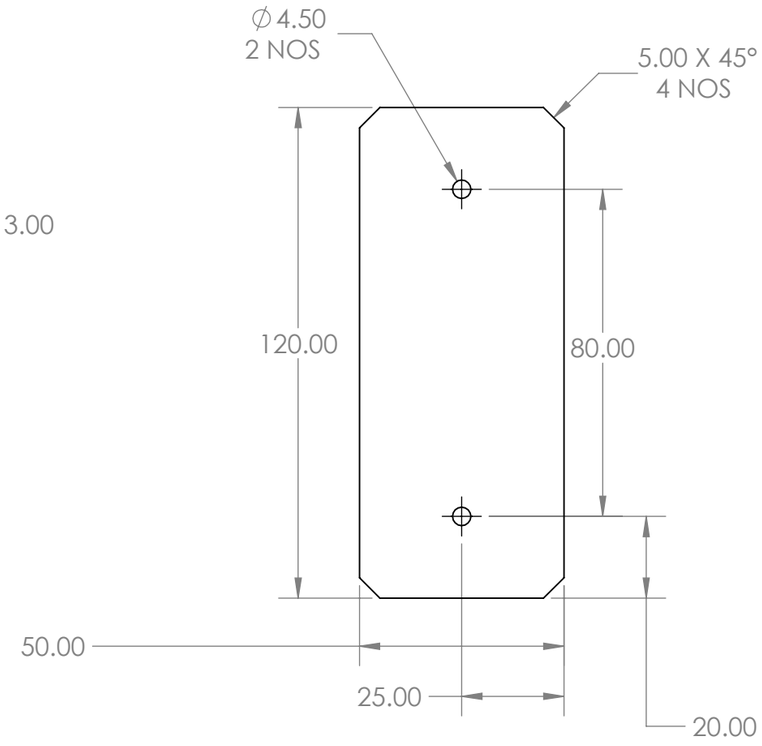

CLIENT:- DR. PALAVE NAGAR				NIHVA TECHNOLOGIES PVT.LTD.PUNE Website - www.nihva.com	
	NAME	SIGN	DATE	TITLE :- PANEL_02 - SUPPORT TUBE	
DRAWN	S.W		13.07.2024	MATERIAL:- MS	TREATMENT:- POWDER COATING
CHK'D	P.M.		13.07.2024	PROJECT CODE: - PRJ 24-25 NTPL_236	
APPV'D	V.T.		13.07.2024	DRAWING NO: - PRJ 24-25 NTPL_236-0101-02-004	
if any queries contact - supportautomation@nihva.com				PROJECT NAME - RETRACTABLE SLIDING ROOF	
ALL DIMENSION ARE IN mm	A3			SCALE - 1.1 QTY:-	SHEET 12 OF 19


ITEM NO.	PART NUMBER	DESCRIPTION	QTY.
1	ROLLER BRG HSG	100X80X105 MM (VMC PART)	1
2	SKF_NATR 12	BRG(STD)	2
3	SKF_NATR 8	BRG(STD)	2

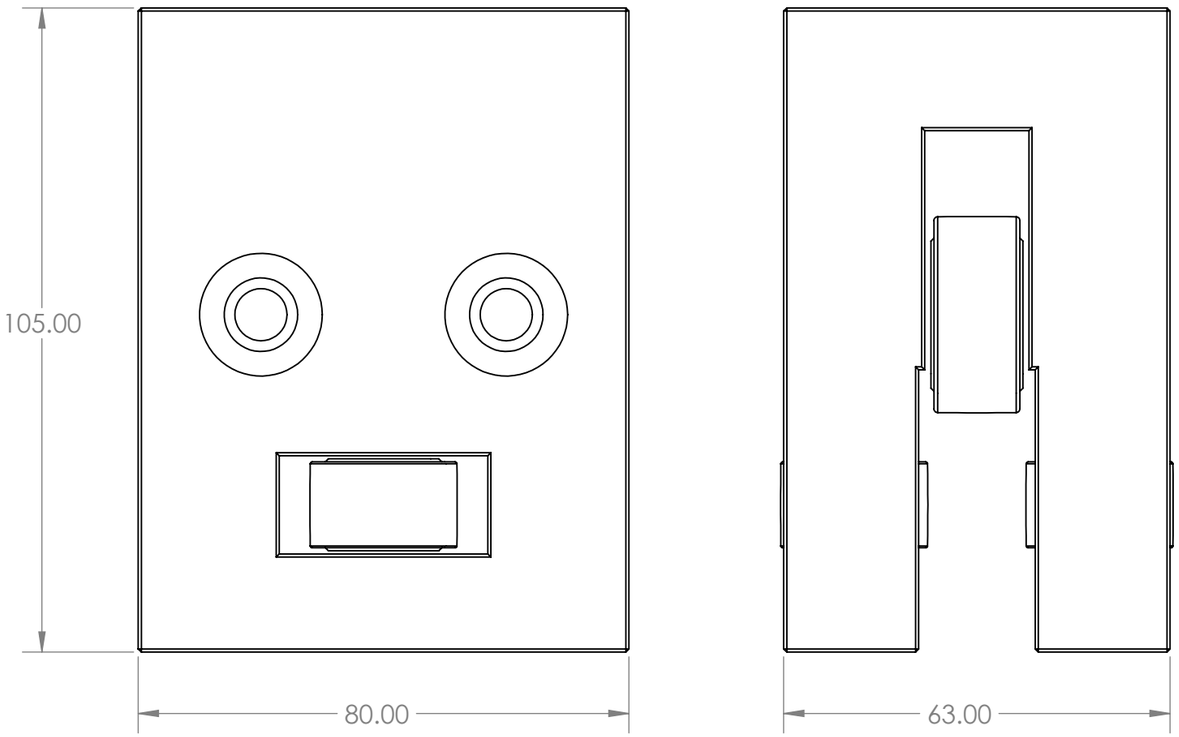


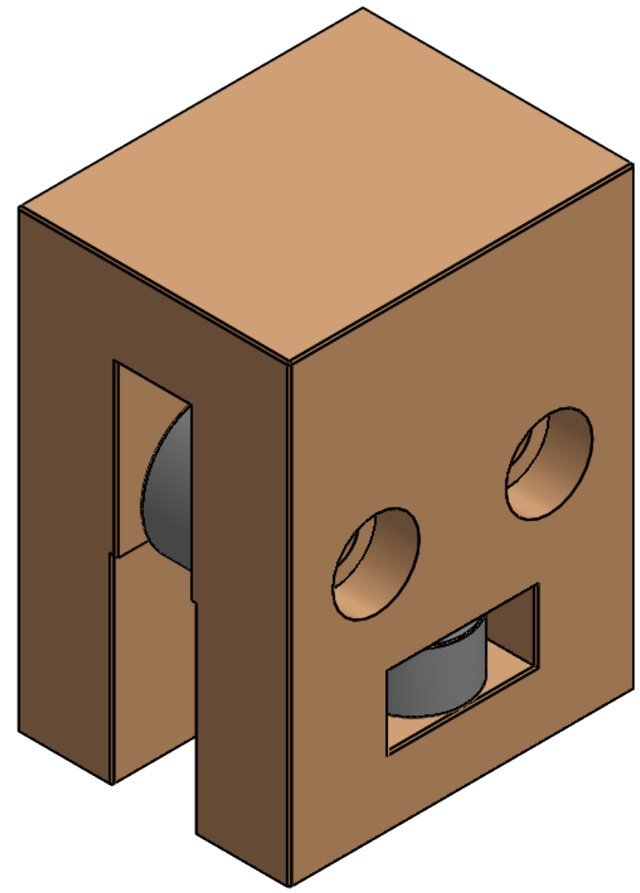


CLIENT:- **DR. PALAVE NAGAR**				NIHVA TECHNOLOGIES PVT.LTD.PUNE Website - www.nihva.com	
	NAME	SIGN	DATE	TITLE :- PANEL_02 LIFTING BLOCK ASM	
DRAWN	S.W		13.07.2024	MATERIAL:- AL	TREATMENT:- VMC
CHK'D	P.M.		13.07.2024	PROJECT CODE: - PRJ 24-25 NTPL_236	
APPV'D	V.T.		13.07.2024	DRAWING NO: - PRJ 24-25 NTPL_236-0101-02-005	
if any queries contact - supportautomation@nihva.com				PROJECT NAME - RETRACTABLE SLIDING ROOF	
ALL DIMENSION ARE IN mm		A3		SCALE - 1.1 QTY:-	SHEET 13 OF 19

ITEM NO.	PART NUMBER	DESCRIPTION	QTY.
1	enclouser asm panel_03	GNT_006	1
2	P3.2	GNT_006	2
3	P3.1	GNT_006	1
4	P3.3	GNT_006	2
5	SQ TUBE 50X50X1.5 MM L-875	INHOUSE +STD	27
6	lift track assembely block	MACHINING PART	4
7	AL CORNER WELD PLATE _NTPL236	3 MM THK(LASER CUT)	2

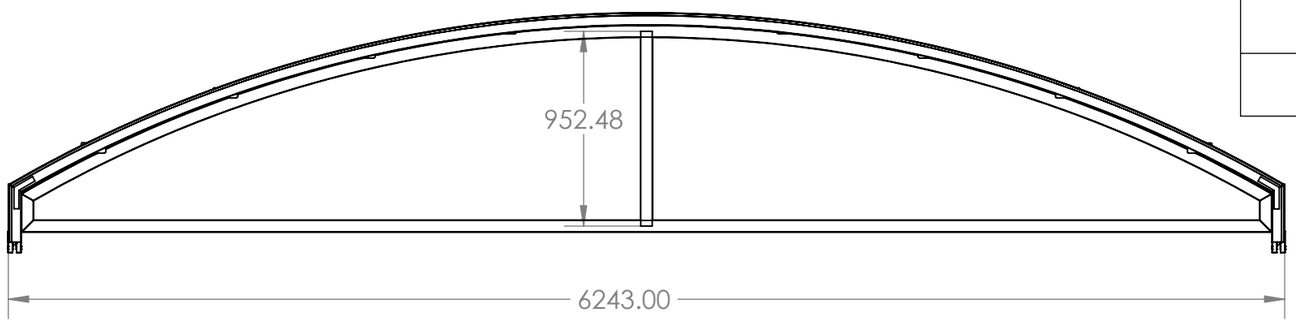


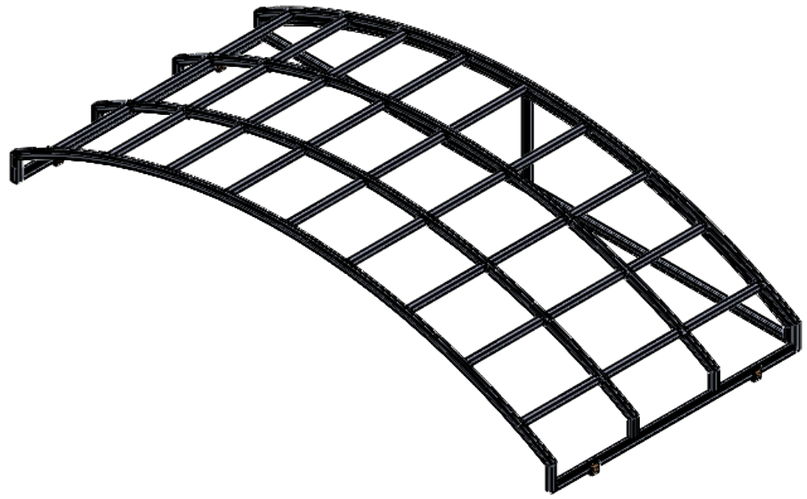

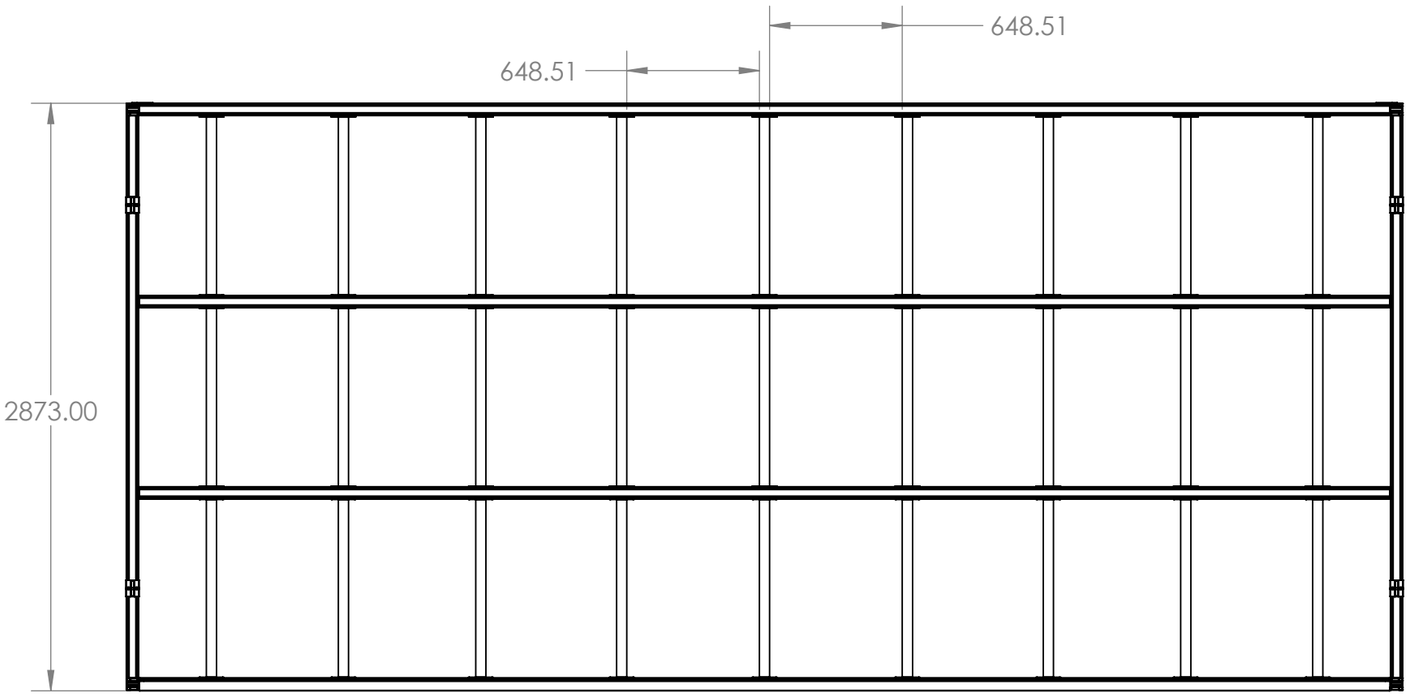



CLIENT:-	DR. PALAVE NAGAR			NIHVA Technologies Pvt. Ltd.	NIHVA TECHNOLOGIES PVT.LTD.PUNE Website - www.nihva.com
	NAME	SIGN	DATE	TITLE :- PANEL_03 ASM	
DRAWN	S.W		13.07.2024	MATERIAL:-	TREATMENT:-
CHK'D	P.M.		13.07.2024	PROJECT CODE: - PRJ 24-25 NTPL_236	
APPV'D	V.T.		13.07.2024	DRAWING NO: - PRJ 24-25 NTPL_236-0101-03-000	
if any queries contact - supportautomation@nihva.com				PROJECT NAME - RETRACTABLE SLIDING ROOF	
ALL DIMENSION ARE IN mm	A3			SCALE - 1.1 QTY:-	SHEET 14 OF 19

ITEM NO.	PART NUMBER	DESCRIPTION	QTY.
1	P3.1	GNT_006	1
2	P3.4 (enclosure)	GNT_006	1

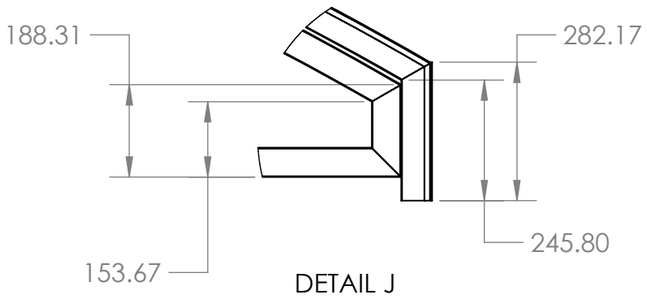


DETAIL J
SCALE 2 : 25

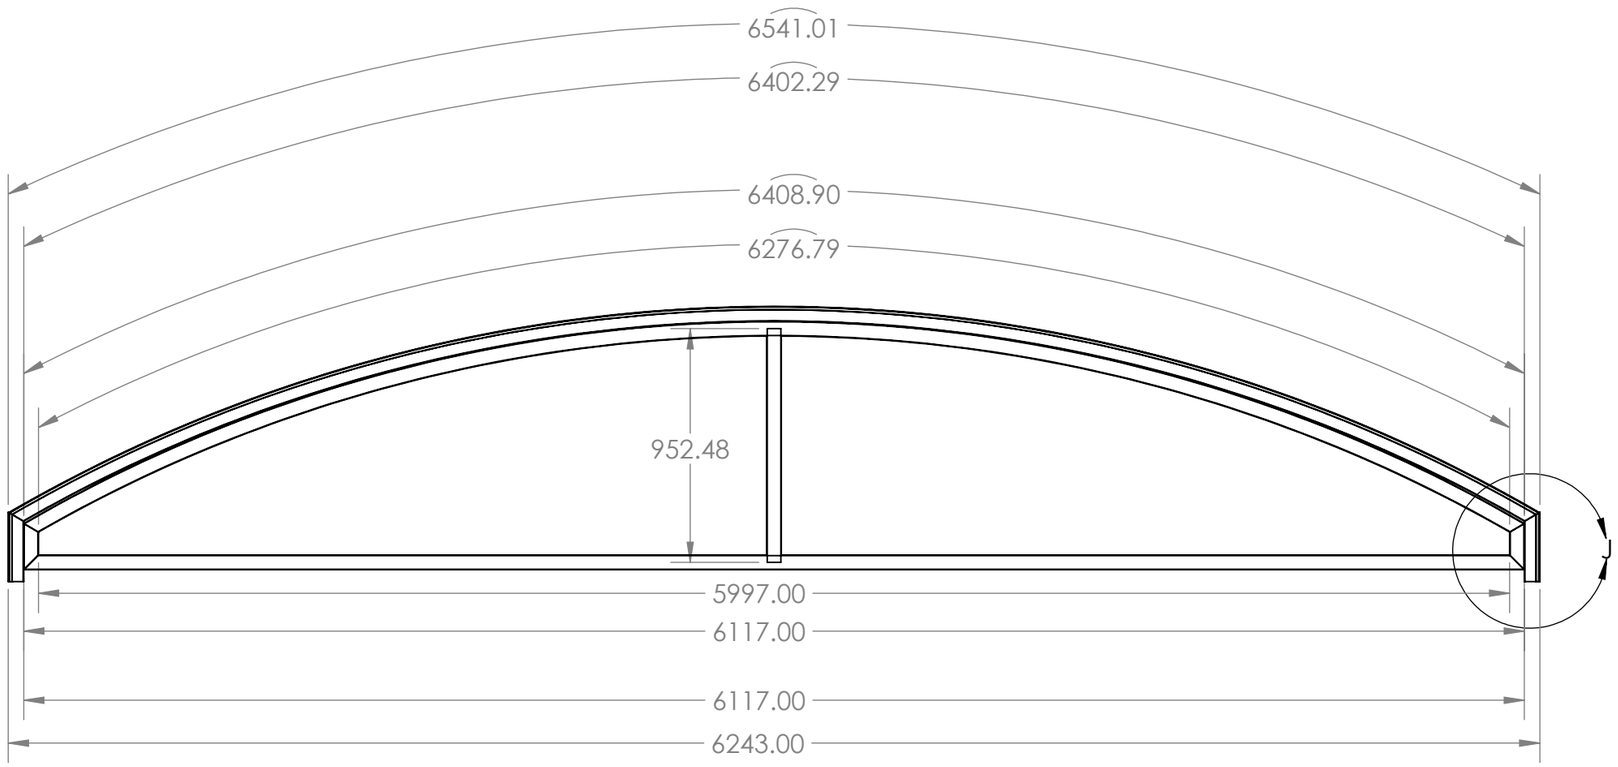


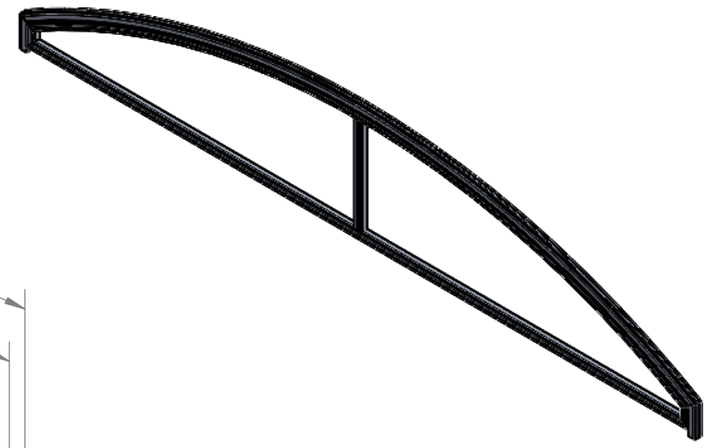

CLIENT:- **DR. PALAVE NAGAR**				NIHVA TECHNOLOGIES PVT.LTD.PUNE Website - www.nihva.com
	NAME	SIGN	DATE	TITLE :- PANEL_03 ENCLOUSER ASM
DRAWN	S.W		13.07.2024	MATERIAL:- AL GNT_006 / TREATMENT:-
CHK'D	P.M.		13.07.2024	PROJECT CODE: - PRJ 24-25 NTPL_236
APPV'D	V.T.		13.07.2024	DRAWING NO: - PRJ 24-25 NTPL_236-0101-03-001
if any queries contact - supportautomation@nihva.com				PROJECT NAME - RETRACTABLE SLIDING ROOF
ALL DIMENSION ARE IN mm	A3			SCALE - 1.1 QTY:- / SHEET 15 OF 19


ITEM NO.	PART NUMBER	DESCRIPTION	QTY.
1	P3.1	GNT_006	1

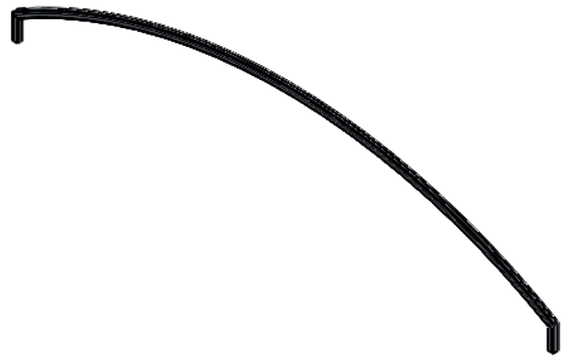

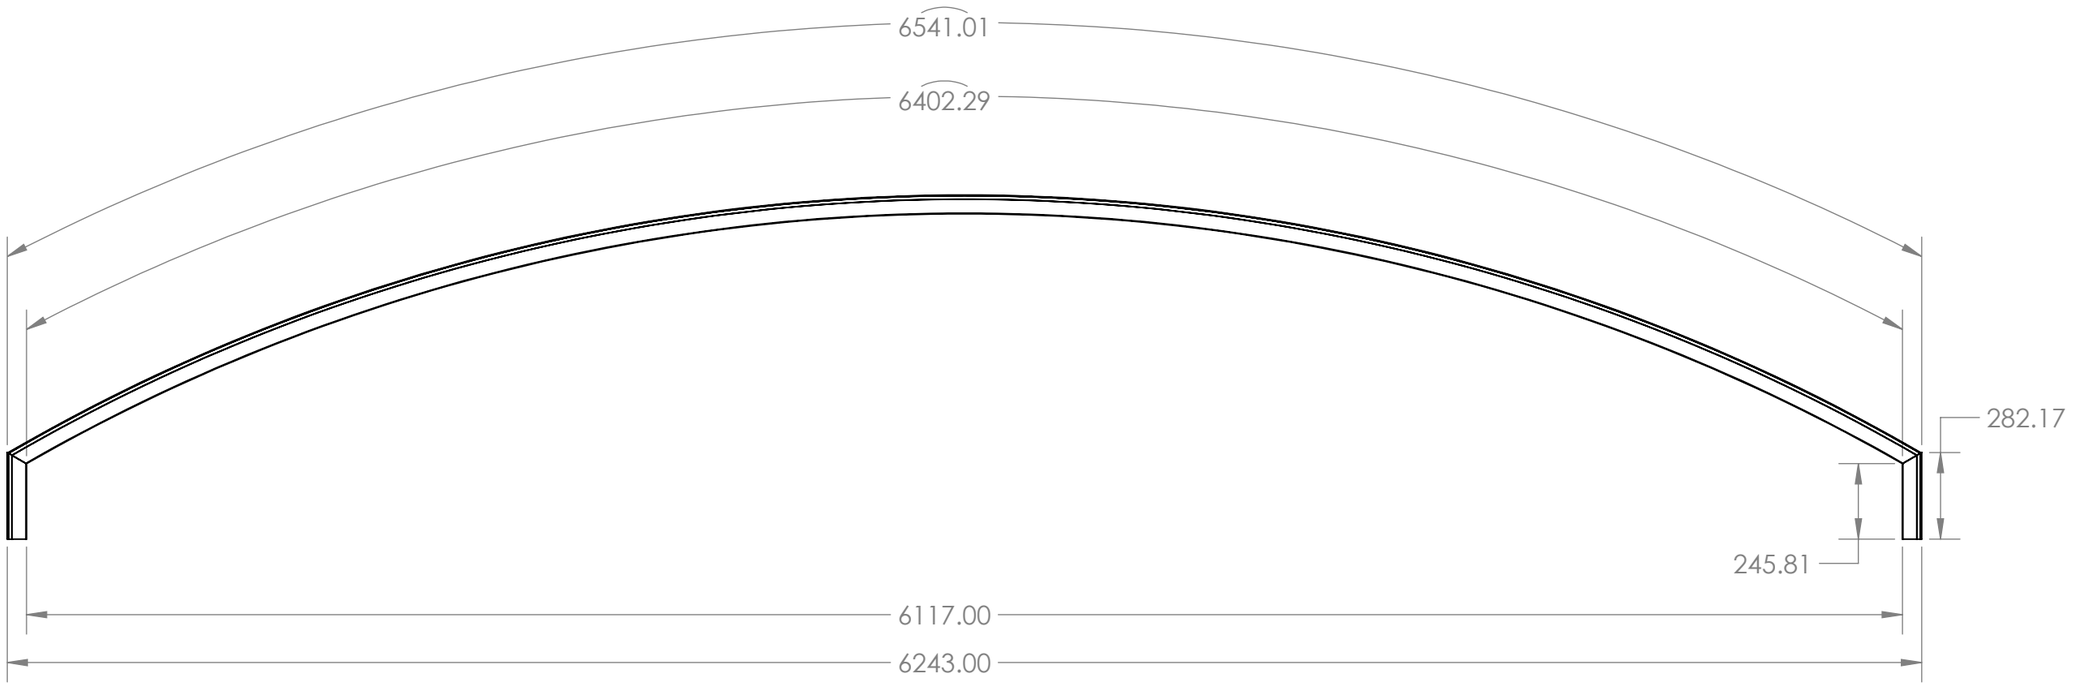


CLIENT:- DR. PALAVE NAGAR				NIHVA TECHNOLOGIES PVT.LTD.PUNE Website - www.nihva.com	
	NAME	SIGN	DATE	TITLE :- PANEL_03 - P3.1	
DRAWN	S.W		13.07.2024	MATERIAL:- AL GNT_006	TREATMENT:-POWDER COATING
CHK'D	P.M.		13.07.2024	PROJECT CODE: - PRJ 24-25 NTPL_236	
APPV'D	V.T.		13.07.2024	DRAWING NO: - PRJ 24-25 NTPL_236-0101-03-002	
if any queries contact - supportautomation@nihva.com				PROJECT NAME - RETRACTABLE SLIDING ROOF	
ALL DIMENSION ARE IN mm	A3			SCALE - 1.1 QTY:-	SHEET 16 OF 19

ITEM NO.	PART NUMBER	DESCRIPTION	QTY.
1	P3.3	GNT_006	2

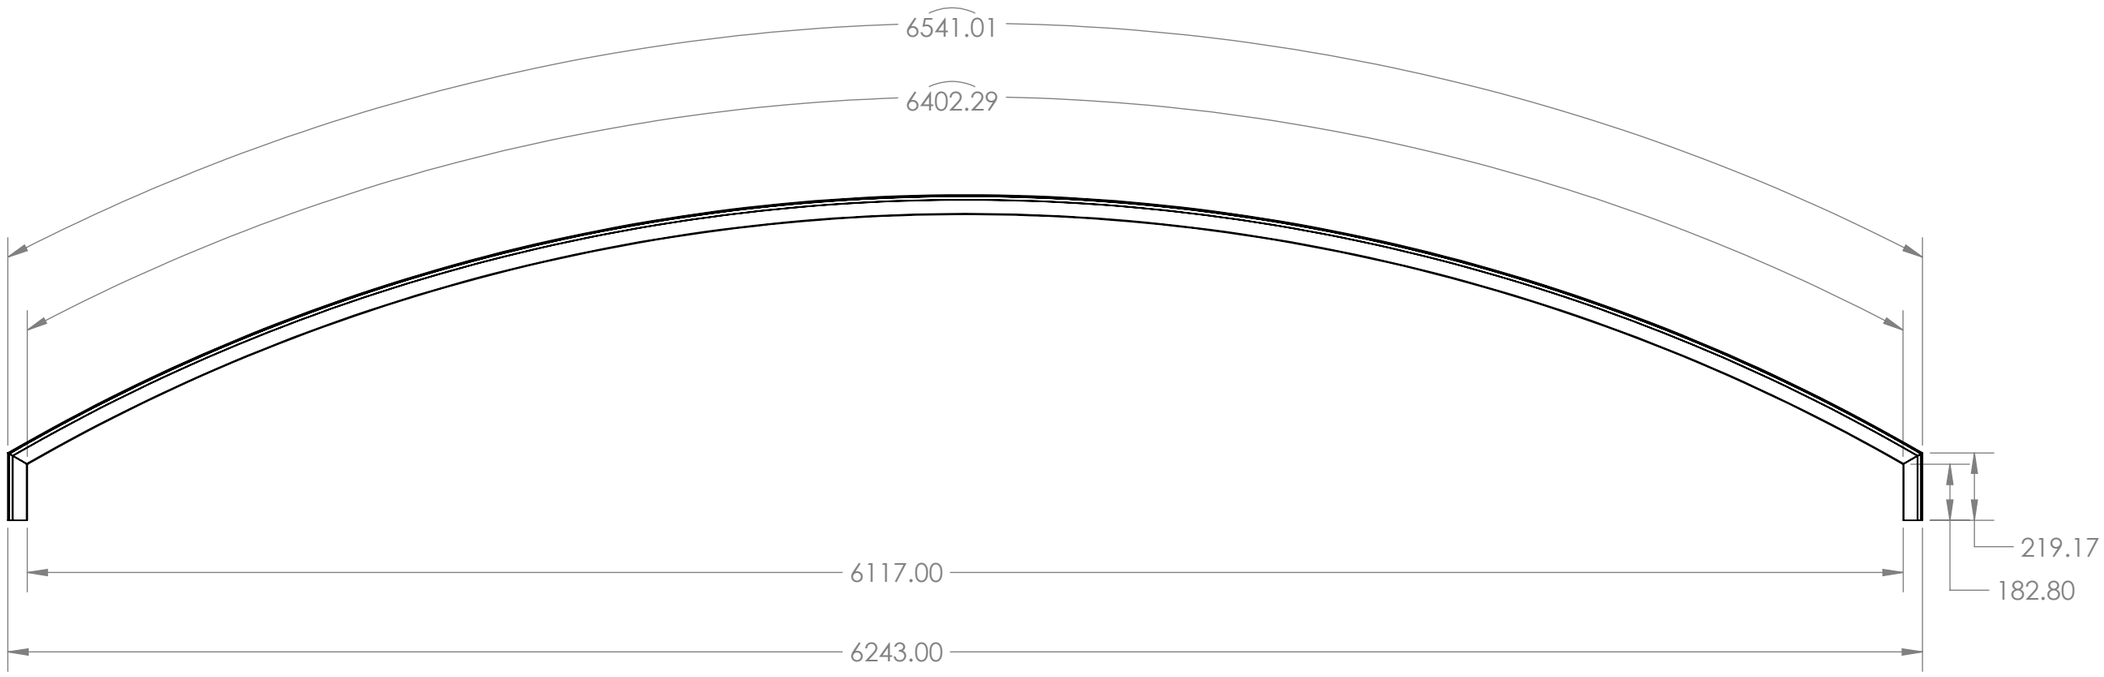

CLIENT:- DR. PALAVE NAGAR				NIHVA TECHNOLOGIES PVT.LTD.PUNE Website - www.nihva.com	
	NAME	SIGN	DATE	TITLE :- PANEL_03 - P3.3	
DRAWN	S.W		13.07.2024	MATERIAL:- AL GNT_006	TREATMENT:-POWDER COATING
CHK'D	P.M.		13.07.2024	PROJECT CODE: - PRJ 24-25 NTPL_236	
APPV'D	V.T.		13.07.2024	DRAWING NO: - PRJ 24-25 NTPL_236-0101-03-003	
if any queries contact - supportautomation@nihva.com				PROJECT NAME - RETRACTABLE SLIDING ROOF	
ALL DIMENSION ARE IN mm	A3			SCALE - 1.1 QTY:-	SHEET 17 OF 19

ITEM NO.	PART NUMBER	DESCRIPTION	QTY.
1	AL CORNER WELD PLATE _NTPL236	3 MM THK(LASER CUT)	52

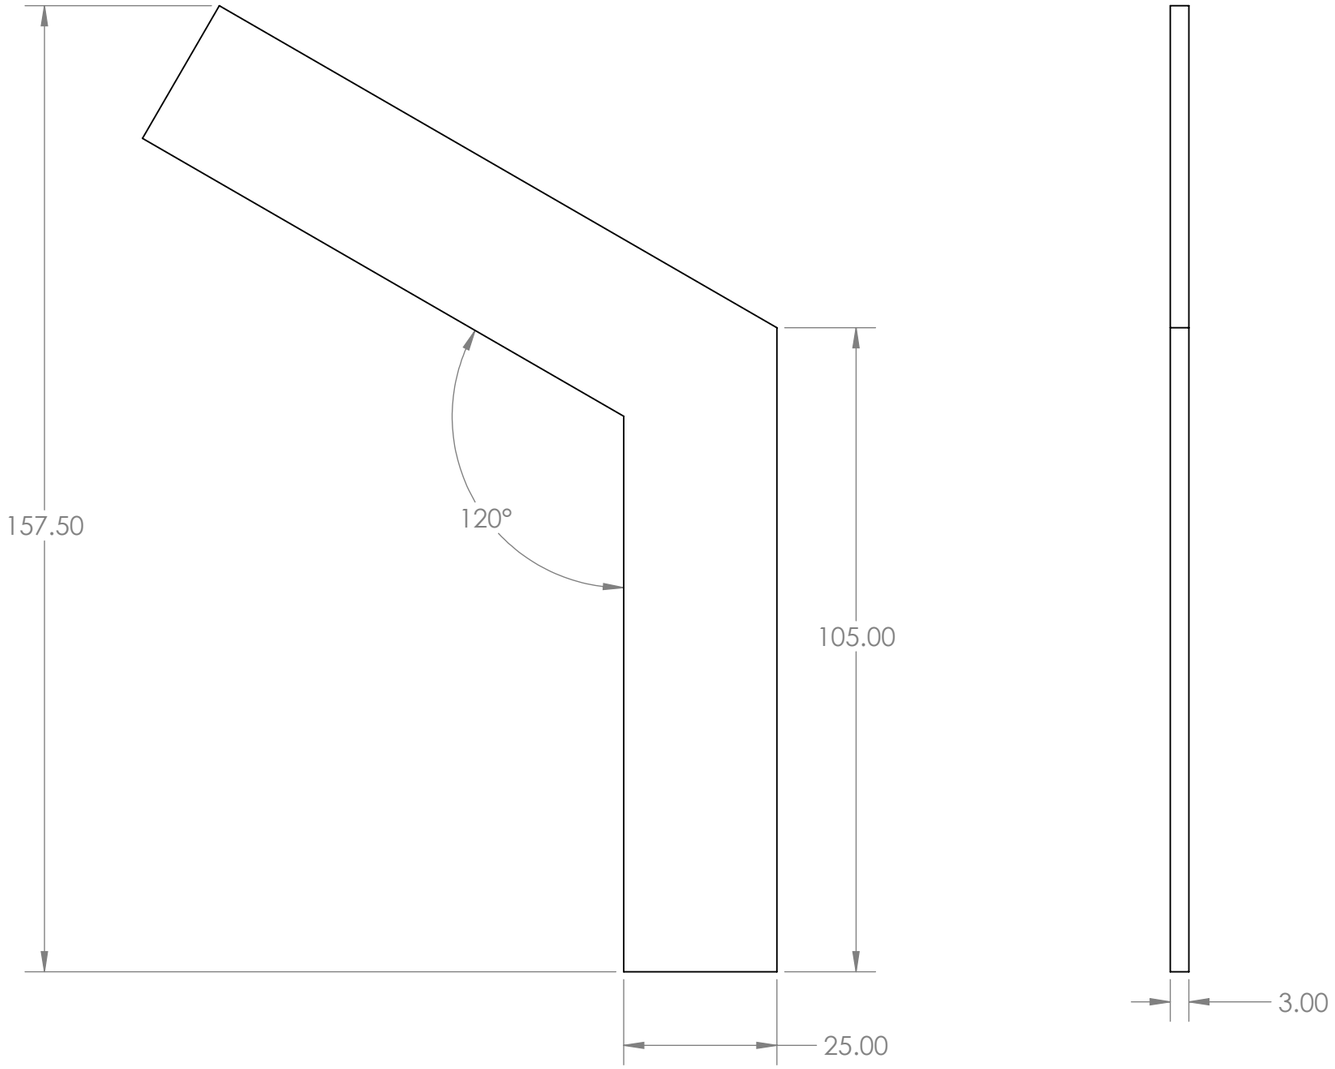

CLIENT:- **DR. PALAVE NAGAR**				NIHVA TECHNOLOGIES PVT.LTD.PUNE Website - www.nihva.com	
	NAME	SIGN	DATE	TITLE :- AL WELD PLATE FOR ALL PANEL	
DRAWN	S.W		13.07.2024	MATERIAL:- MS	TREATMENT:-LASER CUT + PC
CHK'D	P.M.		13.07.2024	PROJECT CODE: - PRJ 24-25 NTPL_236	
APPV'D	V.T.		13.07.2024	DRAWING NO: - PRJ 24-25 NTPL_236-0101-03-004	
if any queries contact - supportautomation@nihva.com				PROJECT NAME - RETRACTABLE SLIDING ROOF	
ALL DIMENSION ARE IN mm		A3		SCALE - 1.1 QTY:-	SHEET 18 OF 19

TITLE - PROPOSED PLAN LAYOUT				NIHVA TECHNOLOGIES PVT.LTD.PUNE Website - www.nihva.com
	NAME	SIGNATURE	DATE	CLIENT -
DRAWN	D.V.		25.07.2023	PRODUCT - RETRACTABLE ROOF
CHK'D	P.M.		25.07.2023	SITE LOCATION -
APPV'D	V.T.		25.07.2023	
if any queries contact - supportautomation@nihva.com				REVISION - 0
ALL DIMENSION ARE IN mm		A3		SCALE - 1.1 / SHEET 19 OF 19