
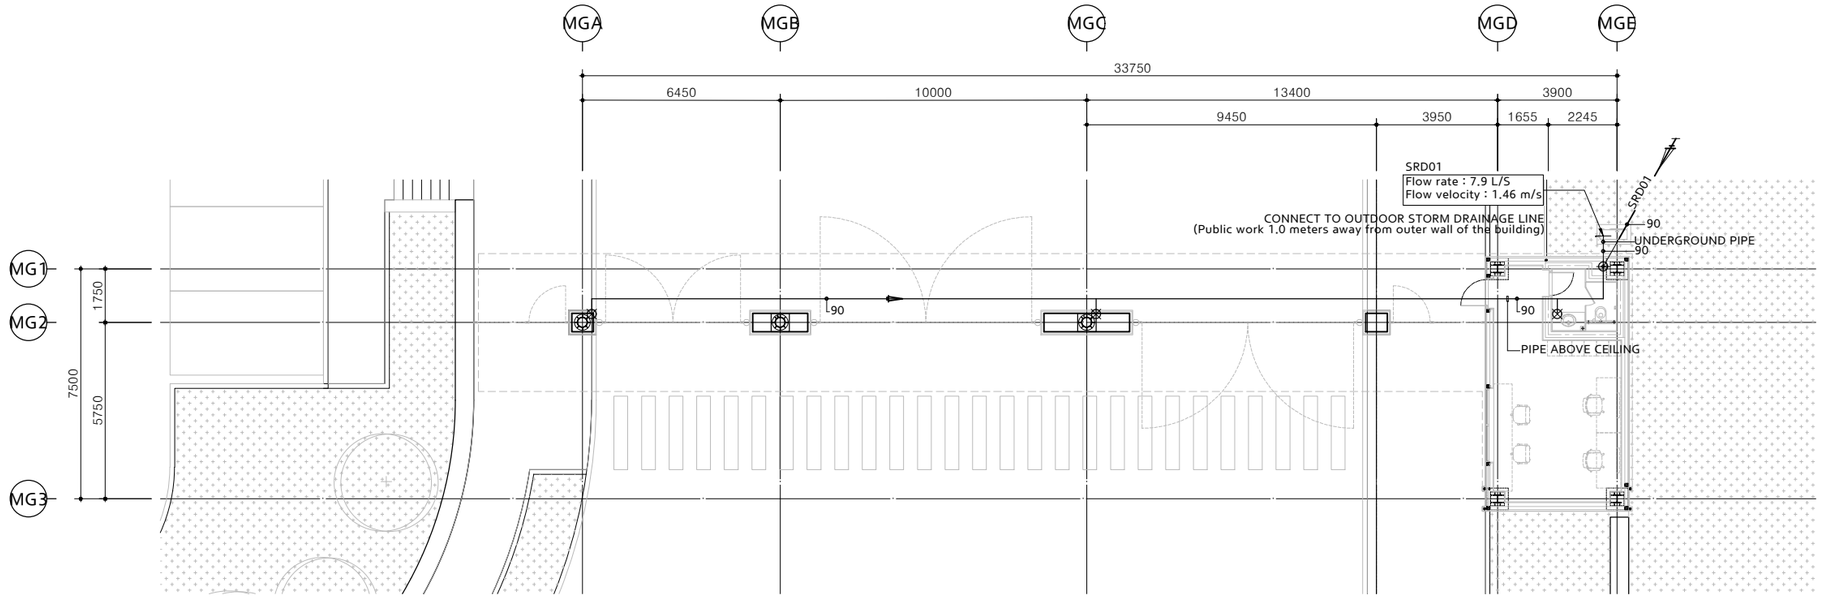



1 GROUND FLOOR STORMWATER DRAIN PLAN

SCALE : 1/100

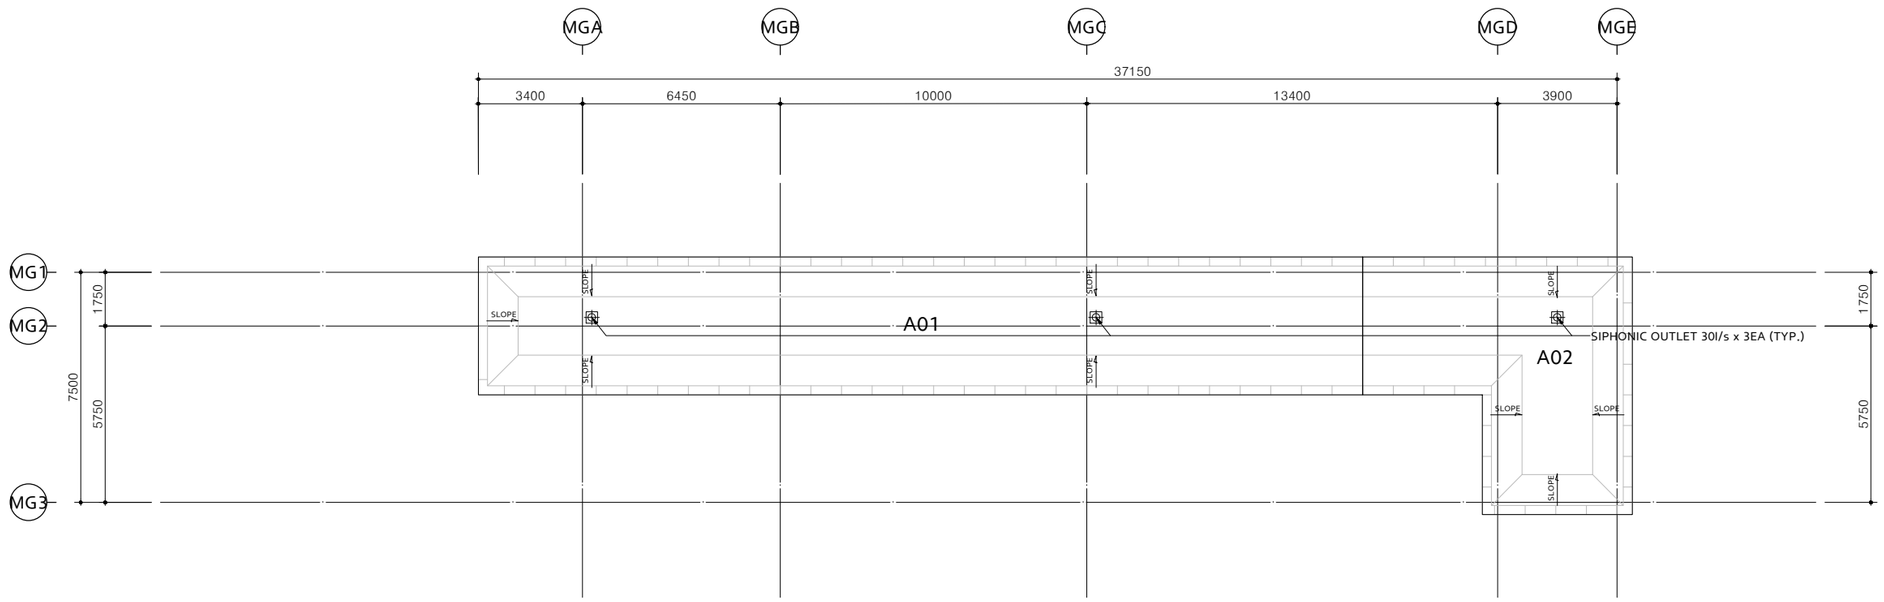

2 ROOF STORMWATER DRAIN PLAN

SCALE : 1/100

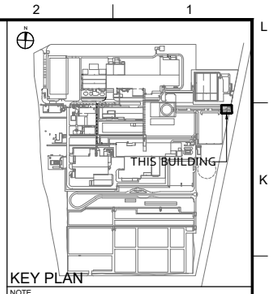

KEY PLAN

NOTE

1. GROUND FLOOR LEVEL
   -GROUND FLOOR FL ±0.00 = EL+663.20
2. LEVEL(T.O.C) OF GROUND FLOOR, WHICH IS THE BASE LEVEL OF ALL LEVEL DIMENSIONS.
3. THIS DRAWING SHOULD BE APPROVED BY HEC & HMI BEFORE APPLICATION
4. REFER TO DRAWING NUMBER "000-G-0001~0900" FOR GENERAL NOTES AND STANDARDS DETAIL.
5. SITE SURVEY FOR THIS DRAWING SHALL BE REQUIRED AND SUPERVISOR'S APPROVAL SHALL BE OBTAINED PRIOR TO CONSTRUCTION.
6. IF THE DRAWING IS DIFFERENT FROM CURRENT SITE, SUPERVISORS AND DESIGNER'S APPROVAL SHALL BE OBTAINED PRIOR TO CONSTRUCTION.
7. STRUCTURES IN THE BUILDING SHOULD BE ALKYD ENAMEL PAINT ON ANTI- RUST PAINT.
8. ALL SEALANT SHALL BE SUBMITTED TO THE MANUFACTURING ENGINEERING TEAM AND APPROVED PRIOR TO THE INSTALLATION BY THEM.

REV.	DESCRIPTION	DRAWN	DATE
0	CONSTRUCTION DRAWING	OH.J.S	2025. 02.14

CLIENT

HYUNDAI

ARCHITECTS & ENGINEERS

JUNGLIM ARCHITECTURE

PROJECT TITLE

PUNE HMI PROJECT

DRAWING TITLE

[MAIN GATE]
GROUND FLOOR & ROOF STORMWATER DRAIN PLAN


SCALE	DRAWN	CHECKED	REVIEWED	APPROVED	APPROVED
A1: 1/100 A3:1/200	OH.J.S	HONG.G.D	LEE.S.L	HEC INDIA	PARK.T.S
DATE 14 FEB,2025					

MAIN CONTRACTOR

HEC INDIA LLP

DRAWING NO.	REV.
WA-IPB-640-A-3002	0

A1 SIZE (841mm x 594mm)

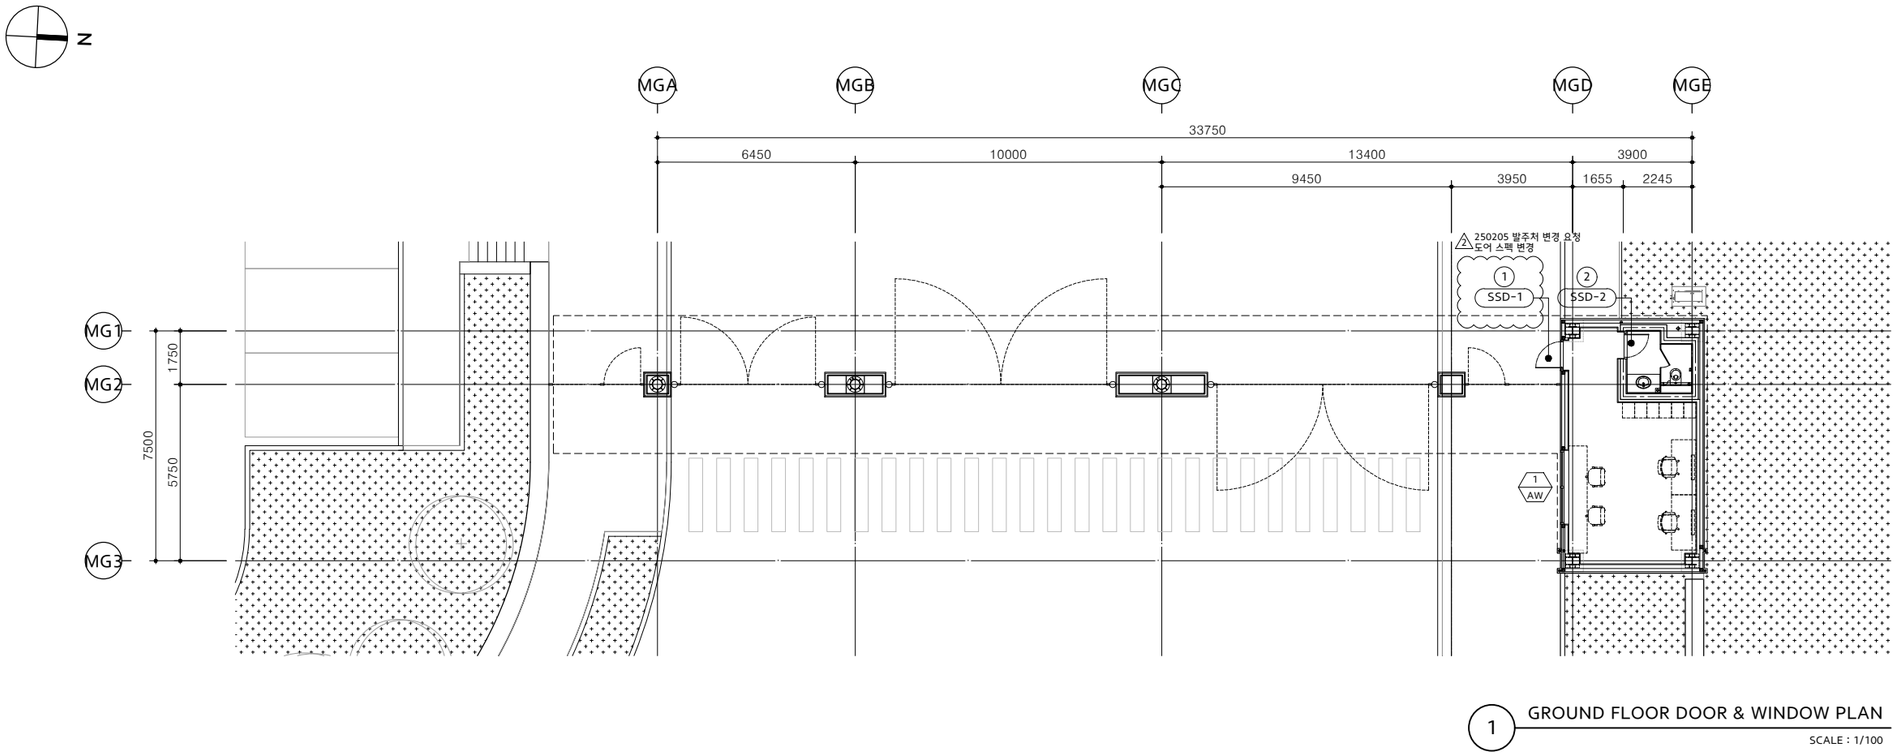


1 GROUND FLOOR DOOR & WINDOW PLAN

SCALE : 1/100


DOOR SHAPE & LEGEND

1 GENERAL NOTE

DOOR SYMBOL

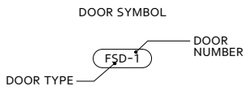


WINDOW SYMBOL

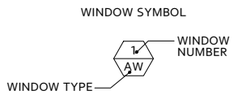


2 DOOR & WINDOW TYPE

SD	STEEL DOOR	OHD	OVERHEAD DOOR
FSD	FIRE STEEL DOOR	RS	ROOL-UP SHUTTER
SSD	S' STEEL DOOR	RRS	RAPID ROOL-UP SHUTTER
SFD	S' STEEL FOLDING DOOR	AW	ALUMINUM WINDOW
ASD	AUTO SLIDING DOOR	SSW	S' STEEL WINDOW
SLID	SLID DOOR	AG	ALUMINUM GRILL


3 DOOR SHAPE : SINGLE DOOR

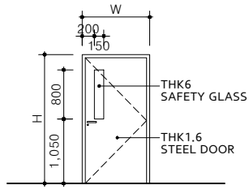

DOOR SHAPE - S1

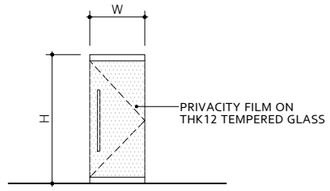

DOOR SHAPE - S2

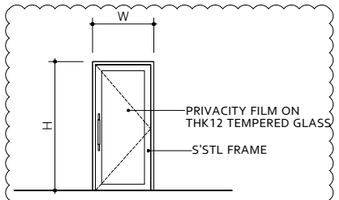


DOOR SHAPE - S3

2 250205 발주처 변경 요청
도어 스펙 변경

DOOR SCHEDULE

FLOOR NO.	NO.	DOOR NO.	MATERIAL		DOOR SIZE			SHAPE	MATERIAL			FIRE	KEY SET	HW SET	REMARKS
			DOOR	FRAME	THK	WIDTH	HEIGHT		HEAD	JAMB	SILL				
1F	1	SSD-1	GLASS	S'STL	-	1,000	2,100	S3	-	-	-	-	-	521	2 250205 발주처 변경 요청 도어 스펙 변경
	2	SSD-2	GLASS	S'STL	-	900	2,100	S2	-	-	-	-	-	501	

WINDOW SCHEDULE

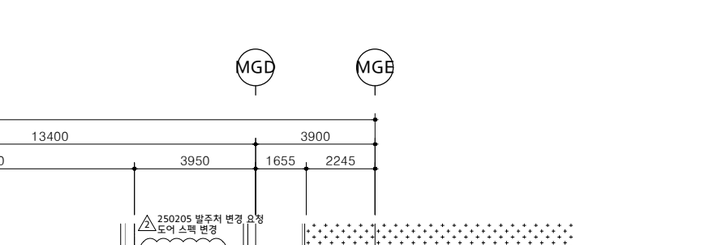

ID	1 AW ALUMINUM WINDOW	QT'Y	1 EA
GLAZING	THK18 PAIR GLASS		
FRAME	AL.BAR / ELECTROSTATIC POWDER COATING		
HARDWARE	-		

ID	-	QT'Y	-
GLAZING	-		
FRAME	-		
HARDWARE	-		

KEY PLAN

NOTE

REV.	DESCRIPTION	DRAWN	DATE
2	CD Rev.2	OH.J.S	2025.02.14
1	CD Rev.1	OH.J.S	2024.10.18
0	CONSTRUCTION DRAWING	OH.J.S	2024.07.30
B	DD Rev.B	OH.J.S	2024.06.28
A	DESIGN DEVELOPMENT	OH.J.S	2024.04.15

CLIENT

HYUNDAI

ARCHITECTS & ENGINEERS

JUNGLIM ARCHITECTURE

PROJECT TITLE

PUNE HMI PROJECT

DRAWING TITLE

[MAIN GATE]
DOOR, WINDOW PLAN & SCHEDULE

SCALE	DRAWN	CHECKED	REVIEWED	APPROVED	APPROVED
A1:1/100 A3:1/200	OH.J.S	HONG.G.D	LEE.S.L	HEC INDIA	PARK.T.S
DATE 14 FEB,2025					

MAIN CONTRACTOR

HEC KOREA LLP

DRAWING NO. WA-IPB-640-A-6101

REV. 2

A1 SIZE (841mm x 594mm)

⚠1 250205 검토사항 반영

HW	ITEM	DESCRIPTION	MANUFACT	MODEL	Q`TY
100	BH-49	BUTT HINGE(SST'L) 5"X4"	BRITON	AH500-5X4"	3 EA
100	DC-06	DOOR CLOSER NHO	FALCON	SC81A-RW/PA	1 EA
100	DS-05	WALL BUMPER	IVES	WS401/402CVX	1 EA
100	PP-01	PUSH PULL PLATE	IVES	8302-4X16"	1 EA
101	BH-49	BUTT HINGE(SST'L) 5"X4"	BRITON	AH500-5X4"	3 EA
101	DS-01	FLOOR STOP	IVES	FS436	1 EA
101	MDL-053	MORTISE LOCKSET-CLASSROOM	SCHLAGE	M70L/SFIC/07B	1 EA
110	BH-49	BUTT HINGE(SST'L) 5"X4"	BRITON	AH500-5X4"	3 EA
110	DC-06	DOOR CLOSER NHO	FALCON	SC81A-RW/PA	1 EA
110	DS-01	FLOOR STOP	IVES	FS436	1 EA
110	MDL-051	MORTISE LOCKSET-ENTRANCE	SCHLAGE	M56L/SFIC/07B	1 EA
111	BH-49	BUTT HINGE(SST'L) 5"X4"	BRITON	AH500-5X4"	3 EA
111	DC-06	DOOR CLOSER NHO	FALCON	SC81A-RW/PA	1 EA
111	DS-01	FLOOR STOP	IVES	FS436	1 EA
111	MDL-053	MORTISE LOCKSET-CLASSROOM	SCHLAGE	M70L/SFIC/07B	1 EA
111A	BH-49	BUTT HINGE(SST'L) 5"X4"	BRITON	AH500-5X4"	3 EA
111A	CK-05	DIGITAL LOCK	SCHLAGE	S-8100	1 EA
111A	DC-06	DOOR CLOSER NHO	FALCON	SC81A-RW/PA	1 EA
111A	DS-01	FLOOR STOP	IVES	FS436	1 EA
112	BH-49	BUTT HINGE(SST'L) 5"X4"	BRITON	AH500-5X4"	3 EA
112	DC-06	DOOR CLOSER NHO	FALCON	SC81A-RW/PA	1 EA
112	DS-05	WALL BUMPER	IVES	WS401/402CVX	1 EA
112	MDL-049	MORTISE LOCKSET-PASSAGE	SCHLAGE	M10 07B	1 EA
113	BH-49	BUTT HINGE(SST'L) 5"X4"	BRITON	AH500-5X4"	4 EA
113	DC-06	DOOR CLOSER NHO	FALCON	SC81A-RW/PA	1 EA
113	DS-01	FLOOR STOP	IVES	FS436	1 EA
113	MDL-051	MORTISE LOCKSET-ENTRANCE	SCHLAGE	M56L/SFIC/07B	1 EA
115	BH-49	BUTT HINGE(SST'L) 5"X4"	BRITON	AH500-5X4"	4 EA
115	DC-06	DOOR CLOSER NHO	FALCON	SC81A-RW/PA	1 EA
115	DS-01	FLOOR STOP	IVES	FS436	1 EA
115	MDL-053	MORTISE LOCKSET-CLASSROOM	SCHLAGE	M70L/SFIC/07B	1 EA
130	BH-56	BUTT HINGE(SST'L) 4"X4"	BRITON	AH500-4X4"	3 EA
130	DS-01	FLOOR STOP	IVES	FS436	1 EA
130	MDL-051	MORTISE LOCKSET-ENTRANCE	SCHLAGE	M56L/SFIC/07B	1 EA
180	AP-01	ARMOR PLATE	IVES	8400-42X36"	1 EA
180	BH-49	BUTT HINGE(SST'L) 5"X4"	BRITON	AH500-5X4"	3 EA
180	DC-06	DOOR CLOSER NHO	FALCON	SC81A-RW/PA	1 EA
180	DS-05	WALL BUMPER	IVES	WS401/402CVX	1 EA
180	MDL-001	MORTISE DEADLOCK	SCHLAGE	M64L/SFIC	1 SET
180	PP-01	PUSH PULL PLATE	IVES	8302-4X16"	1 EA
200	BH-49	BUTT HINGE(SST'L) 5"X4"	BRITON	AH500-5X4"	6 EA
200	DC-06	DOOR CLOSER NHO	FALCON	SC81A-RW/PA	1 EA
200	DPS-01	DUST PROOF STRIKE	IVES	DP1	1 EA
200	DS-01	FLOOR STOP	IVES	FS436	1 EA
200	FB-02	FLUSH BOLT-12"	IVES	FB458-12-MD	2 EA
200	MDL-051	MORTISE LOCKSET-ENTRANCE	SCHLAGE	M56L/SFIC/07B	1 EA
200	MDT-008	MORTISE DUMMY TRIM	SCHLAGE	M172 07B	1 EA

HW	ITEM	DESCRIPTION	MANUFACT	MODEL	Q`TY
201	BH-49	BUTT HINGE(SST'L) 5"X4"	BRITON	AH500-5X4"	8 EA
201	DC-06	DOOR CLOSER NHO	FALCON	SC81A-RW/PA	1 EA
201	DPS-01	DUST PROOF STRIKE	IVES	DP1	1 EA
201	DS-01	FLOOR STOP	IVES	FS436	1 EA
201	FB-02	FLUSH BOLT-12"	IVES	FB458-12-MD	1 EA
201	FB-03	FLUSH BOLT-24"	IVES	FB458-24-MD	1 EA
201	MDL-051	MORTISE LOCKSET-ENTRANCE	SCHLAGE	M56L/SFIC/07B	1 EA
201	MDT-008	MORTISE DUMMY TRIM	SCHLAGE	M172 07B	1 EA
202	AFB-01	AUTO FLUSH BOLT	IVES	FB31P-12-MD	1 EA
202	BH-49	BUTT HINGE(SST'L) 5"X4"	BRITON	AH500-5X4"	8 EA
202	DC-06	DOOR CLOSER NHO	FALCON	SC81A-RW/PA	1 EA
202	DPS-01	DUST PROOF STRIKE	IVES	DP1	1 EA
202	DS-01	FLOOR STOP	IVES	FS436	1 EA
202	MDL-051	MORTISE LOCKSET-ENTRANCE	SCHLAGE	M56L/SFIC/07B	1 EA
202	MDT-008	MORTISE DUMMY TRIM	SCHLAGE	M172 07B	1 EA
210	BH-49	BUTT HINGE(SST'L) 5"X4"	BRITON	AH500-5X4"	6 EA
210	CO-01	DOOR COORDINATOR	IVES	COR52	1 EA
210	DC-06	DOOR CLOSER NHO	FALCON	SC81A-RW/PA	2 EA
210	DPS-01	DUST PROOF STRIKE	IVES	DP1	1 EA
210	DS-01	FLOOR STOP	IVES	FS436	2 EA
210	FB-02	FLUSH BOLT-12"	IVES	FB458-12-MD	2 EA
210	MDL-051	MORTISE LOCKSET-ENTRANCE	SCHLAGE	M56L/SFIC/07B	1 EA
210	MDT-008	MORTISE DUMMY TRIM	SCHLAGE	M172 07B	1 EA
211	BH-49	BUTT HINGE(SST'L) 5"X4"	BRITON	AH500-5X4"	8 EA
211	CO-01	DOOR COORDINATOR	IVES	COR52	1 EA
211	DC-06	DOOR CLOSER NHO	FALCON	SC81A-RW/PA	2 EA
211	DPS-01	DUST PROOF STRIKE	IVES	DP1	1 EA
211	DS-01	FLOOR STOP	IVES	FS436	2 EA
211	FB-02	FLUSH BOLT-12"	IVES	FB458-12-MD	1 EA
211	FB-03	FLUSH BOLT-24"	IVES	FB458-24-MD	1 EA
211	MDL-051	MORTISE LOCKSET-ENTRANCE	SCHLAGE	M56L/SFIC/07B	1 EA
211	MDT-008	MORTISE DUMMY TRIM	SCHLAGE	M172 07B	1 EA
212	AFB-01	AUTO FLUSH BOLT	IVES	FB31P-12-MD	1 EA
212	BH-49	BUTT HINGE(SST'L) 5"X4"	BRITON	AH500-5X4"	8 EA
212	CO-01	DOOR COORDINATOR	IVES	COR52	1 EA
212	DC-06	DOOR CLOSER NHO	FALCON	SC81A-RW/PA	2 EA
212	DPS-01	DUST PROOF STRIKE	IVES	DP1	1 EA
212	DS-01	FLOOR STOP	IVES	FS436	2 EA
212	MDL-051	MORTISE LOCKSET-ENTRANCE	SCHLAGE	M56L/SFIC/07B	1 EA
212	MDT-008	MORTISE DUMMY TRIM	SCHLAGE	M172 07B	1 EA
251	DC-01	DOOR CLOSER NHO	FALCON	SC71A-RW/PA	1 EA
251	DPS-01	DUST PROOF STRIKE	IVES	DP1	1 EA
251	DS-01	FLOOR STOP	IVES	FS436	1 EA
251	FB-02	FLUSH BOLT-12"	IVES	FB458-12-MD	2 EA
251	MDL-051	MORTISE LOCKSET-ENTRANCE	SCHLAGE	M56L/SFIC/07B	1 EA
251	MDT-008	MORTISE DUMMY TRIM	SCHLAGE	M172 07B	1 EA
251	PH-03	PIVOT HINGE(OFFSET HUNG)	BRITON	6200-SET-SS	2 SET
251	PH-04	INTERMEDIATE PIVOT HINGE	BRITON	6200-INT-SS	2 EA

KEY PLAN

NOTE

REV.	DESCRIPTION	DRAWN	DATE
1	CD Rev.1	OH.J.S	2025. 02.14
0	CONSTRUCTION DRAWING	OH.J.S	2024. 09.30

CLIENT

HYUNDAI

ARCHITECTS & ENGINEERS

JUNGLIM ARCHITECTURE

PROJECT TITLE

PUNE HMI PROJECT

DRAWING TITLE

[MAIN GATE]
DOOR HARDWARE LIST-1

SCALE A1:1/NONE A3:1/NONE	DRAWN	CHECKED	REVIEWED	APPROVED	APPROVED
DATE	OH.J.S	HONG.G.D	LEE.S.L	HEC INDIA	PARK.T.S
14 FEB,2025					

MAIN CONTRACTOR

HEC INDIA LLP

DRAWING NO. WA-IPB-640-A-6102

REV. 1

A1 SIZE (841mm x 594mm)

⚠1 250205 검토사항 반영

HW	ITEM	DESCRIPTION	MANUFACT	MODEL	Q`TY
252	DC-01	DOOR CLOSER NHO	FALCON	SC71A-RW/PA	1 EA
252	DPS-01	DUST PROOF STRIKE	IVES	DP1	1 EA
252	DS-01	FLOOR STOP	IVES	FS436	1 EA
252	FB-02	FLUSH BOLT-12"	IVES	FB458-12-MD	1 EA
252	FB-03	FLUSH BOLT-24"	IVES	FB458-24-MD	1 EA
252	MDL-051	MORTISE LOCKSET-ENTRANCE	SCHLAGE	M56L/SFIC/07B	1 EA
252	MDT-008	MORTISE DUMMY TRIM	SCHLAGE	M172 07B	1 EA
252	PH-03	PIVOT HINGE(OFFSET HUNG)	BRITON	6200-SET-SS	2 SET
252	PH-04	INTERMEDIATE PIVOT HINGE	BRITON	6200-INT-SS	2 EA
253	AFB-01	AUTO FLUSH BOLT	IVES	FB31P-12-MD	1 EA
253	DC-01	DOOR CLOSER NHO	FALCON	SC71A-RW/PA	1 EA
253	DPS-01	DUST PROOF STRIKE	IVES	DP1	1 EA
253	DS-01	FLOOR STOP	IVES	FS436	1 EA
253	MDL-051	MORTISE LOCKSET-ENTRANCE	SCHLAGE	M56L/SFIC/07B	1 EA
253	MDT-008	MORTISE DUMMY TRIM	SCHLAGE	M172 07B	1 EA
253	PH-03	PIVOT HINGE(OFFSET HUNG)	BRITON	6200-SET-SS	2 SET
253	PH-04	INTERMEDIATE PIVOT HINGE	BRITON	6200-INT-SS	2 EA
254	AFB-01	AUTO FLUSH BOLT	IVES	FB31P-12-MD	1 EA
254	DC-01	DOOR CLOSER NHO	FALCON	SC71A-RW/PA	1 EA
254	DPS-01	DUST PROOF STRIKE	IVES	DP1	1 EA
254	DS-01	FLOOR STOP	IVES	FS436	1 EA
254	MDL-051	MORTISE LOCKSET-ENTRANCE	SCHLAGE	M56L/SFIC/07B	1 EA
254	MDT-008	MORTISE DUMMY TRIM	SCHLAGE	M172 07B	1 EA
254	PH-03	PIVOT HINGE(OFFSET HUNG)	BRITON	6200-SET-SS	2 SET
254	PH-04	INTERMEDIATE PIVOT HINGE	BRITON	6200-INT-SS	6 EA
255	AFB-01	AUTO FLUSH BOLT	IVES	FB31P-12-MD	1 EA
255	DC-01	DOOR CLOSER NHO	FALCON	SC71A-RW/PA	1 EA
255	DPS-01	DUST PROOF STRIKE	IVES	DP1	1 EA
255	DS-01	FLOOR STOP	IVES	FS436	1 EA
255	MDL-051	MORTISE LOCKSET-ENTRANCE	SCHLAGE	M56L/SFIC/07B	1 EA
255	MDT-008	MORTISE DUMMY TRIM	SCHLAGE	M172 07B	1 EA
255	PH-03	PIVOT HINGE(OFFSET HUNG)	BRITON	6200-SET-SS	2 SET
255	PH-04	INTERMEDIATE PIVOT HINGE	BRITON	6200-INT-SS	4 EA
260	AFB-01	AUTO FLUSH BOLT	IVES	FB31P-12-MD	1 EA
260	DPS-01	DUST PROOF STRIKE	IVES	DP1	1 EA
260	DS-09	FLOOR STOP	IVES	FS444	1 EA
260	MDL-051	MORTISE LOCKSET-ENTRANCE	SCHLAGE	M56L/SFIC/07B	1 EA
260	MDT-008	MORTISE DUMMY TRIM	SCHLAGE	M172 07B	1 EA
260	SH-10	SPECIAL HINGE	IVES	7237F-SET	2 EA
260	SH-10A	INTERMEDIATE PIVOT	IVES	7230F-7237F INT	4 EA
270	AFB-01	AUTO FLUSH BOLT	IVES	FB31P-12-MD	1 EA
270	CO-07	DOOR COORDINATOR	IVES	COR72	1 EA
270	DC-01	DOOR CLOSER NHO	FALCON	SC71A-RW/PA	2 EA
270	DPS-01	DUST PROOF STRIKE	IVES	DP1	1 EA
270	DS-01	FLOOR STOP	IVES	FS436	2 EA
270	MDL-051	MORTISE LOCKSET-ENTRANCE	SCHLAGE	M56L/SFIC/07B	1 EA
270	MDT-008	MORTISE DUMMY TRIM	SCHLAGE	M172 07B	1 EA
270	PH-03	PIVOT HINGE(OFFSET HUNG)	BRITON	6200-SET-SS	2 SET
270	PH-04	INTERMEDIATE PIVOT HINGE	BRITON	6200-INT-SS	6 EA

HW	ITEM	DESCRIPTION	MANUFACT	MODEL	Q`TY
271	CO-07	DOOR COORDINATOR	IVES	COR72	1 EA
271	DC-01	DOOR CLOSER NHO	FALCON	SC71A-RW/PA	2 EA
271	DPS-01	DUST PROOF STRIKE	IVES	DP1	1 EA
271	DS-01	FLOOR STOP	IVES	FS436	2 EA
271	FB-02	FLUSH BOLT-12"	IVES	FB458-12-MD	2 EA
271	MDL-051	MORTISE LOCKSET-ENTRANCE	SCHLAGE	M56L/SFIC/07B	1 EA
271	MDT-008	MORTISE DUMMY TRIM	SCHLAGE	M172 07B	1 EA
271	PH-03	PIVOT HINGE(OFFSET HUNG)	BRITON	6200-SET-SS	2 SET
271	PH-04	INTERMEDIATE PIVOT HINGE	BRITON	6200-INT-SS	2 EA
280	AP-01	ARMOR PLATE	IVES	8400-42X36"	2 EA
280	BH-49	BUTT HINGE(SST'L) 5"X4"	BRITON	AH500-5X4"	6 EA
280	CO-01	DOOR COORDINATOR	IVES	COR52	1 EA
280	DC-06	DOOR CLOSER NHO	FALCON	SC81A-RW/PA	2 EA
280	DPS-01	DUST PROOF STRIKE	IVES	DP1	1 EA
280	DS-05	WALL BUMPER	IVES	WS401/402CVX	2 EA
280	FB-02	FLUSH BOLT-12"	IVES	FB458-12-MD	2 EA
280	MDL-001	MORTISE DEADLOCK	SCHLAGE	M64L/SFIC	1 SET
280	PP-01	PUSH PULL PLATE	IVES	8302-4X16"	2 EA
400	BH-49	BUTT HINGE(SST'L) 5"X4"	BRITON	AH500-5X4"	3 EA
400	DC-06	DOOR CLOSER NHO	FALCON	SC81A-RW/PA	1 EA
400	DS-01	FLOOR STOP	IVES	FS436	1 EA
400	MDL-054	MORTISE LOCKSET-STOREROOM	SCHLAGE	M80L/SFIC/07B	1 EA
401	BH-49	BUTT HINGE(SST'L) 5"X4"	BRITON	AH500-5X4"	4 EA
401	DC-06	DOOR CLOSER NHO	FALCON	SC81A-RW/PA	1 EA
401	DS-01	FLOOR STOP	IVES	FS436	1 EA
401	MDL-054	MORTISE LOCKSET-STOREROOM	SCHLAGE	M80L/SFIC/07B	1 EA
500	DH-35	PUSH PULL HANDLE	ZERO	UNO G5955-01-024	1 SET
500	FH-07	FLOOR HINGE	CISA	F8500-AB	1 EA
500	PF-10	BOTTOM FITTING	CISA	PF10-12-SS-G	1 EA
500	PF-12	TOP FITTING	CISA	PF20-12-SS	1 EA
501	DH-35	PUSH PULL HANDLE	ZERO	UNO G5955-01-024	1 SET
501	FH-07	FLOOR HINGE	CISA	F8500-AB	1 EA
502	DH-35	PUSH PULL HANDLE	ZERO	UNO G5955-01-024	1 SET
502	FH-07	FLOOR HINGE	CISA	F8500-AB	1 EA
502	GDL-01	GLASS DEADLOCK	Adans Rite	MS1850/SFIC/4066	1 EA
502	PF-10	BOTTOM FITTING	CISA	PF10-12-SS-G	1 EA
502	PF-12	TOP FITTING	CISA	PF20-12-SS	1 EA
503	DH-35	PUSH PULL HANDLE	ZERO	UNO G5955-01-024	1 SET
503	DPS-01	DUST PROOF STRIKE	IVES	DP1	1 EA
503	FH-07	FLOOR HINGE	CISA	F8500-AB	1 EA
503	PF-06	PATCH LOCK	CISA	PL10-12-SS-CY	1 SET
503	PF-10	BOTTOM FITTING	CISA	PF10-12-SS-G	1 EA
503	PF-12	TOP FITTING	CISA	PF20-12-SS	1 EA
510	DH-35	PUSH PULL HANDLE	ZERO	UNO G5955-01-024	1 SET
510	DPS-01	DUST PROOF STRIKE	IVES	DP1	1 EA
510	FH-07	FLOOR HINGE	CISA	F8500-AB	1 EA
510	PF-06	PATCH LOCK	CISA	PL10-12-SS-CY	1 SET
510	PF-10	BOTTOM FITTING	CISA	PF10-12-SS-G	1 EA
510	PF-12	TOP FITTING	CISA	PF20-12-SS	1 EA
510	PF-13	TRANSOM FITTING WITH PIVOT	CISA	PF40-12-SS	1 EA

KEY PLAN

NOTE

REV.	DESCRIPTION	DRAWN	DATE
1	CD Rev.1	OH.J.S	2025. 02.14
0	CONSTRUCTION DRAWING	OH.J.S	2024. 09.30

CLIENT

HYUNDAI

ARCHITECTS & ENGINEERS

JUNGLIM ARCHITECTURE

PROJECT TITLE

PUNE HMI PROJECT

DRAWING TITLE

[MAIN GATE]
DOOR HARDWARE LIST-2

SCALE	DRAWN	CHECKED	REVIEWED	APPROVED	APPROVED
A1:1/NONE A3:1/NONE	OH.J.S	HONG.G.D	LEE.S.L	HEC INDIA	PARK.T.S
DATE					
14 FEB,2025					

MAIN CONTRACTOR

HEC HANLIM

DRAWING NO. WA-IPB-640-A-6103

REV. 1

A1 SIZE (841mm x 594mm)

HW	ITEM	DESCRIPTION	MANUFACT	MODEL	Q`TY
512	BDL-01	BOTTOM RAIL DEADLOCK	ADAMS RITE	MS1861/SFIC/4066	1 SET
512	DH-35	PUSH PULL HANDLE	ZERO	UNO G5955-01-024	1 SET
512	DPS-01	DUST PROOF STRIKE	IVES	DP1	1 EA
512	FH-07	FLOOR HINGE	CISA	F8500-AB	1 EA
516	BDL-01	BOTTOM RAIL DEADLOCK	ADAMS RITE	MS1861/SFIC/4066	1 SET
516	DH-35	PUSH PULL HANDLE	ZERO	UNO G5955-01-024	1 SET
516	DPS-01	DUST PROOF STRIKE	IVES	DP1	1 EA
516	FH-07	FLOOR HINGE	CISA	F8500-AB	1 EA
516	PF-12	TOP FITTING	CISA	PF20-12-SS	1 EA
516	PF-13	TRANSOM FITTING WITH PIVOT	CISA	PF40-12-SS	1 EA
600	BDL-01	BOTTOM RAIL DEADLOCK	ADAMS RITE	MS1861/SFIC/4066	2 SET
600	DH-35	PUSH PULL HANDLE	ZERO	UNO G5955-01-024	2 SET
600	DPS-01	DUST PROOF STRIKE	IVES	DP1	2 EA
600	FH-07	FLOOR HINGE	CISA	F8500-AB	2 EA
601	BDL-01	BOTTOM RAIL DEADLOCK	ADAMS RITE	MS1861/SFIC/4066	2 SET
601	DH-35	PUSH PULL HANDLE	ZERO	UNO G5955-01-024	2 SET
601	DPS-01	DUST PROOF STRIKE	IVES	DP1	2 EA
601	FH-08	FLOOR HINGE	CISA	F5500-AB	2 EA
611	BDL-01	BOTTOM RAIL DEADLOCK	ADAMS RITE	MS1861/SFIC/4066	2 SET
611	DH-35	PUSH PULL HANDLE	ZERO	UNO G5955-01-024	2 SET
611	DPS-01	DUST PROOF STRIKE	IVES	DP1	2 EA
611	FH-07	FLOOR HINGE	CISA	F8500-AB	2 EA
611	PF-12	TOP FITTING	CISA	PF20-12-SS	2 EA
611	PF-13	TRANSOM FITTING WITH PIVOT	CISA	PF40-12-SS	2 EA
620	BDL-01	BOTTOM RAIL DEADLOCK	ADAMS RITE	MS1861/SFIC/4066	2 SET
620	DH-05	PUSH PULL HANDLE	ZERO	UNO T67	2 SET
620	DPS-01	DUST PROOF STRIKE	IVES	DP1	2 EA
620	FH-08	FLOOR HINGE	CISA	F5500-AB	2 EA
623	BDL-01	BOTTOM RAIL DEADLOCK	ADAMS RITE	MS1861/SFIC/4066	2 SET
623	DH-35	PUSH PULL HANDLE	ZERO	UNO G5955-01-024	2 SET
623	DPS-01	DUST PROOF STRIKE	IVES	DP1	2 EA
623	FH-08	FLOOR HINGE	CISA	F5500-AB	2 EA
700	DH-02	PUSH PULL HANDLE	ZERO	UNO PH001SS	1 SET
700	SDH-31	SLIDING DAMPING SET	BRIO	QR120S-S1PK W/ 120SCT	1 EA
700	SDL-01	SLIDING DOOR LOCK	ADAMS RITE	MS1890/SFIC/4066	1 SET
700	SDT-01	SLIDING DOOR TRACK-2M	BRIO	120F-2M	1 EA
701	DH-02	PUSH PULL HANDLE	ZERO	UNO PH001SS	1 SET
701	SDH-31	SLIDING DAMPING SET	BRIO	QR120S-S1PK W/ 120SCT	1 EA
701	SDT-02	SLIDING DOOR TRACK-3M	BRIO	120F-3M	1 EA
⚠1 250205 발주처 변경 요청: 도어 스팩 추가					
521	BDL-01	BOTTOM RAIL DEADLOCK	ADAMS RITE	MS1861/SFIC/4066	1 SET
521	DH-01	PUSH PULL HANDLE	ZERO	UNO T5955-01-024	1 SET
521	DPS-01	DUST PROOF STRIKE	IVES	DP1	1 EA
521	FH-07	FLOOR HINGE	CISA	F8500-AB	1 EA

HW	ITEM	DESCRIPTION	MANUFACT	MODEL	Q`TY

KEY PLAN

NOTE

REV.	DESCRIPTION	DRAWN	DATE
⚠1	CD Rev.1	OH.J.S	2025. 02.14
⚠0	CONSTRUCTION DRAWING	OH.J.S	2024. 09.30

CLIENT

HYUNDAI

ARCHITECTS & ENGINEERS

JUNGLIM ARCHITECTURE

PROJECT TITLE

PUNE HMI PROJECT

DRAWING TITLE

[MAIN GATE]
DOOR HARDWARE LIST-3

SCALE A1:1/NONE A3:1/NONE	DRAWN	CHECKED	REVIEWED	APPROVED	APPROVED
DATE	OH.J.S	HONG.G.D	LEE.S.L	HEC INDIA	PARK.T.S
14 FEB,2025					

MAIN CONTRACTOR

HEC HANLIM

DRAWING NO. WA-IPB-640-A-6104

REV. 1

A1 SIZE (841mm x 594mm)

구 분	AUTO FLUSH BOLT	ARMOR PLATE	BOTTOM RAIL DEADLOCK	BUTT HINGE(SST'L) 5"X4"	BUTT HINGE(SST'L) 4"X4"	DIGITAL LOCK	PUSH PULL PLATE	⚠1 250205 발주처 변경 요청: 도어 스팩 추가		
모 델	FB31P-12-MD	8400-42X36"	MS1861/SFIC/4066	AH500-5X4"	AH500-4X4"	S-8100	8302-4X16"			
제조업체	IVES	IVES	ADAMS RITE	BRITON	BRITON	SCHLAGE	IVES			
비 고	AFB-01	AP-01	BDL-01	BH-49	BH-56	CK-05	PP-01			
구 분	DOOR CLOSER NHO	DOOR CLOSER NHO	FLOOR STOP	WALL BUMPER	FLOOR STOP	FLUSH BOLT-12"/24"	DUST PROOF STRIKE	PUSH PULL HANDLE	PUSH PULL HANDLE	PUSH PULL HANDLE
모 델	SC71A-RW/PA	SC81A-RW/PA	FS436	WS401/402CVX	FS444	FB458-MD	DP1	UNO T5955-01-024	UNO G5955-01-024	UNO PH001SS
제조업체	FALCON	FALCON	IVES	IVES	IVES	IVES	IVES	ZERO	ZERO	ZERO
비 고	DC-01	DC-06	DS-01	DS-05	DS-09	FB-02, 03	DPS-01	DH-01	DH-35	DH-02
구 분	FLOOR HINGE	FLOOR HINGE	GLASS DEADLOCK	MORTISE DEADLOCK	MORTISE LOCKSET-PASSAGE	MORTISE LOCKSET-ENTRANCE	MORTISE LOCKSET-CLASSROOM	MORTISE LOCKSET-STOREROOM	MORTISE DUMMY TRIM	
모 델	F8500-AB	F5500-AB	MS1850/SFIC/4066	M64L/SFIC	M10 07B	M56L/SFIC/07B	M70L/SFIC/07B	M80L/SFIC/07B	M172 07B	
제조업체	CISA	CISA	Adans Rite	SCHLAGE	SCHLAGE	SCHLAGE	SCHLAGE	SCHLAGE	SCHLAGE	
비 고	FH-07	FH-08	GDL-01	MDL-001	MDL-049	MDL-051	MDL-053	MDL-054	MDT-008	
구 분	PATCH LOCK	BOTTOM FITTING	TOP FITTING	TRANSOM FITTING WITH PIVOT	PIVOT HINGE(OFFSET HUNG)	INTERMEDIATE PIVOT HINGE	SLIDING DAMPING SET	SLIDING DOOR LOCK	SLIDING DOOR TRACK-2M	PUSH PULL HANDLE
모 델	PL10-12-SS-CY	PF10-12-SS-G	PF20-12-SS	PF40-12-SS	6200-SET-SS	6200-INT-SS	QR120S-S1PK W/ 120SCT	MS1890/SFIC/4066	120F-2M	UNO T67
제조업체	CISA	CISA	CISA	CISA	BRITON	BRITON	BRIO	ADAMS RITE	BRIO	ZERO
비 고	PF-06	PF-10	PF-12	PF-13	PH-03	PH-04	SDH-31	SDL-01	SDT-01	DH-05
구 분	SLIDING DOOR TRACK-3M	SPECIAL HINGE	INTERMEDIATE PIVOT	DOOR COORDINATOR						
모 델	120F-3M	7237F-SET	7230F-7237F INT	COR Serise						
제조업체	BRIO	IVES	IVES	IVES						
비 고	SDT-02	SH-10	SH-10A	CO-01, 07						

KEY PLAN

NOTE

REV.	DESCRIPTION	DRAWN	DATE
1	CD Rev.1	OH.J.S	2025. 02.14
0	CONSTRUCTION DRAWING	OH.J.S	2024. 09.30

CLIENT

HYUNDAI

ARCHITECTS & ENGINEERS

JUNGLIM ARCHITECTURE

PROJECT TITLE

PUNE HMI PROJECT

DRAWING TITLE

[MAIN GATE]
DOOR HARDWARE LIST-4

SCALE A1:1/NONE A3:1/NONE	DRAWN	CHECKED	REVIEWED	APPROVED	APPROVED
	OH.J.S	HONG.G.D	LEE.S.L	HEC INDIA	PARK.T.S
DATE 14 FEB,2025					


MAIN CONTRACTOR

HEC INDIA LLP

DRAWING NO. WA-IPB-640-A-6105


REV. 1

A1 SIZE (841mm x 594mm)

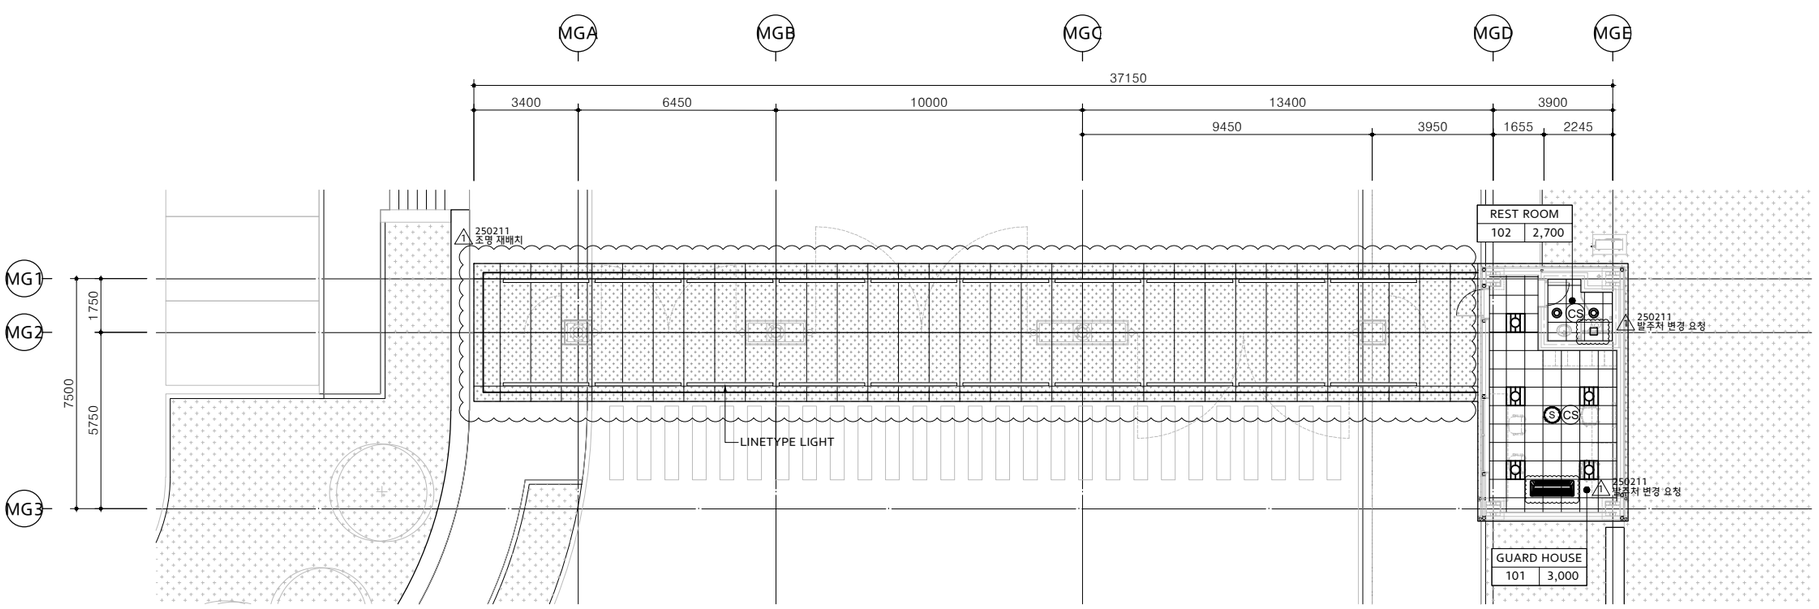

1 GROUND FLOOR CEILING PLAN

SCALE : 1/100

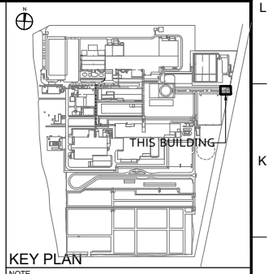

KEY PLAN

NOTE

1. GROUND FLOOR LEVEL
   -GROUND FLOOR FL ±0.00 = EL+663.20

2. LEVEL(T.O.C) OF GROUND FLOOR, WHICH IS THE BASE LEVEL OF ALL LEVEL DIMENSIONS.

3. THIS DRAWING SHOULD BE APPROVED BY HEC & HMI BEFORE APPLICATION

4. REFER TO DRAWING NUMBER "000-G-0001~0900" FOR GENERAL NOTES AND STANDARDS DETAIL.

5. SITE SURVEY FOR THIS DRAWING SHALL BE REQUIRED AND SUPERVISOR'S APPROVAL SHALL BE OBTAINED PRIOR TO CONSTRUCTION.

6. IF THE DRAWING IS DIFFERENT FROM CURRENT SITE, SUPERVISORS AND DESIGNER'S APPROVAL SHALL BE OBTAINED PRIOR TO CONSTRUCTION.

7. STRUCTURES IN THE BUILDING SHOULD BE ALKYD ENAMEL PAINT ON ANTI- RUST PAINT.

8. ALL SEALANT SHALL BE SUBMITTED TO THE MANUFACTURING ENGINEERING TEAM AND APPROVED PRIOR TO THE INSTALLATION BY THEM.

*LEGEND

: AL. SHEET

: ACOUSTIC CEILING TILE

: LINE TYPE LIGHT

■ CEILING FIXTURE LEGEND-E

SYMBOL	DESCRIPTION
	LED 1/40W
	LED 1/15W

■ CEILING FIXTURE LEGEND-M

SYMBOL	DESCRIPTION
	EHP (1WAY-TYPE)
	CEILING FAN

250211 방주저 변경 요청

■ CEILING FIXTURE LEGEND-F

SYMBOL	DESCRIPTION
S	COMBINATION DETECTOR 57° C
CS	3 WATT CEILING SPEAKER

REV.	DESCRIPTION	DRAWN	DATE
1	CD Rev.1	OH.J.S	2025.02.14
0	CONSTRUCTION DRAWING	OH.J.S	2024.11.29

CLIENT

HYUNDAI

ARCHITECTS & ENGINEERS

JUNGLIM ARCHITECTURE

PROJECT TITLE

PUNE HMI PROJECT

DRAWING TITLE

[MAIN GATE]
GROUND FLOOR CEILING PLAN

SCALE	DRAWN	CHECKED	REVIEWED	APPROVED	APPROVED
A1:1/30 A3:1/60	OH.J.S	HONG.G.D	LEE.S.L	HEC INDIA	PARK.T.S
DATE					
14 FEB 2025					


MAIN CONTRACTOR

HEC INDIA LLP


DRAWING NO. WA-IPB-640-A-7001

REV. 1


A1 SIZE (841mm x 594mm)

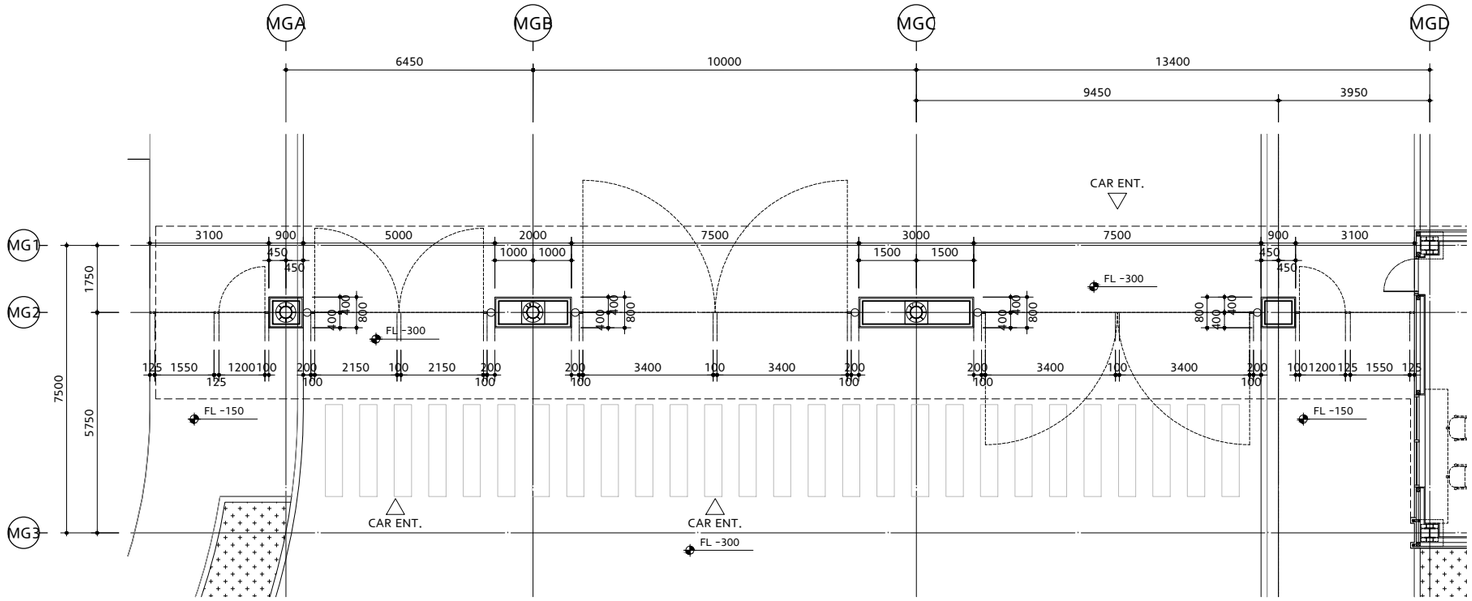


1 DOOR PLAN
SCALE : 1/80

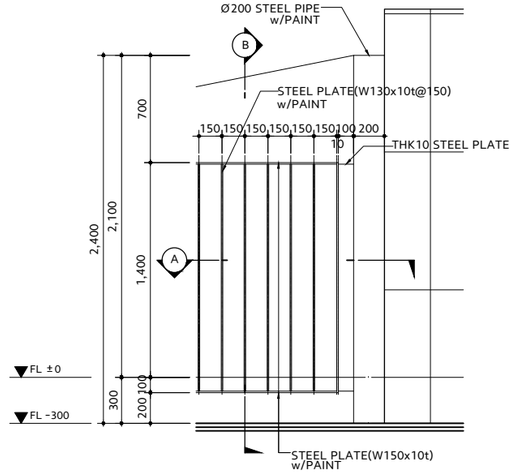


3 DETAIL-1
SCALE : NONE

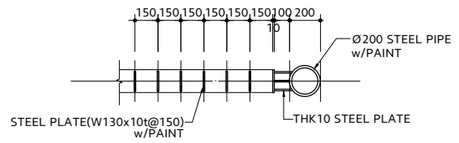

4 SECTION-A
SCALE : NONE

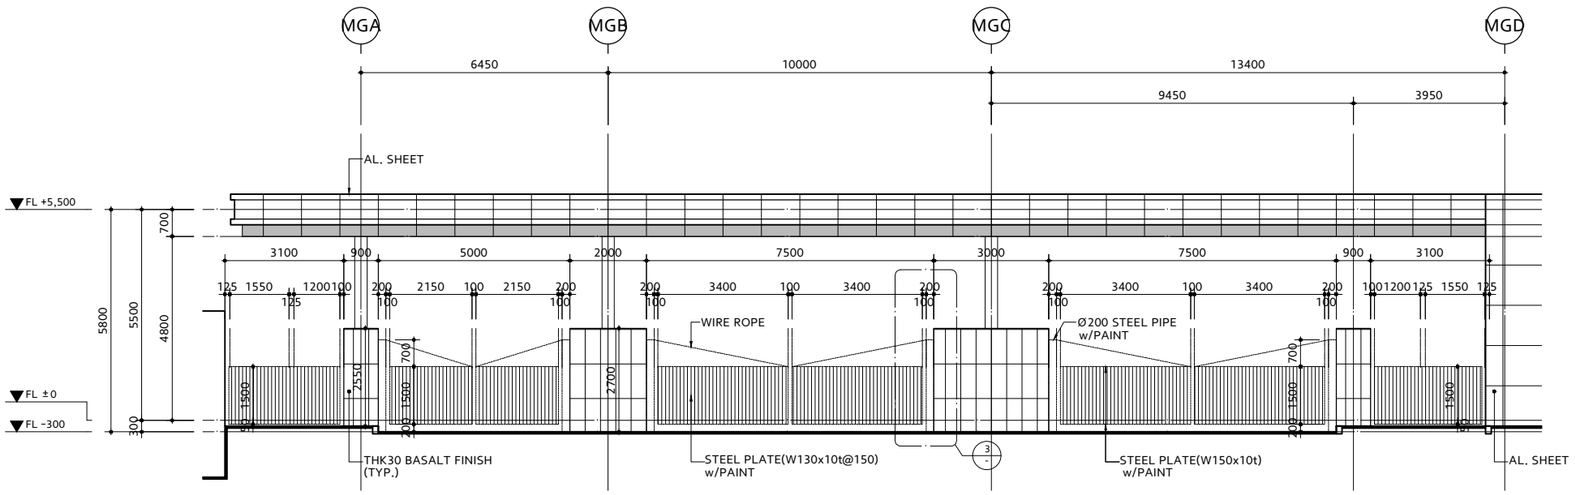

2 DOOR ELEVATION
SCALE : 1/80

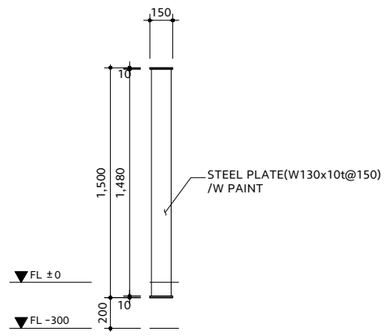

5 SECTION-B
SCALE : NONE

KEY PLAN

NOTE

1. GROUND FLOOR LEVEL
   -GROUND FLOOR FL±0.00 = EL+663.20
2. LEVEL(T.O.C) OF GROUND FLOOR, WHICH IS THE BASE LEVEL OF ALL LEVEL DIMENSIONS.
3. THIS DRAWING SHOULD BE APPROVED BY HEC & HMI BEFORE APPLICATION
4. REFER TO DRAWING NUMBER "000-G-0001~0900" FOR GENERAL NOTES AND STANDARDS DETAIL.
5. SITE SURVEY FOR THIS DRAWING SHALL BE REQUIRED AND SUPERVISOR'S APPROVAL SHALL BE OBTAINED PRIOR TO CONSTRUCTION.
6. IF THE DRAWING IS DIFFERENT FROM CURRENT SITE, SUPERVISORS AND DESIGNER'S APPROVAL SHALL BE OBTAINED PRIOR TO CONSTRUCTION.
7. STRUCTURES IN THE BUILDING SHOULD BE ALKYD ENAMEL PAINT ON ANTI- RUST PAINT.
8. ALL SEALANT SHALL BE SUBMITTED TO THE MANUFACTURING ENGINEERING TEAM AND APPROVED PRIOR TO THE INSTALLATION BY THEM.

REV.	DESCRIPTION	DRAWN	DATE
0	CONSTRUCTION DRAWING	OH.J.S	2025. 02.14

CLIENT: HYUNDAI

ARCHITECTS & ENGINEERS: JUNGLIM ARCHITECTURE

PROJECT TITLE: PUNE HMI PROJECT

DRAWING TITLE: [MAIN GATE] ENTRANCE DOOR DETAIL

SCALE	DRAWN	CHECKED	REVIEWED	APPROVED	APPROVED
A1:1/80 A3:1/160	OH.J.S	HONG.G.D	LEE.S.L	HEC INDIA	PARK.T.S
DATE: 14 FEB.2025					

MAIN CONTRACTOR: HEC

DRAWING NO.: WA-IPB-640-A-7601

REV.: 0

A1 SIZE (841mm x 594mm)