


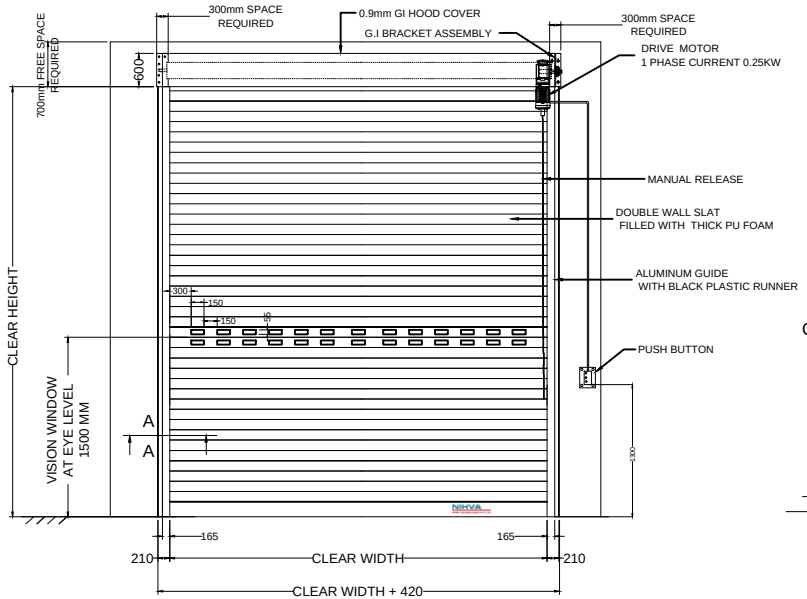


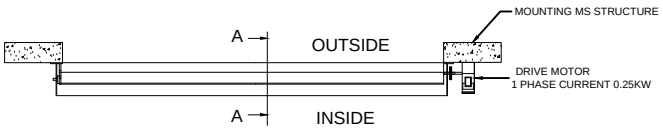

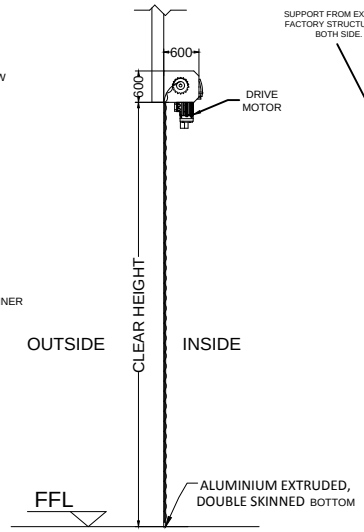

Section A-A

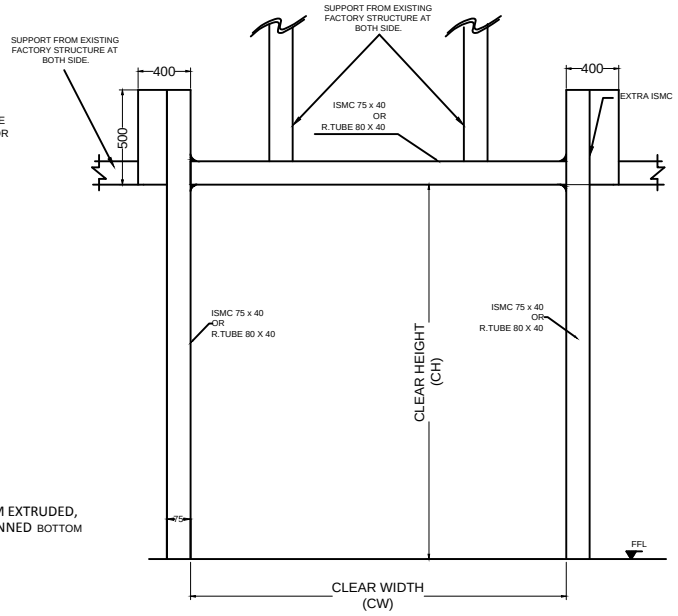


STRUCTURE

CLIENT SCOPE

1) 16A 3 PIN INDUSTRIAL TYPE FEMALE SOCKET 230V, 50HZ, WITH EARTH AROUND 1/2 METER FROM CONTROLLER/OPERATOR.

5000 mm	4500 mm	1 NO
CLEAR WIDTH	CLEAR HEIGHT	QUANTITY

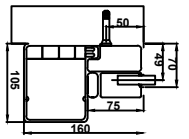


SECTION DETAIL

MAIN SLATS

DOUBLE WALL ROLLING SHUTTER



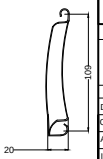

STANDARD COLOR OF SLATS & SHUTTER -RAL9002 (GRAY WHITE)

NOTE : DOOR TO BE FIXED FROM INSIDE ONLY

This drawing & design is the property of NIHVA TECHNOLOGIES. Not to be sold or copied to any other concern.

TITLE	DOUBLE WALL ROLLING SHUTTER	NIHVA TECHNOLOGIES PVT. LTD.	NIHVA TECHNOLOGIES PVT. LTD. PUNE Tel : 020 66304033 Email:- info@nihva.com Website:- www.nihva.com

	NAME	SIGN	DATE	
DRAWN	S.S.		09.10.2020	CLIENT -
CHECK	P.A		09.10.2020	PROJECT -
APPRD.				SITE LOCATION -

If any queries contact : projectsupport @nihva.com	DWG. NO. : NIHVA/20-21/VDR/0070	REV- R00
ALL DIMENSION ARE IN mm	SCALE: NTS	WT: SHEET: