
MAINTENANCE STOPPER

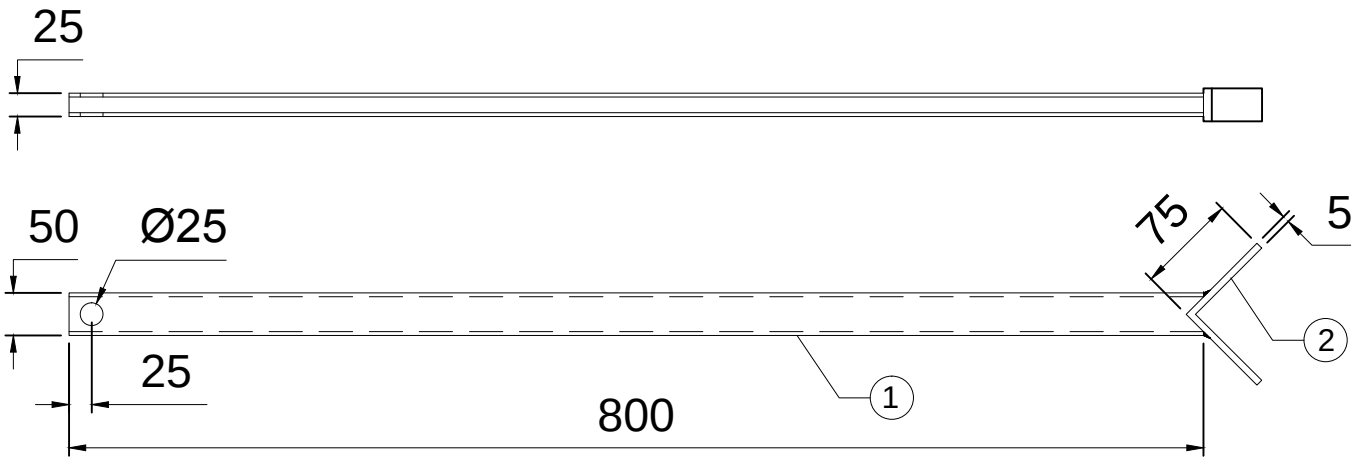

1. SQ .TUBE 50 X 25 X 3 THK X 800L = 2 NOS
2. ISA 75 X 75 X 5 X 35L = 2 NOS

TOLERANCE - ±5mm

This drawing & design is the property of NIHVA TECHNOLOGIES. Not to be sold or copied to any other concern.

TITLE: MAINTENANCE STOPPER DRG				NIHVA TECHNOLOGIES PVT. LTD. PUNE Tel : 020 66304033 Email:- info@nihva.com Website:- www.nihva.com	
	NAME	SIGN	DATE		
DRAWN	P.V.A		20.06.2019	CLIENT -	
CHECK	V.M.T		20.06.2019	PROJECT - NDL451	
APPRD.				SITE LOCATION -	
If any queries contact : design@nihva.com				DWG. NO. : NIHVA/19-20/VDR/081	
ALL DIMENSION ARE IN mm				SCALE: NTS	WT: REV- 0