

PRODUCED BY AN AUTODESK EDUCATIONAL PRODUCT

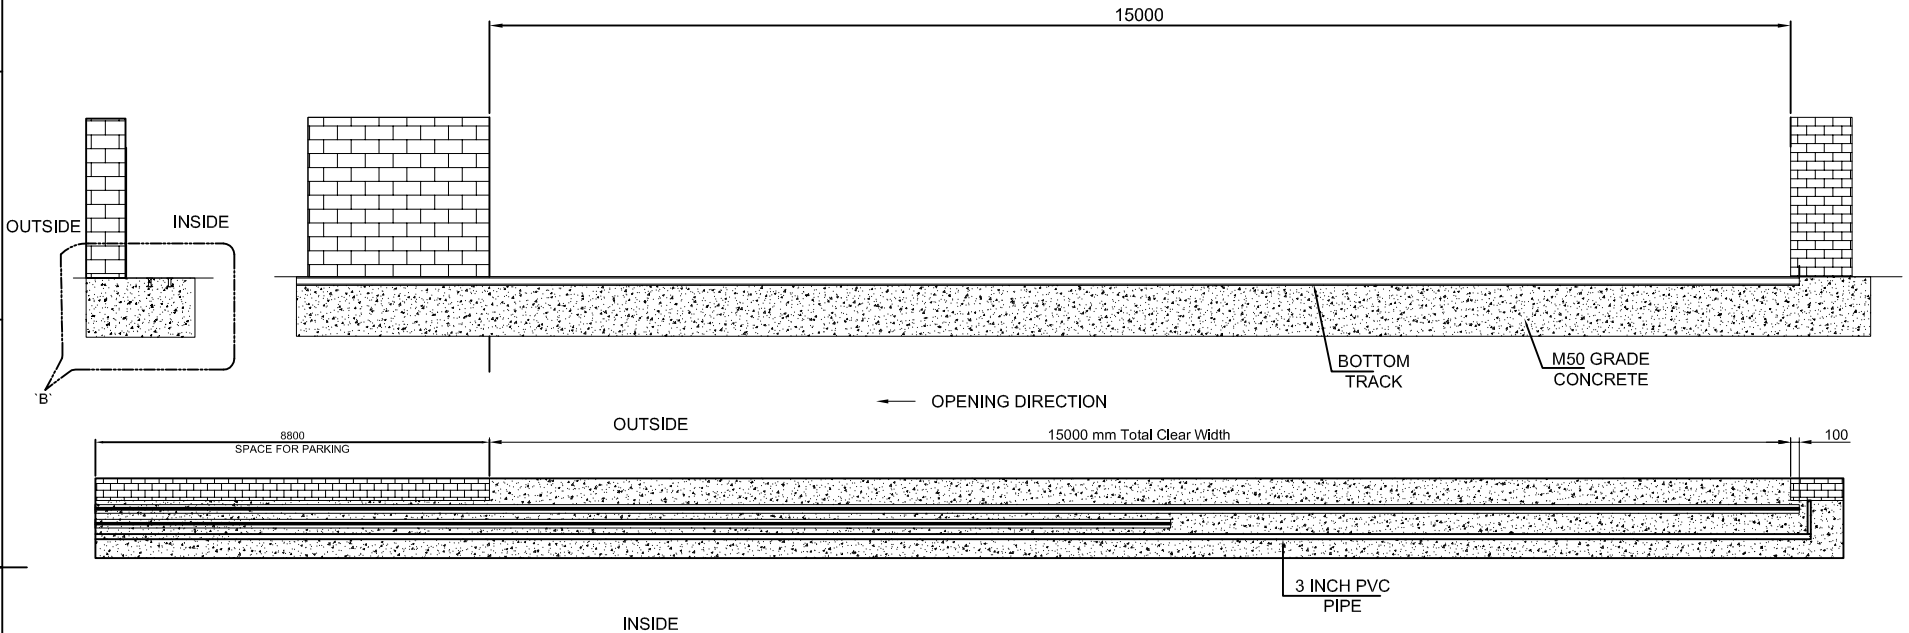

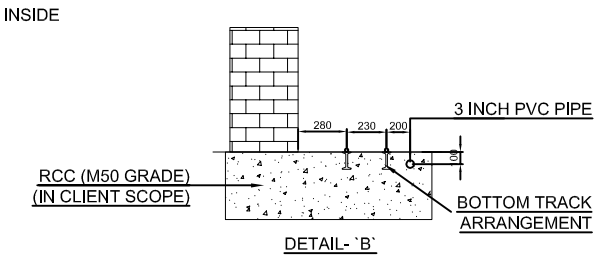

DETAIL- `B`

NOTE-
1. ALL REQUIRED CIVIL WORK WILL BE IN CLIENTS SCOPE.
3.GATE LEAF WILL BE IN TWO PARTS FOR TRANSPORTATION & WILL BE WELD TOGETHER ON SITE.

TOLERANCE - ±10mm

CLEAR WIDTH	CLEAR HEIGHT	QUANTITY
15000	1500	01 NOS

This drawing & design is the property of NIHVA TECHNOLOGIES. Not to be sold or copied to any other concern.

TITLE: FOUNDATION DETAIL DRAWING

	NAME	SIGN	DATE
DRAWN	A.K.		20.04.2019
CHECK	P.A.		20.04.2019
APPRD.	R.D.		20.04.2019

NIHVA TECHNOLOGIES PVT. LTD.
NIHVA TECHNOLOGIES PVT. LTD. PUNE
Tel : 020 66304033
Email:- info@nihva.com
Website:- www.nihva.com

CLIENT - ESR PUNE
PROJECT - WANI PROJECTS
SITE LOCATION - CHAKAN, PUNE.
If any queries contact : design@nihva.com
DWG. NO. : NIHVA/19-20/0008
REV- 00
ALL DIMENSION ARE IN mm
SCALE: NTS
WT:
SHEET: 01 OF 01

PRODUCED BY AN AUTODESK EDUCATIONAL PRODUCT