

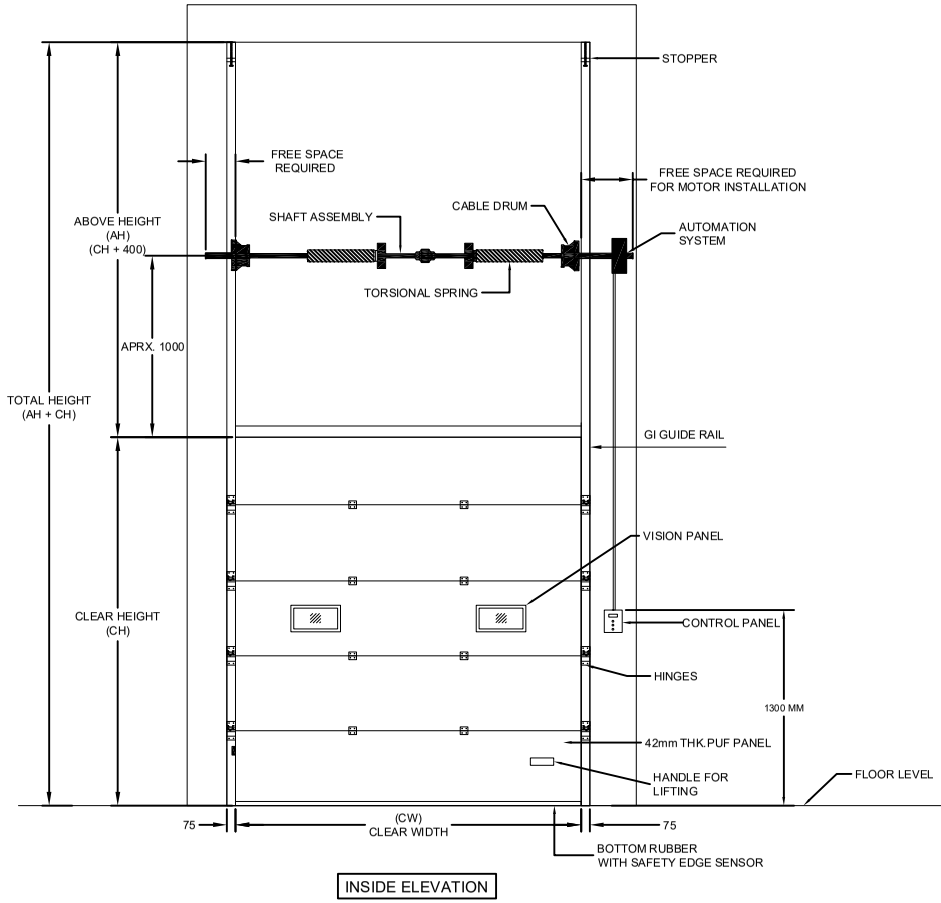



INSIDE ELEVATION

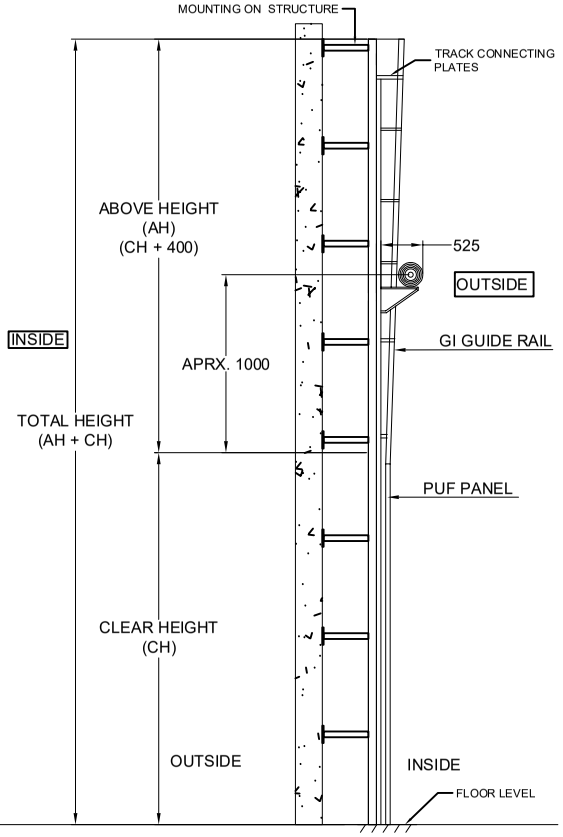


SIDE VIEW

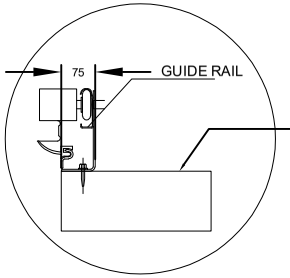

TRACK DETAILS

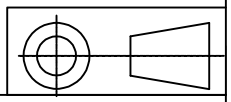

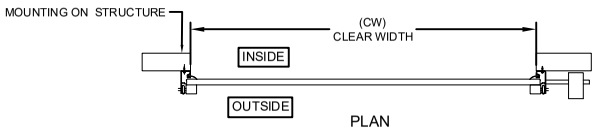

PLAN

Technnical Specifications:

Sr. No	Description	Details
1	Model	Overhead Sectional Door
2	Opening Direction & Mounting	Vertical Lift
3	Opening/Closing Speed	CDM9 0.28 m/s
4	Door Material	Steel
5	Panel Thickness	42 mm
6	Filling	CFC-free polyurethane
7	Door sealent	All door sealants made of EPDM rubber, temperature resistant - 30/+70
8	Water Penetration	EN 12425 class 3
9	Air Permealibity	EN12426 class 3
10	Thermal Transittance	EN 12428 1.10W /m2K
11	Bottom sealing	Bottom of the door to be equiped with three lip sealing made of oil resistant EPDM rubber
12	Door saftey	Doors equiped with spring break device
13	Incase of Power failuer	Doors to be equiped with quick release fuction
14	Operator power conumption	Operator to have a maximum power consumption of 0.37kW and a standby consumption of Maximum 15W
15	Drive Unit & Mounting Type	Single phase 230V direct drive on shaft
16	Emergency Operation	by Disengagement rope manual
17	Operating Switch	Up/Down Keypad + stopbutton
18	Locks : Lock bolt	The Lock bolt locks the door from the inside, without the use of a key. The Lock bolt is not visible from the outside.
19	Accessories	Push Button on both sides

SR.	Description	Clear Width (CW)	Clear Height (CH)	QTY
1.	Overhead Sectional Door	3000	4000	1

IMPORTANT NOTES:
1.SINGLE PHASE POWER SUPPLY REQUIRED AT DOOR LOCATION.
2.ALL CIVIL WORK SHALL BE CLIENT'S SCOPE.
3.REQUIRED STRUCTURE FOR DOOR IS IN CLIENT'S SCOPE.
4.ALL DIMWNSIONS IN MM

NIHVA TECHNOLOGIES PVT. LTD.

NIHVA TECHNOLOGIES PVT. LTD. PUNE
Email:- info@nihva.com
Website:- www.nihva.com

TITLE:

SECTIONAL DOOR - VL

CLIENT'S APPROVAL :

CLIENT - Systematic Conscom Ltd.

PROJECT -

SITE LOCATION -

DWG. NO. : NIHVA/23-24/57

SCALE: NTS	WT:	SHEET:1 OF 1	REV- 0

	NAME	DATE	SIGN
DRAWN	S.J	10-01-2023	
CHECK	A.K.	10-01-2023	
APPROVAL	V.T.	10-01-2023	

If any queries contact : design1@nihva.com

NOTE: ALL DIMENSIONS ARE IN mm

THIS DRAWING & DESIGNING IS THE PROPERTY OF NIHVA TECHNOLOGIES. NOT TO BE SOLD OR COPIED TO ANY OTHER CONCERN.