

Weitergabe sowie Vervielfältigung dieses Dokuments, Verwertung und Mitteilung seines Inhalts sind nur nach vorheriger ausdrücklicher schriftlicher Zustimmung von SMS Meer GmbH gestattet. Das Dokument ist vor unberechtigtem Zugriff Dritter zu schützen. Zuwiderhandlungen verpflichten zu Schadensersatz. Alle Rechte aus Patent-/Gebrauchsmuster-/Markenschutz vorbehalten.

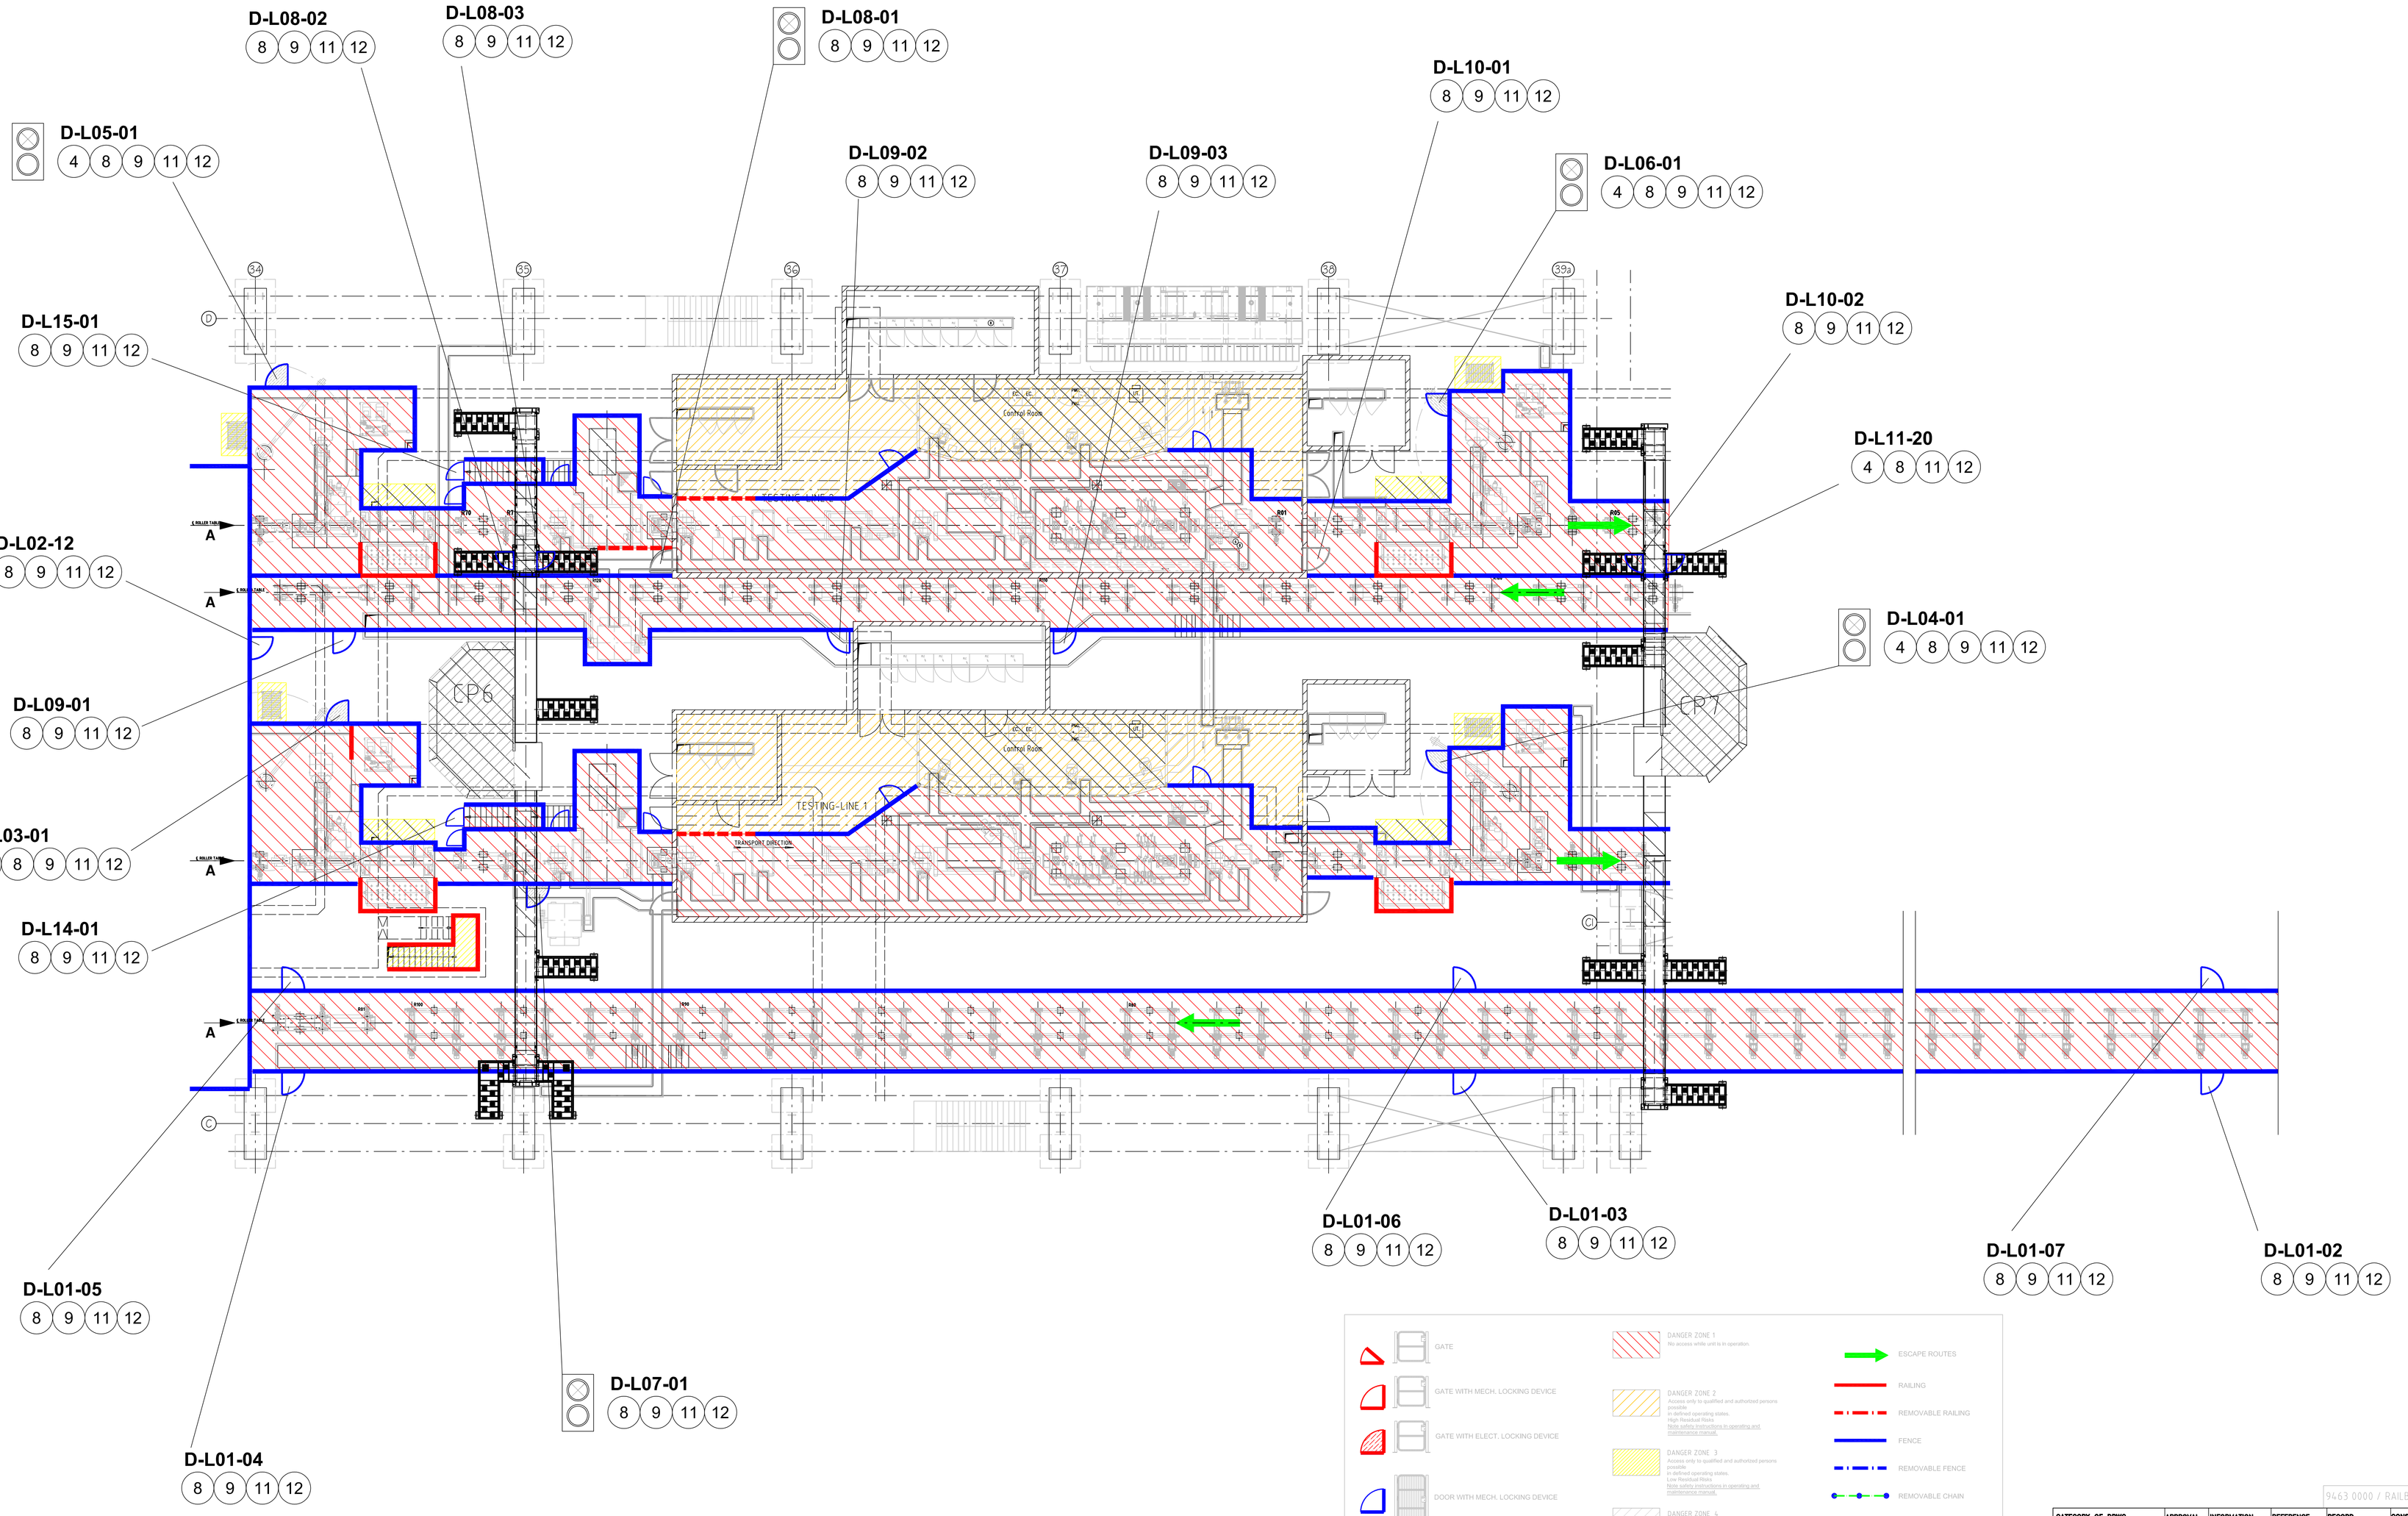

Ansicht (view) A

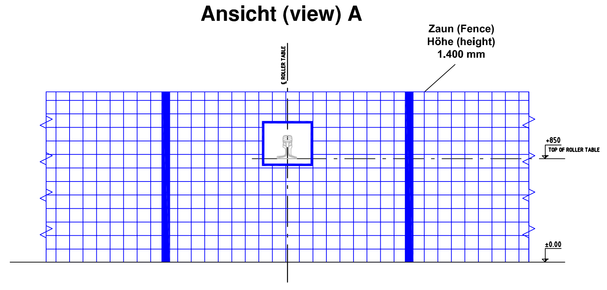

9463 0000 / RAILBHIL

CATEGORY OF DRWG.	APPROVAL	INFORMATION	REFERENCE	RECORD	CONSTRUCTION

BHILAI STEEL PLANT, BHILAI, CHATTISGARH
7,0 MTPA EXPANSION

मेकॉन लिमिटेड
MECON LIMITED

VENSDOR'S NAME:	SMS Meer/SMS Meer India/ABB
PACKAGE DESCRIPTION:	UNIVERSAL RAIL MILL (Pkg No-047)
TITLE OF DRAWING.	PARTITION 10, Safety Layout
SCALE-	
VENDOR'S DRG NO.-	
PROJECT DRG. NO. BSP-SMS Meer-08-047-21-130-35-BE-06657	REV. -

Fertigungsvorschriften / Manufacturing Instructions: SN 200
Ursprung / Origin | Fertiggewicht / Finished weight | Modell-Nr. / Pattern-No.
Werkstoff / Material | kg
Projektionsmethode 1 — First angle projection method ISO 128

	Datum / Date	Name	Typ / Type: Safety Layout	Maßstab / Scale
Bearb. / Drawn	19.09.11	Fryen	Benennung / Title: Teilbereich. 10	1:100
Gepr. / Checked	19.10.11	Prätzel		
Norm / Standard			PARTITION 10	

Sach-Nr. / Drawing-No.: 0100133-00.657
Blatt / Sheet: 1 | 1 Blätter / Sheets
Ersatz für / Supersedes:
Ersetzt durch / Superseded by:

SMS MEER — SMS group

Änderung / Revision	Datum / Date	Name

Diese Zeichnung und alle darauf enthaltenen Informationen sind vertraulich. This drawing and all information on it is confidential.

A0