

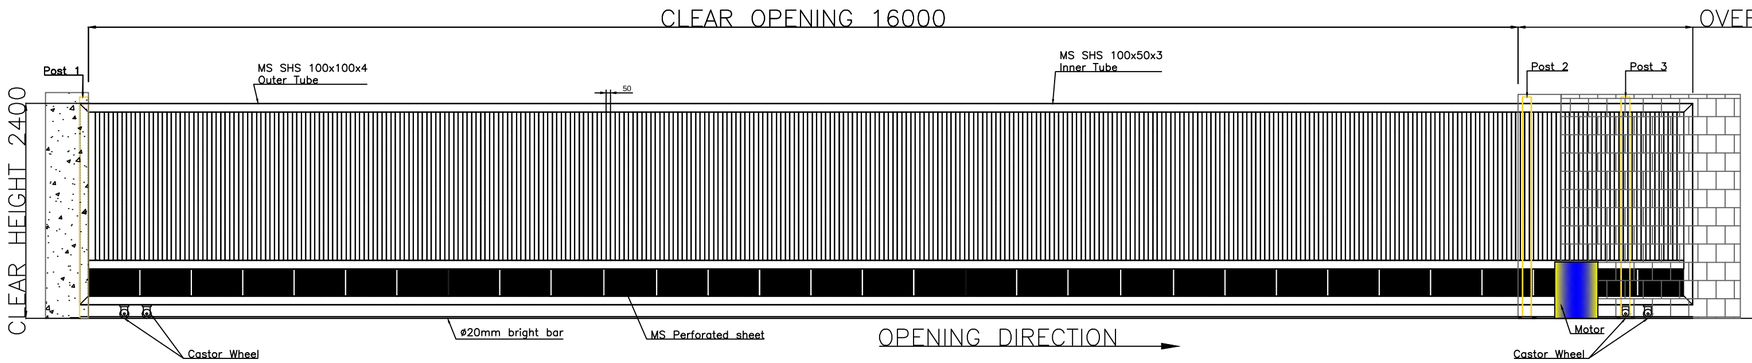



ELEVATION VIEW

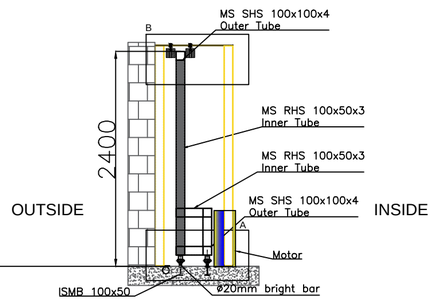


SIDE VIEW

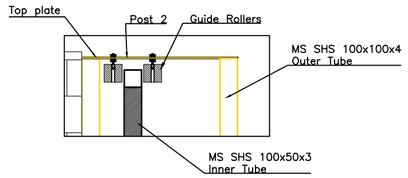

DETAIL B

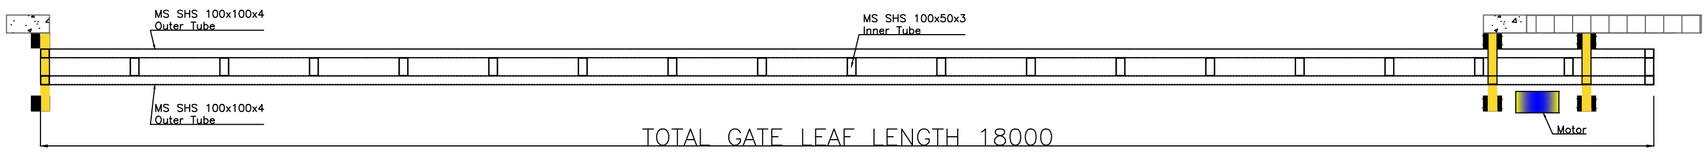

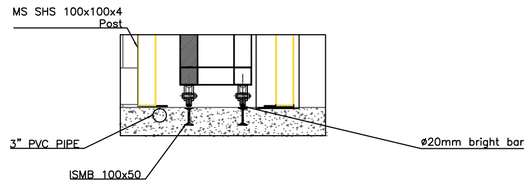

DETAIL A

Technical Specs of Motorized Sliding Gate

1. Opening length - 16000mm
2. Gate Height - 2400mm
3. Parking length required - 18200mm
4. Outer tube size - MS SHS 100x100x4mm
5. Inner tube size - MS RHS 100x50x3mm
6. Bottom Rail - Bright bar Ø20mm
7. Post size - MS SHS 100x100x4mm
8. T`Safety feature - Photocell and flashing light

Note-

1. All dimension are in mm.
2. All civil work is under client scope.
3. 3" PVC pipe in the foundation to be provided by client.

This drawing & design is the property of NIHVA TECHNOLOGIES. Not to be sold or copied to any other concern.

TITLE
MOTORIZED SLIDING GATE

	NAME	SIGN	DATE
DRAWN	G.P.		11.02.22
CHECK	A.K.		11.02.22
APPRD.	V.T.		11.02.22

If any queries contact : design@nihva.com

ALL DIMENSION ARE IN mm

NIHVA
NIHVA TECHNOLOGIES PVT. LTD.

NIHVA TECHNOLOGIES PVT. LTD. PUNE
Tel : 020 66304033
Email:- info@nihva.com
Website:- www.nihva.com

CLIENT - SRF

LOCATION -

PRODUCT - MOTORIZED SLIDING GATE

NIHVA\21-22\CLT\344 | REV- 0

SCALE: NTS | SHEET: 01 OF 01