

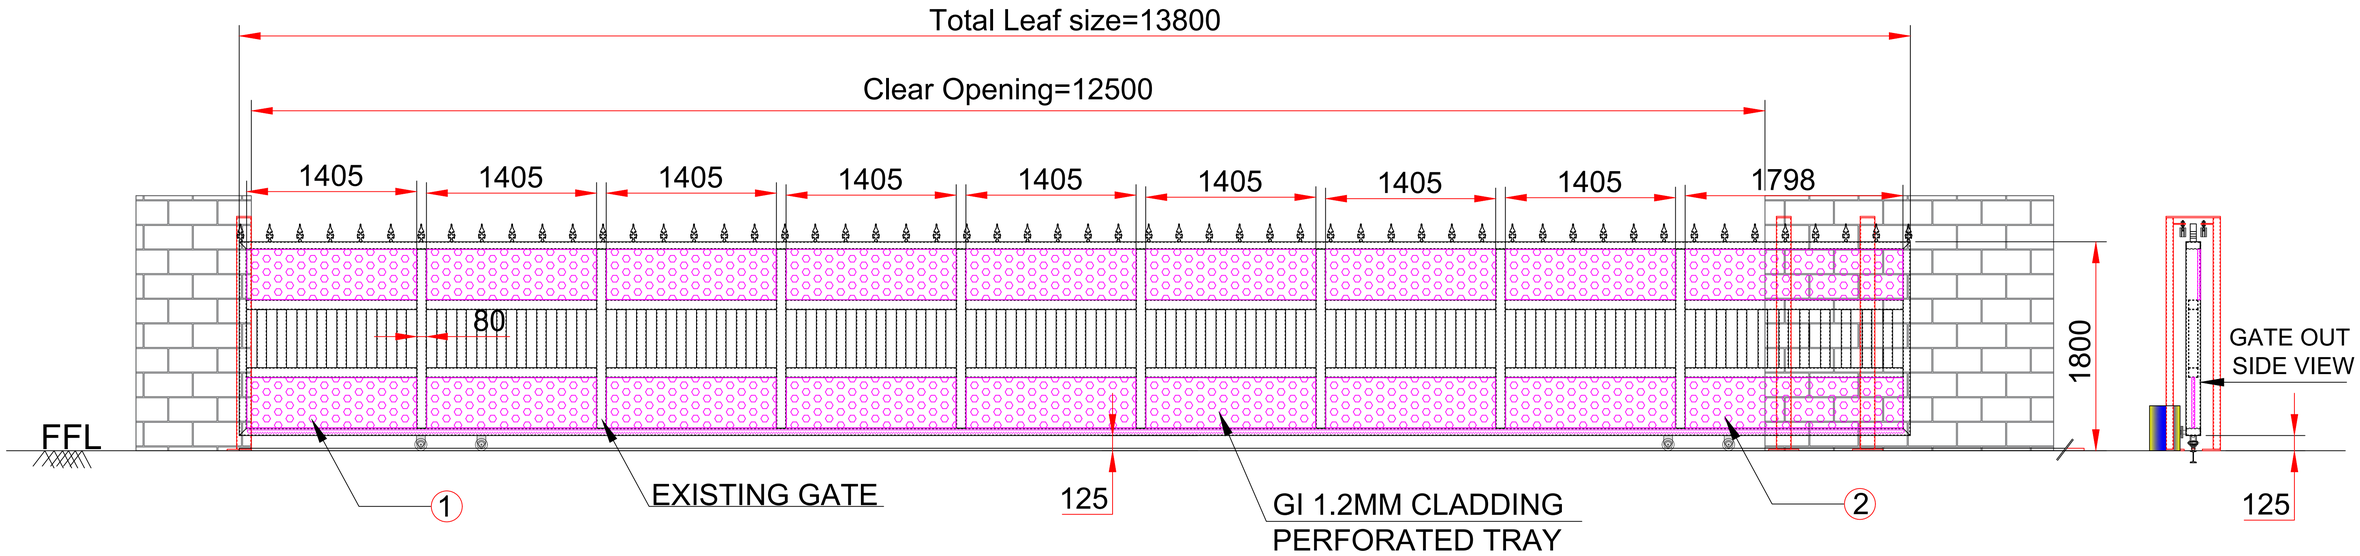


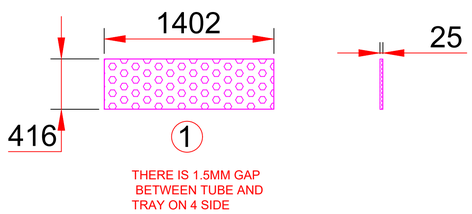

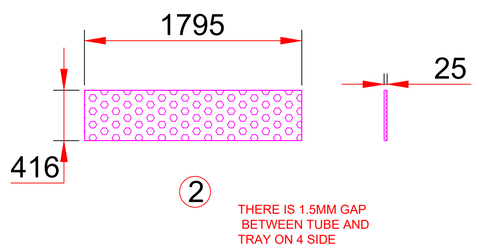

NOTE:-

1. ALL DIMENSION ARE IN MM
2. ABOVE GIVEN DRAWING IS EXISTING GATE WITH CLADDING
3. COPPER FLEXIBLE CABLE 1 Sqmm x 6CORE - 80 MTR (Make – Polycab)
4. THERE IS 1.5MM GAP BETWEEN TUBE AND TRAY ON 4 SIDE

Rev No.	Revision	Date	Revised By
2.	TRAY DETAILS ADDED & PLACED AT THE CENTER OF THE TUBE	07/06/2023	SUJATA
1.	CLADDING TRAY HAS BEEN ADDED AT TOP OF THE GATE	31/05/2023	SUJATA

This drawing & design is the property of NIHVA TECHNOLOGIES. Not to be sold or copied to any other concern.

TITLE:- Automatic Sliding

NIHVA TECHNOLOGIES PVT. LTD.

	NAME	DATE	SIGN
DRAWN	SUJATA	11/05/2023	
CHECK			
APPRD.			

CLIENT - Suraj Buildcon Pvt Ltd

LOCATION - Pune

PRODUCT - Automatic Sliding Gate | QTY-02

If any queries contact : design1@nihva.com | DWG NO:- NIHVA/22-23/CLT/0141_1 | REV-02

ALL DIMENSION ARE IN mm | SCALE: NTS | SCALE:-- 1:1 | SHEET: 01 OF 01