

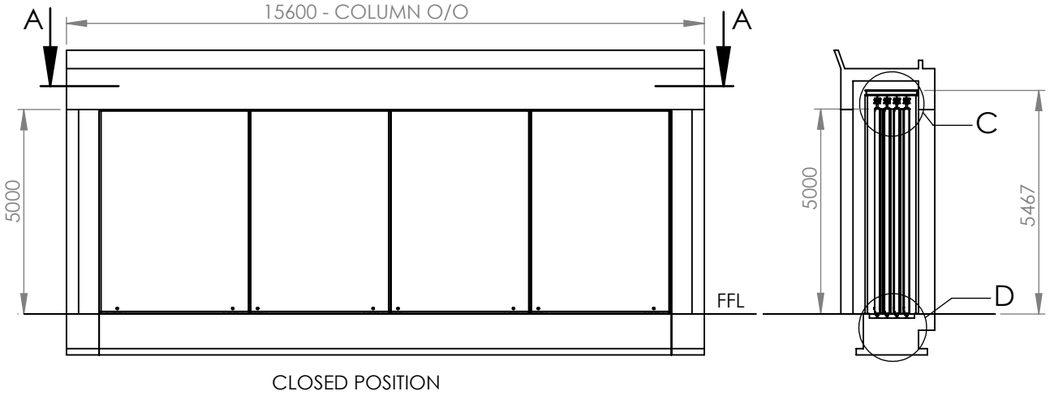



CLOSED POSITION

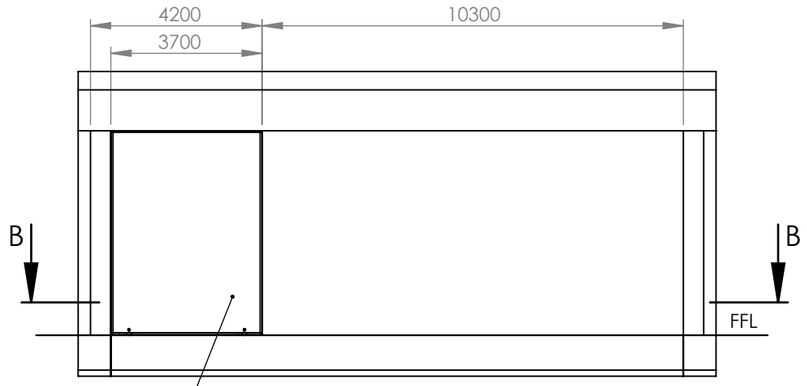


LEFT SIDE STACKING

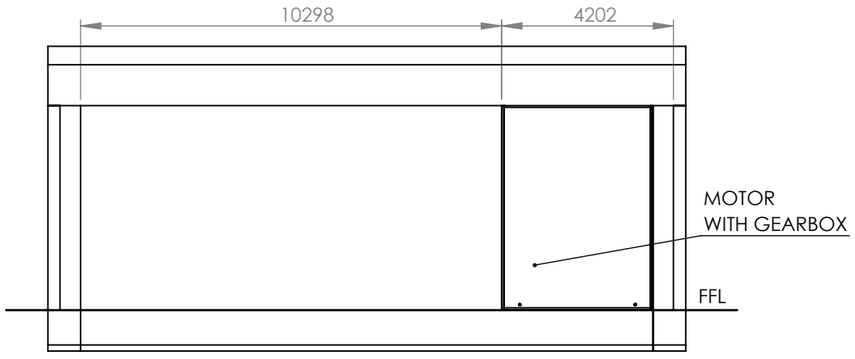

RIGHT SIDE STACKING

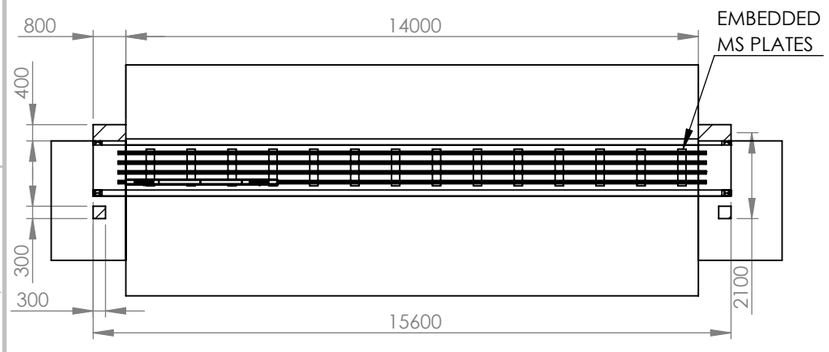


SECTION B-B

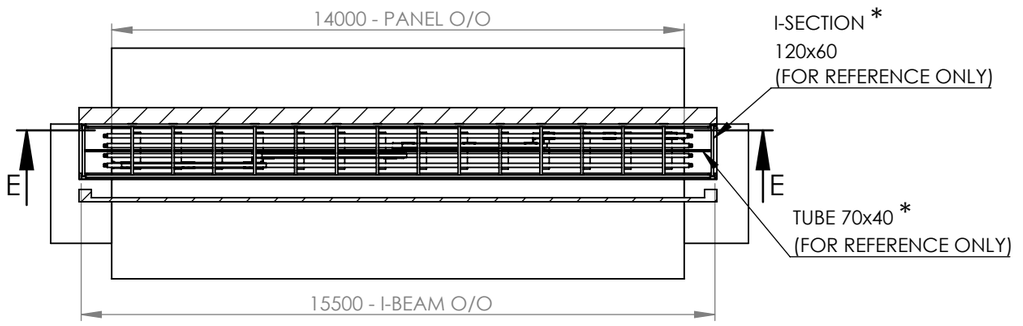


SECTION A-A


* -SUBJECT TO CHANGE AS PER SITE CONDITIONS
-CLIENT SCOPE

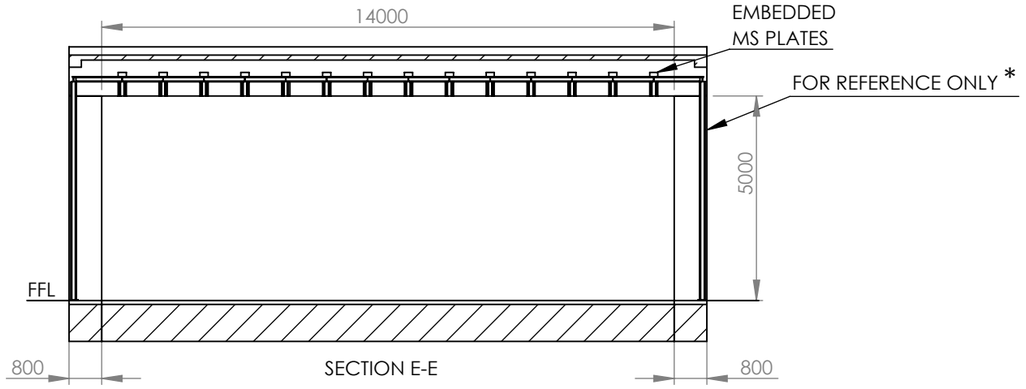


SECTION E-E

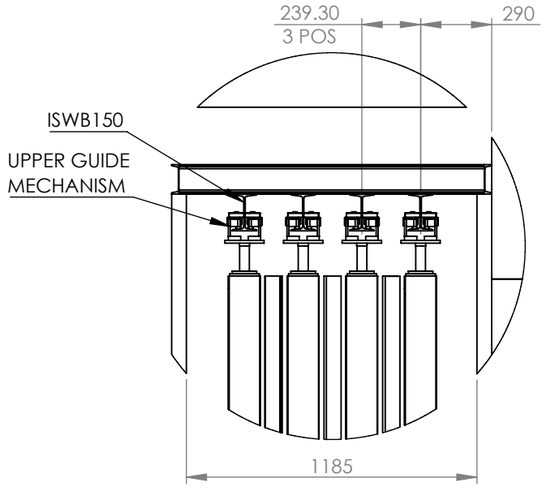

DETAIL C
SCALE 1 : 25

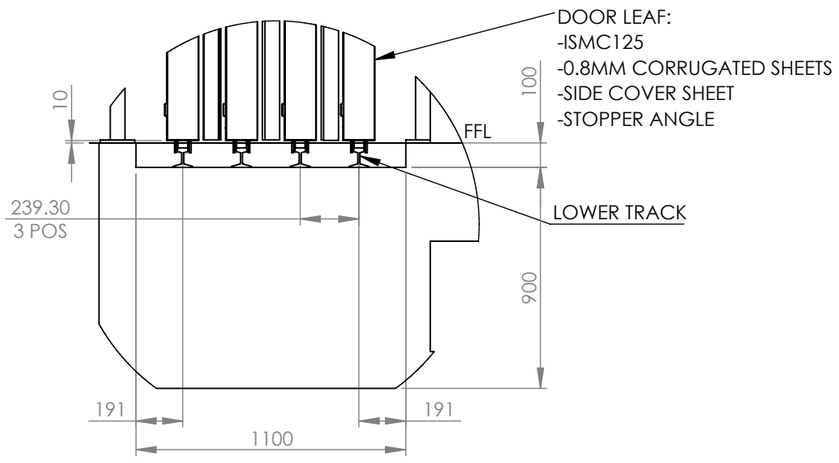

DETAIL D
SCALE 1 : 25

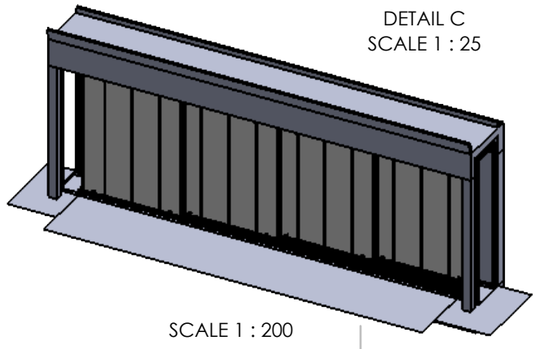

SCALE 1 : 200

TITLE : HANGING SLIDING DOOR

NIHVA Technologies Pvt. Ltd.

NIHVA TECHNOLOGIES PVT LTD

	NAME	SIGN	DATE
DRAWN	BHARATI SABALE		23-12-2024
CHK'D	SURAJ WARALE		23-12-2024
APPV'D	VIJAY T		23-12-2024

DIMENSIONS ARE IN MILLIMETERS

CLIENT NAME : ISRO

PRODUCT NAME : HANGING SLIDING DOOR

SITE LOCATION : ALUVA, KERALA

DWG NO. GA

A3

REVISION : 1

SCALE:

SHEET 1 OF 1