


PRODUCED BY AN AUTODESK EDUCATIONAL PRODUCT

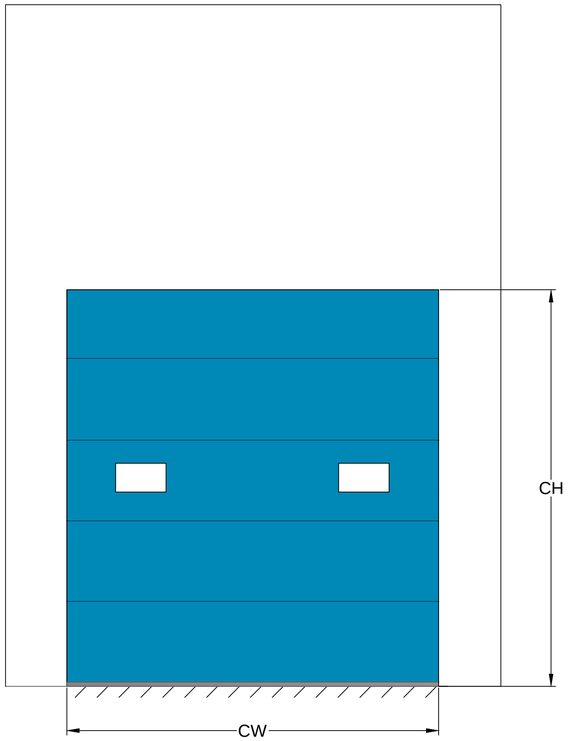


OUTSIDE ELEVATION

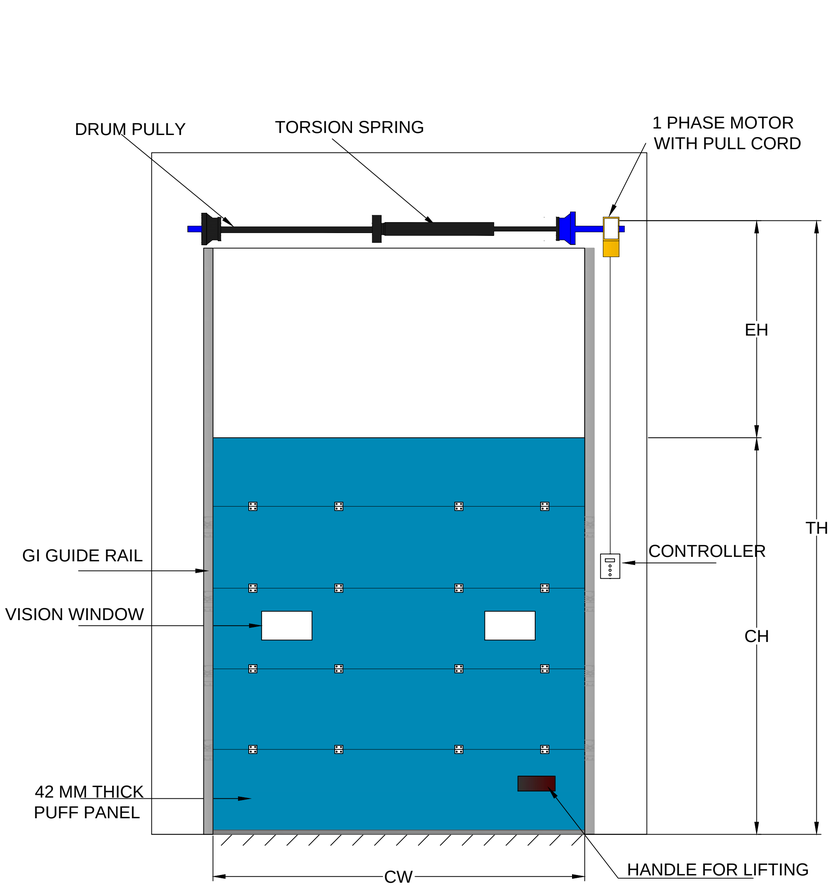


INSIDE ELEVATION

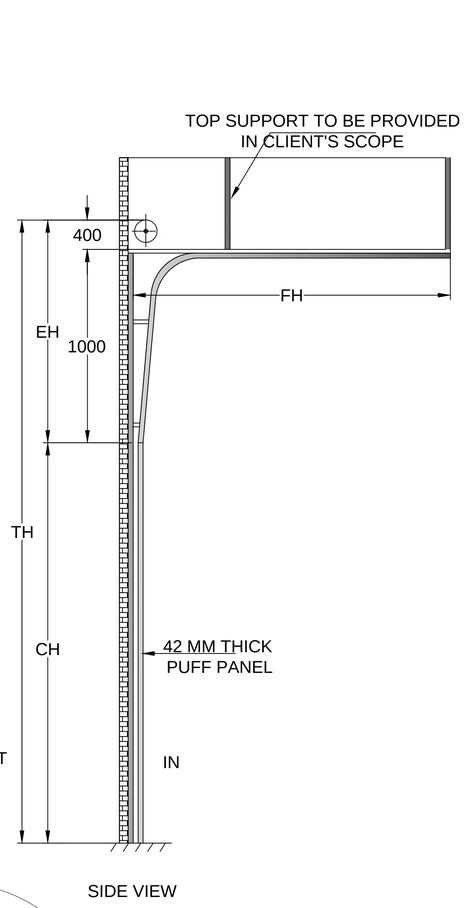

SIDE VIEW

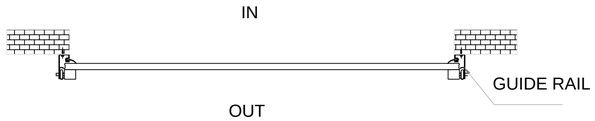

PLAN

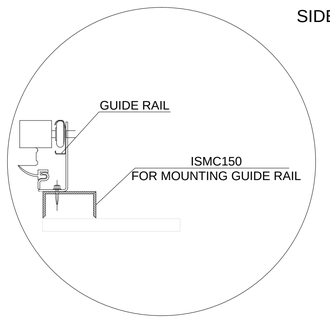

TRACK DETAILS

SR NO	CLEAR WIDTH (CW)	CLEAR HEIGHT (CH)	QUANTITY	EH	FH	TH	LOCATION
1	3000	3000	1	1400	2800	4400	

NOTE- 1. STRUCTURE REQUIRED FOR SECTIONAL DOOR SHALL BE IN CLIENT'S SCOPE.
2.COLOR FOR SECTIONAL DOOR PANEL WOULD BE RAL 5012(LIGHT BLUE)

This drawing & design is the property of NIHVA TECHNOLOGIES. Not be sold or copy to any other concern.

TITLE	SECTIONAL DOOR (HIGH LIFT) (MOTORIZED)		NIHVA TECHNOLOGIES PVT. LTD. PUNE Tel : 020 66304033 Email:- info@nihva.com Website:- www.nihva.com
	SIGN	DATE	
DRAWN	OMKAR	31/07/17	CLIENT - SCON PROJECTS
CHECK	SHEKHAR	31/07/17	PROJECT - BEKAERT INDUSTRIES PVT. LTD.
REV.			SITE - RAJANGAON, MIDC
APPROVAL			DWG. NO. : NIHVA/17-18/0143
If any queries contact : projects@nihva.com			SCALE: NTS / WT: / SHEET: 01 OF 01
ALL DIMENSION ARE IN mm			

PRODUCED BY AN AUTODESK EDUCATIONAL PRODUCT