
Prinzipzeichnung RapidProtect RP300

General drawing Rapid Protect RP300

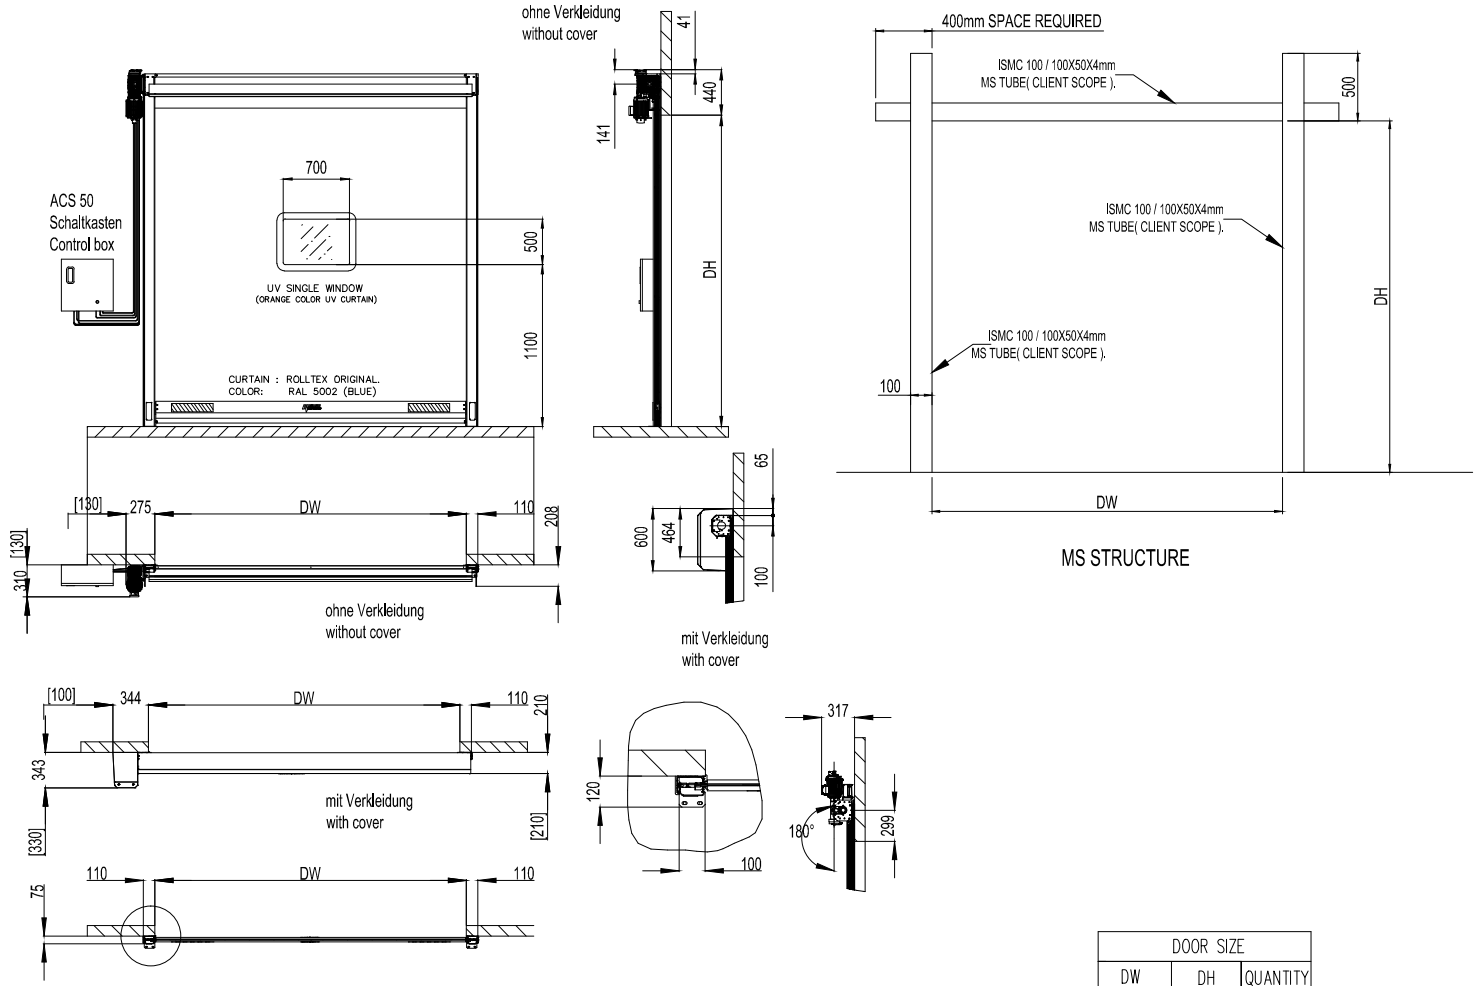

MS STRUCTURE

DOOR SIZE		
DW	DH	QUANTITY
1500	2500	8

Toleranz ±3 mm (gültig für alle Maßangaben) Tolerance ±3 mm (for all dimensions)
Maßangaben in [ ] ==> Montagefreiraum Dimensions in [ ] ==> clearance for installation

NOTE-

1. COLOR : RAL 5002 (BLUE).
2. CURTAIN : ROLLTEX ORIGINAL.
3. REQUIRED STRUCTURE FOR HSD WILL BE IN CLIENT'S SCOPE.

This drawing & designing is the property of NIHVA TECHNOLOGIES. Not be sold or copy to any other concern.

TITLE				
HIGH SPEED DOOR RP 300 & STRUCTURE				
	NAME	SIGN	DATE	
DRAWN	P.A		29.10.2018	
CHECK	R.D		29.10.2018	
REV.	V.T		29.10.2018	
APPROVAL				

NIHVA TECHNOLOGIES PVT. LTD.
Website:- www.nihva.com

NIHVA TECHNOLOGIES PVT. LTD. PUNE
Tel : 020 66304033
Email:- info@nihva.com

CLIENT -

PROJECT -

SITE -

DWG. NO. : NIHVA/18-19/VDR/0186 REV:- 0

SCALE: NTS WT: SHEET: 01 OF 01

If any queries contact : sales@nihva.com

ALL DIMENSIONS ARE IN mm