

Drawing issued for
Discussion / Information

The Drawing is based on original design proposal & prepared by AHU & supplied to us by Bharma Corp Ltd. No information on this drawing is a design intent,outlined by us. DMA is solely issuing this drawing with reference to micro detailing work to help site excecution. We intent not to deviate from original design intent as instructed by client.

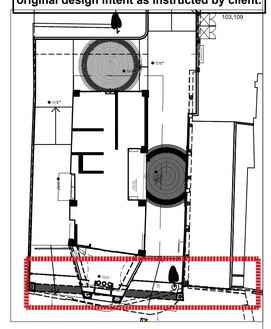


Key

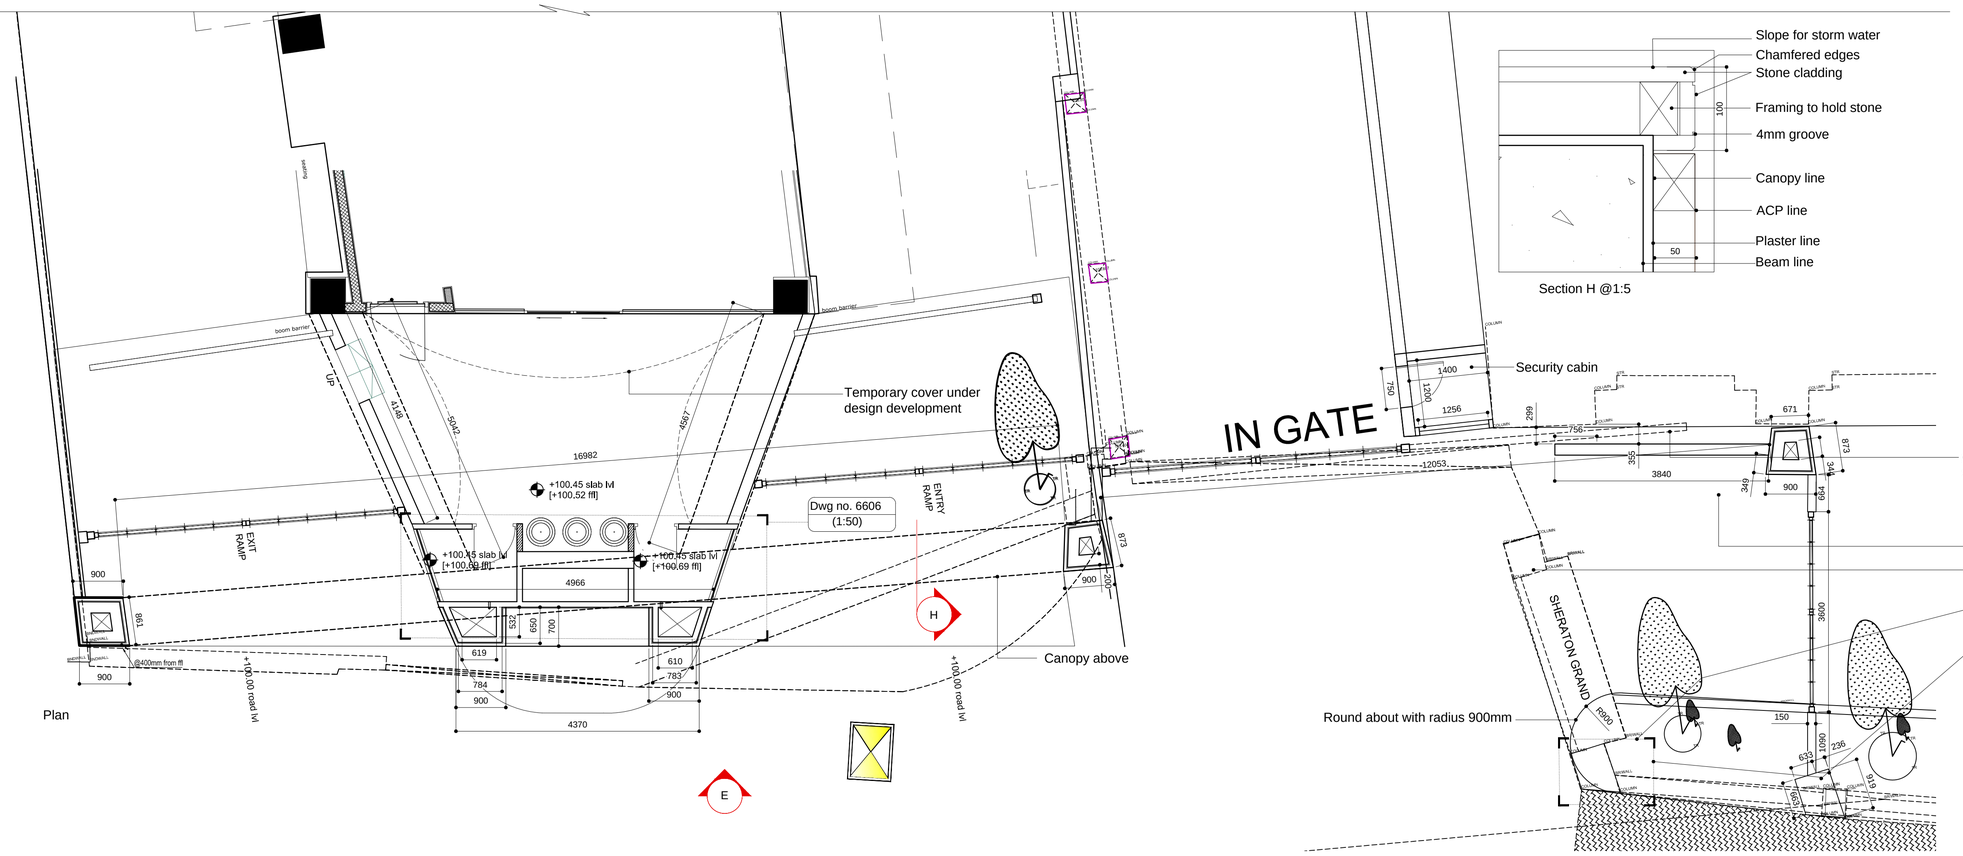


Plan

Section H @1:5

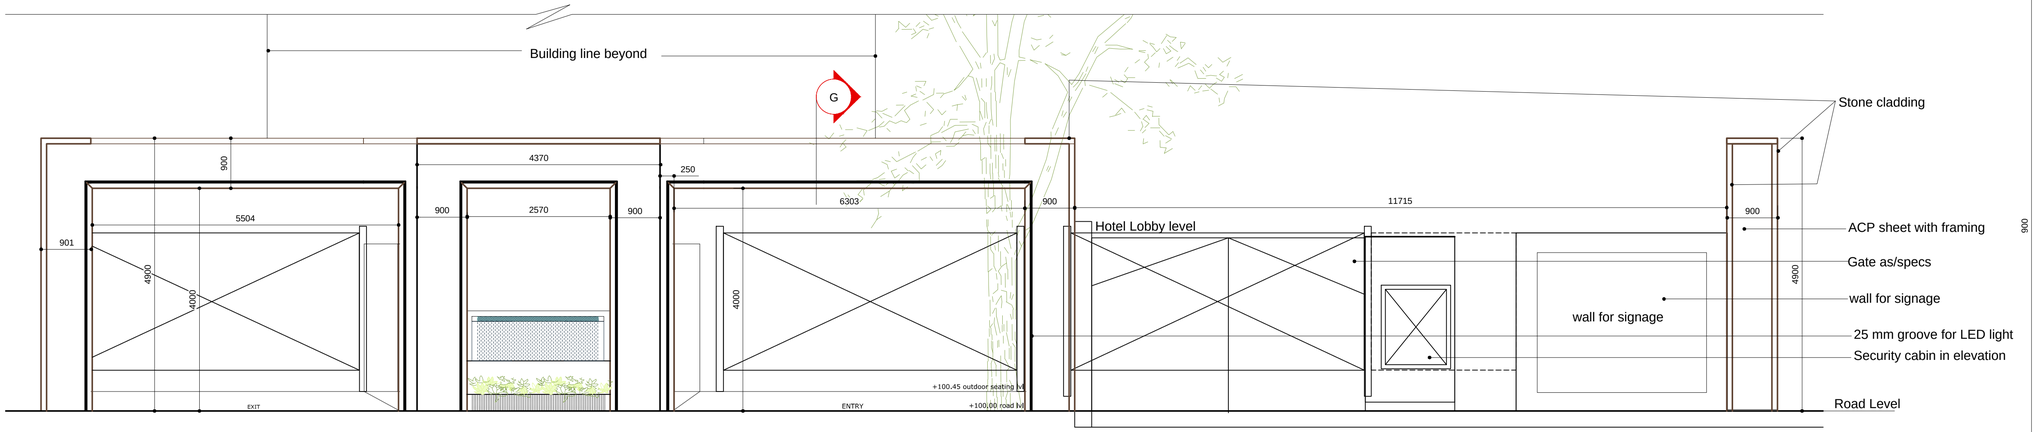

Elevation E

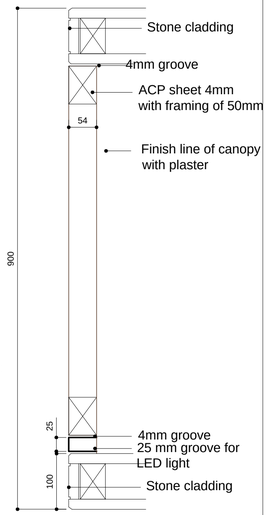

Section G(1:7)

- This drawing is a property of **DARSHAN MEDHI ARCHITECTS** , and is not to be used or reproduced without their written permission.
- The contractor must verify all the dimensions of the job and report any dimensional and other discrepancies to the architect.
- Do not scale the drawing
- All dimensions to be checked on site
- Refer Structural engineers information for details on tolerance, movment and construction joints
- Refer structural drawings and specifications for all structural information
- Refer MEP drawings and specifications for all MEP information

Date	Ref.	Revision

Project - Office building for Brahma Corp

Subject - South Compound wall design

Scale - 1:75@A2

Date - 2023-12-19

Architects - **DARSHAN MEDHI ARCHITECTS** 201 Archway, Sopanbaug, Balewadi Highstreet, Pune 45 **E** - dma@dmastudio.com

Sort code		Dwg No.	Rev.
OBBS	**CS**	**6605**	**-**