


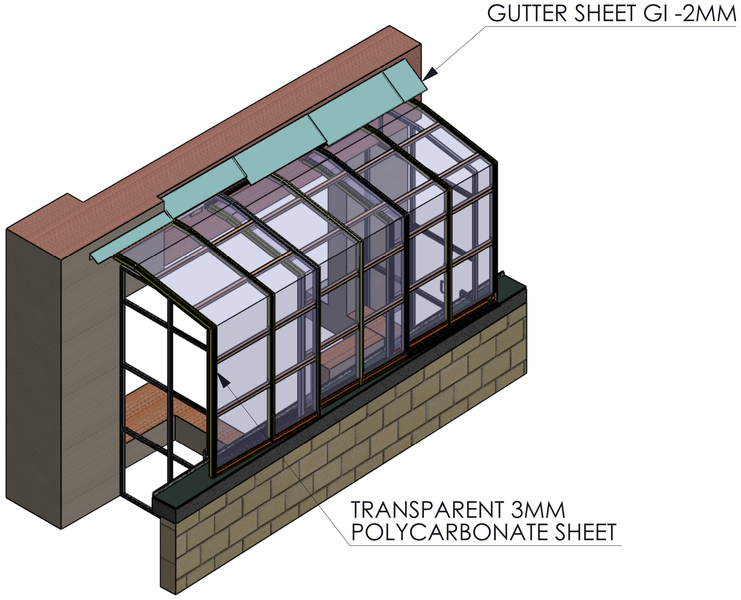


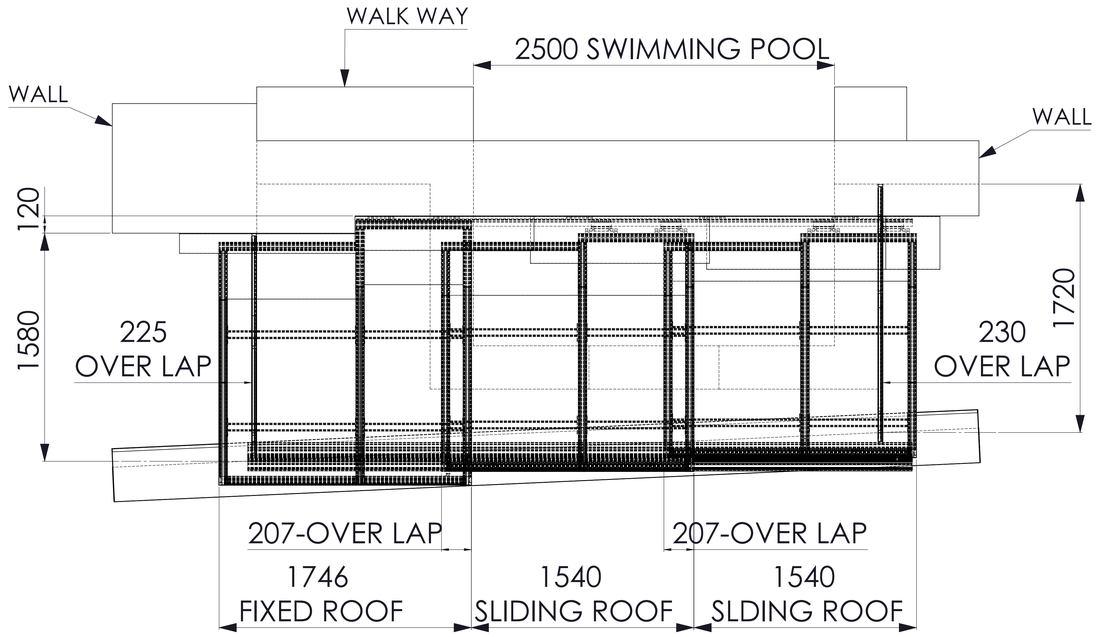

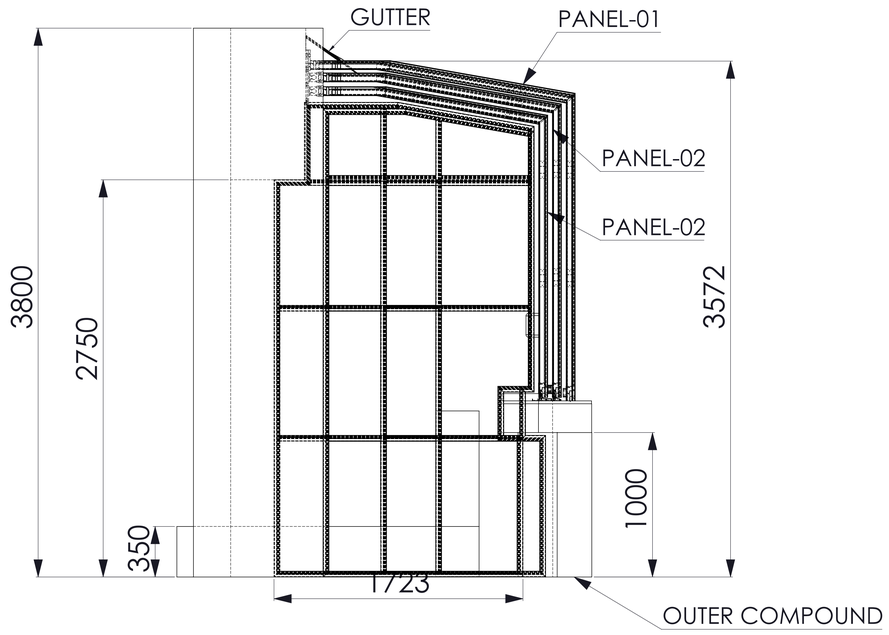

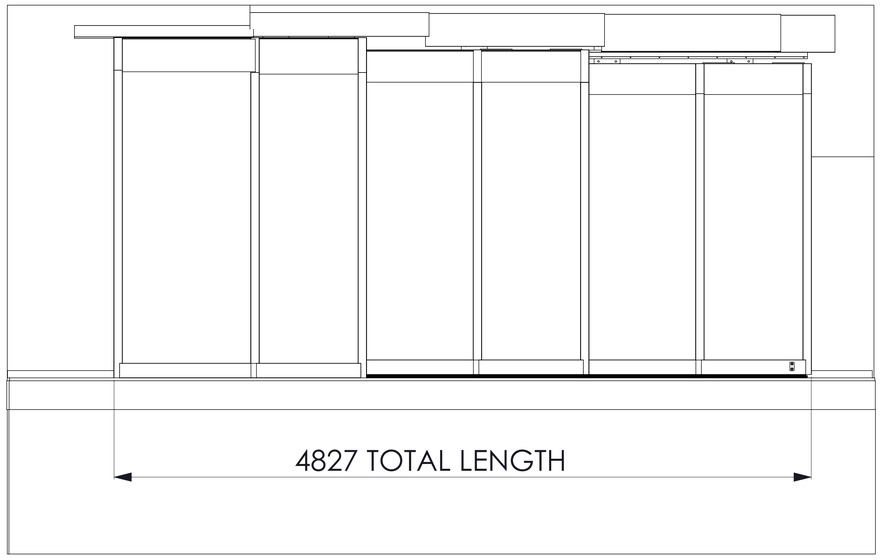

NOTE:
RAL CODE-

This drawing & design is the property of NIHVA TECHNOLOGIES. Not to be sold or copied to any other concern.

PRODUCT:-
MANUALLY RETRACTABLE BALCONY ENCLOSURE

QTY - 1 NOS

NIHVA
NIHVA TECHNOLOGIES PVT. LTD.

NAME	SIGN	DATE	
DRAWN	B.B	25/06/24	
CHECK	B.B	25/06/24	
APPRD.	V. T.	25/06/24	

CLIENT - NTPL - 2028

LOCATION - PUNE


PRODUCT - BALCONY ENCLOSURE

DWG NO - 2024-NTPL-2028-MAY-BLEN REV -02

ALL DIMENSION ARE IN mm

SCALE:

SHEET:

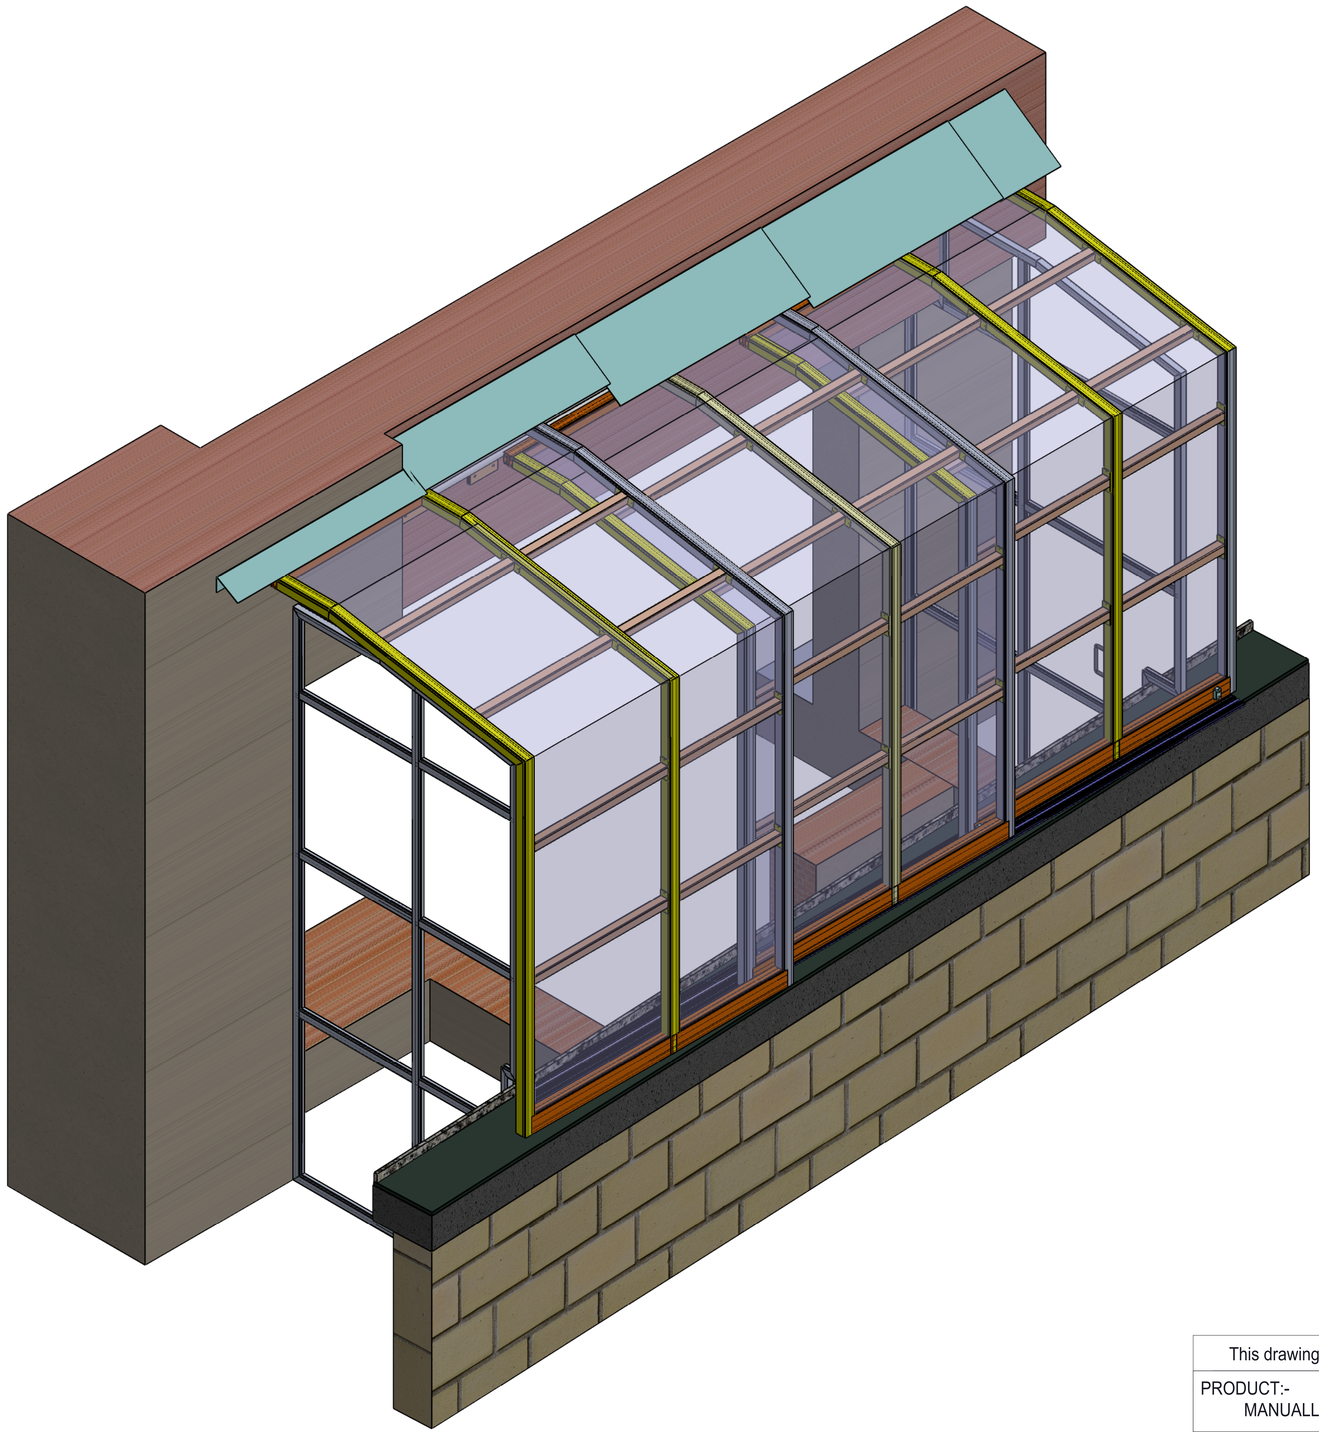

This drawing & design is the property of NIHVA TECHNOLOGIES. Not to be sold or copied to any other concern.

PRODUCT:-
MANUALLY RETRACTABLE BALCONY ENCLOSURE

QTY - 1 NOS

NIHVA
NIHVA TECHNOLOGIES PVT. LTD.

NAME	SIGN	DATE	
DRAWN	B.B	25/06/24	
CHECK	B.B	25/06/24	
APPRD.	V. T.	25/06/24	

CLIENT - NTPL - 2028

LOCATION - PUNE


PRODUCT - BALCONY ENCLOSURE


DWG NO - 2024-NTPL-2028-MAY-BLEN REV -02


ALL DIMENSION ARE IN mm


SCALE:


SHEET:

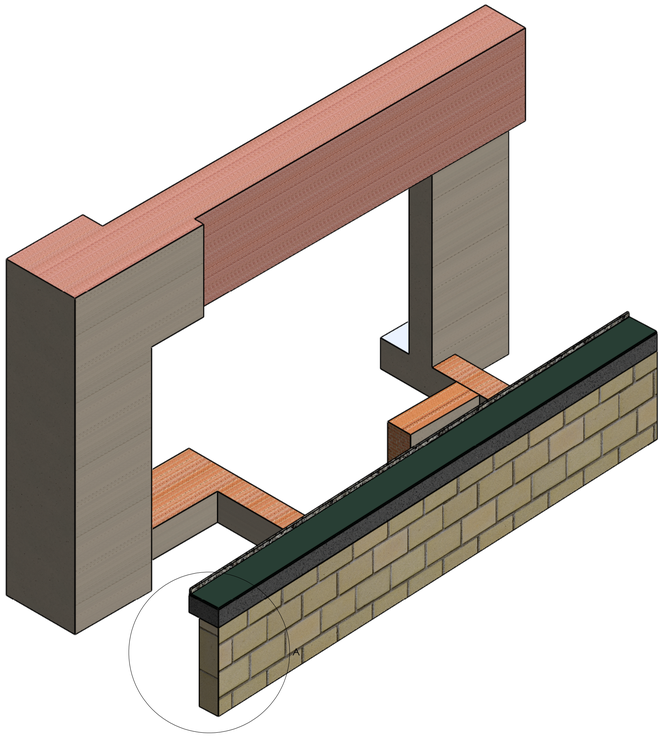

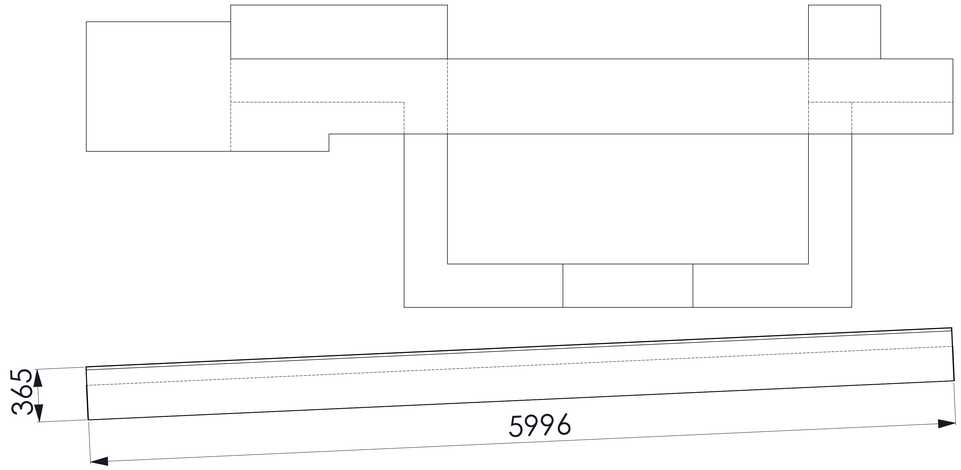

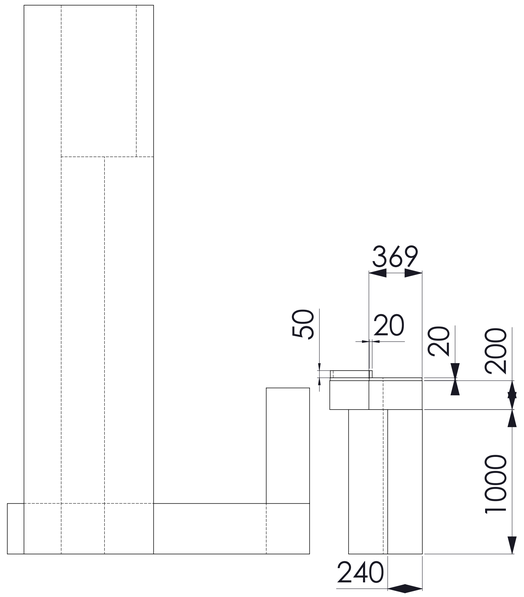

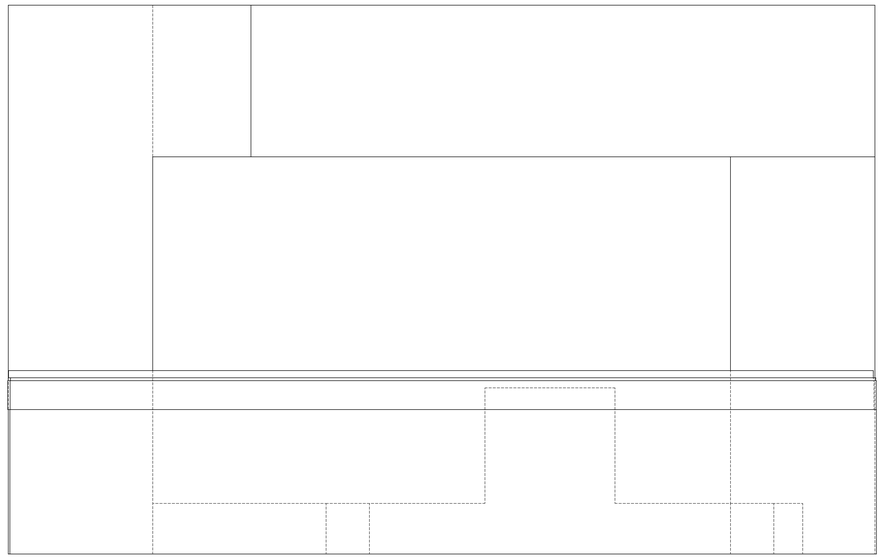

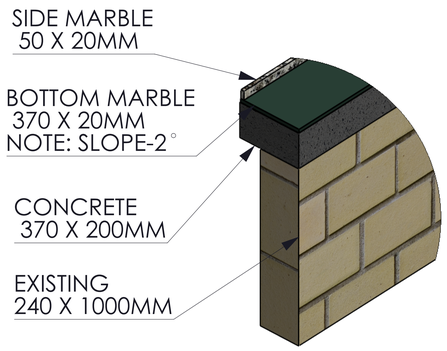

DETAIL A
SCALE 1 : 10

This drawing & design is the property of NIHVA TECHNOLOGIES. Not to be sold or copied to any other concern.

PRODUCT:-
BALCONY ENCLOSURE CIVIL DRAWING

QTY - 1 NOS

NAME	SIGN	DATE	
DRAWN	B.B	25/06/24	
CHECK	B.B	25/06/24	
APPRD.	V. T.	25/06/24	

NIHVA
NIHVA TECHNOLOGIES PVT. LTD.

CLIENT - NTPL - 2028

LOCATION - PUNE

PRODUCT - BALCONY ENCLOSURE

DWG NO - 2024-NTPL-2028-MAY-BLEN REV -02

ALL DIMENSION ARE IN mm

SCALE:

SHEET: