
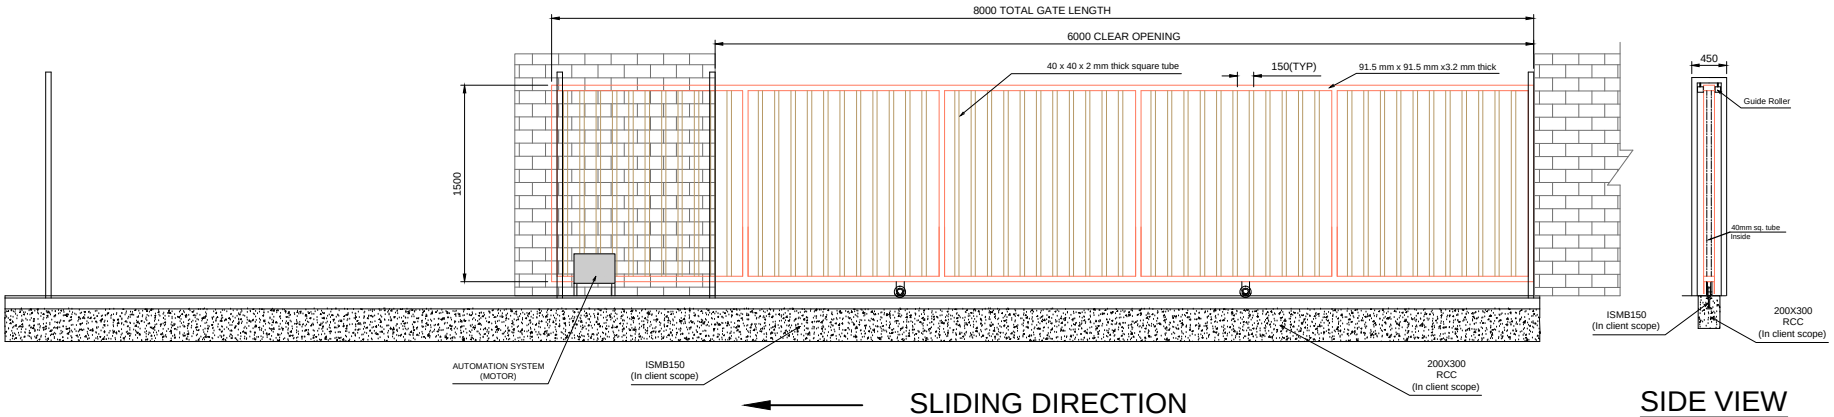


SLIDING DIRECTION

INSIDE VIEW

SIDE VIEW

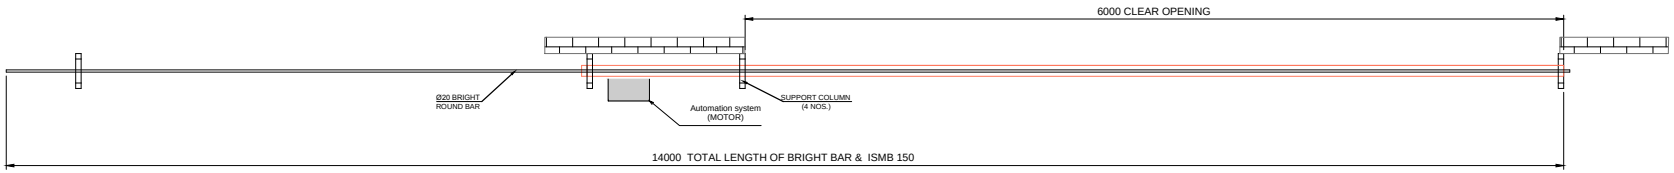

TOP VIEW

Clear Opening size - 6000X1500mm
Total length of gate - 8000X1500mm
No. Of Column - 4 nos.
Factory paint finish - Red oxide primer coat
NOTE :- Supply of 'c' channel for vertical support of gate in NIHVA scope
*Excavation and civil work for grouting of 'c' channel & I beam will be in client scope.

This drawing & designing is the property of NIHVA TECHNOLOGIES. Not be sold or copy to any other concern.

TITLE	MOTORIZED SLIDING GATE		NIHVA TECHNOLOGIES PVT. LTD.
	SIGN	DATE	
DRAWN	ABHIJIT	22/09/15	CLIENT - REWARD CONSTRUCTION
CHECK	ANIL	22/09/15	PROJECT - GIVAUDAN
REV.	01		SITE - RANJANGAON MIDC
APPROVAL			DWG. NO. : NIHVA/15-16/082
If any queries contact : projects@nihva.com			SCALE: 01 / WT: / SHEET: 01 OF 01
ALL DIMENSION ARE IN mm			

NIHVA TECHNOLOGY PVT. LTD. PUNE
Tel : 020 66304033
Email:- info@nihva.com
Website:- www.nihva.com